

AGORA

CLICK・KICK

By Kengo Kuma & Associates


FASE 2. IDEA BÁSICA


LOCALIZACIÓN

[Venue Building] Click Clack by Kengo Kuma



ESTADO ACTUAL

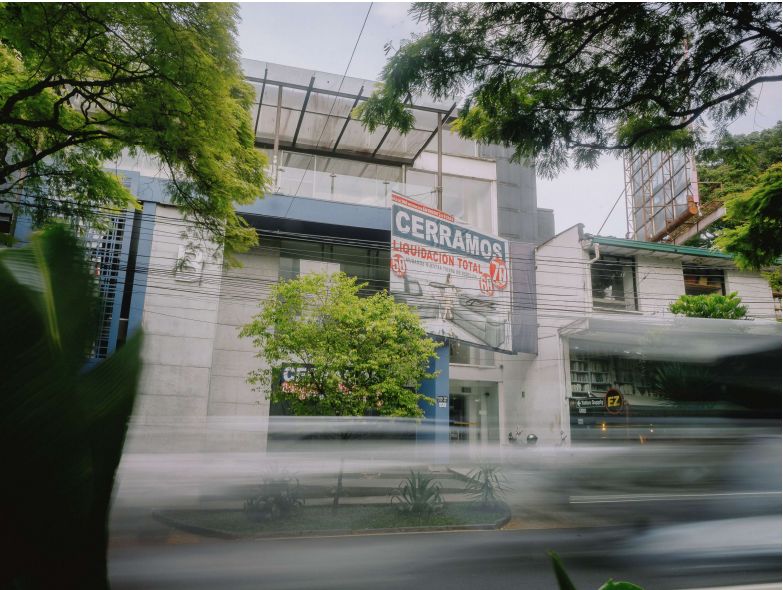

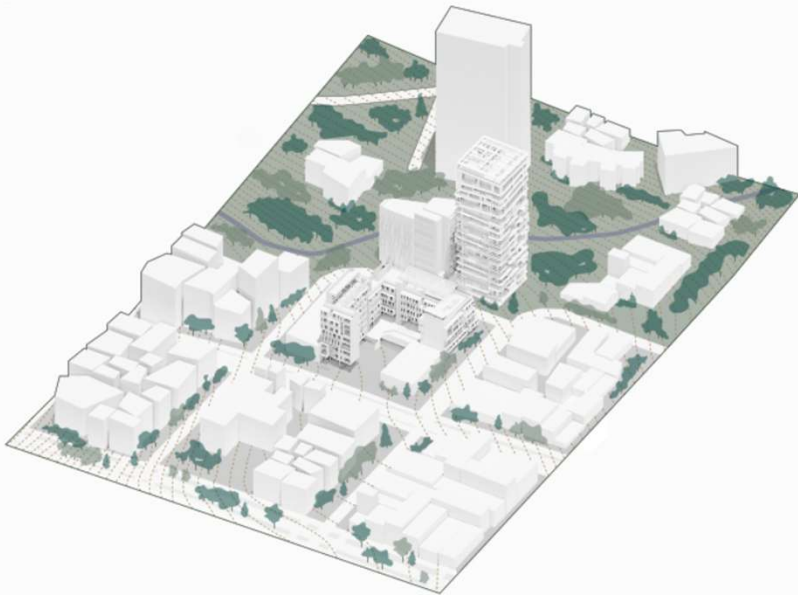

Site

A Green Back, A lush jacket, the presence of water, an urban front



Scale

What are we now and what is next


DISTRIBUCIÓN LOTES

LOTE 1 = Hotel Click Clack 1
 LOTE 2 = Hotel Click Clack 2
 LOTE 3 = Ágora Click Clack

Cada edificio debe ser independiente estructuralmente y en evacuación.

INVERSORES 1 = Hotel Click Clack 1 + 2
 INVERSORES 2 = Ágora Click Clack

ADMINISTRACIÓN KK = Hotel KK 1 + 2 +
 Ágora KK

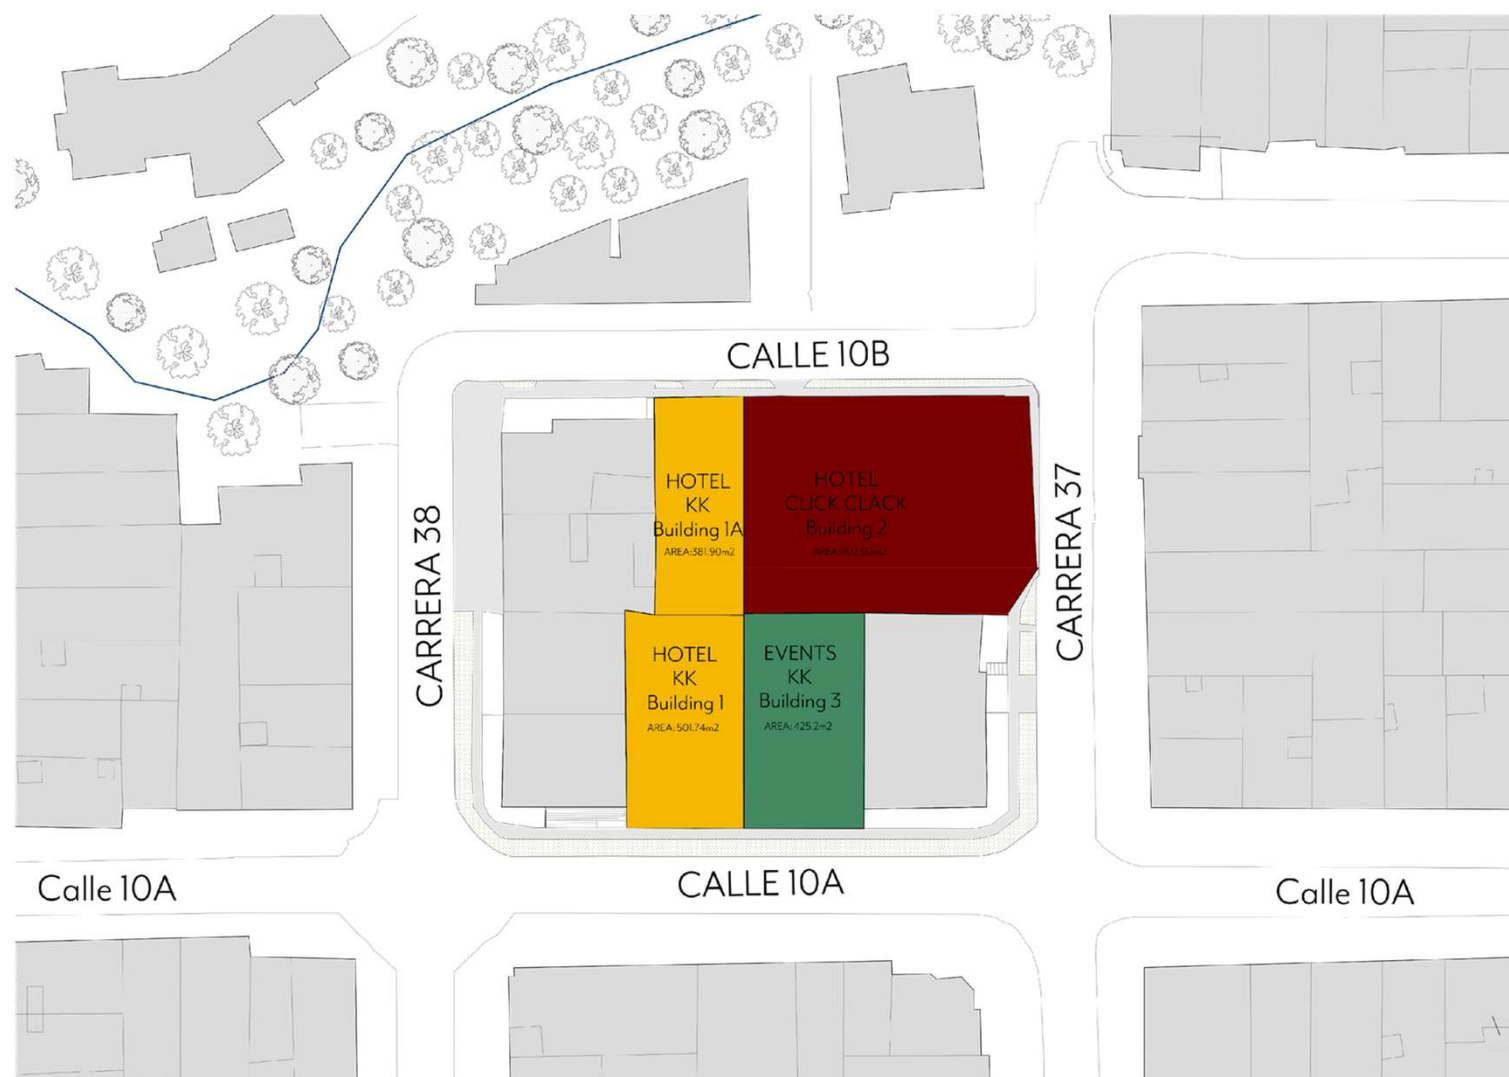

[Venue Building] Click Clack by Kengo Kuma

TODO ES UN PAISAJE

6


[Venue Building] Click Clack by Kengo Kuma

::


Enero
'26

!


confidential

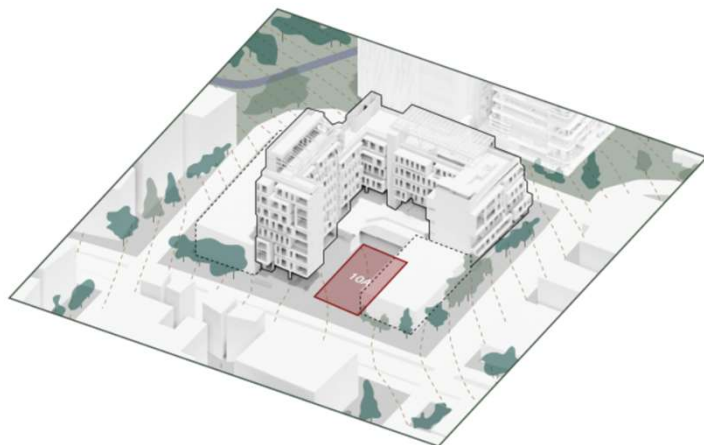


10A
The Boundaries of the plot

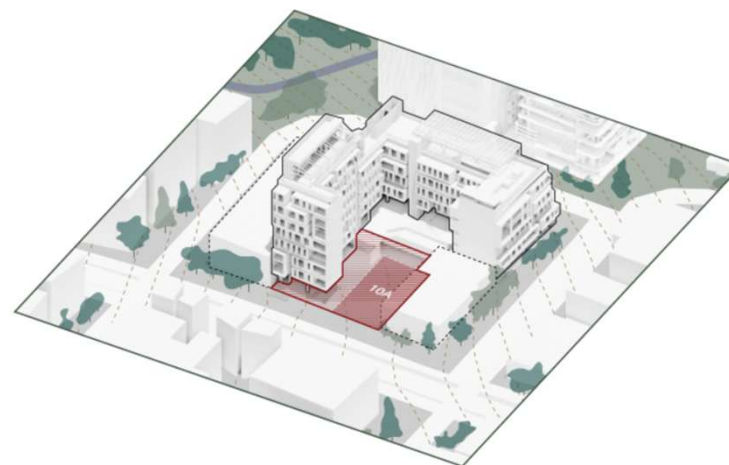

Not an Island
Enhanced front, and infrastructure facilitator

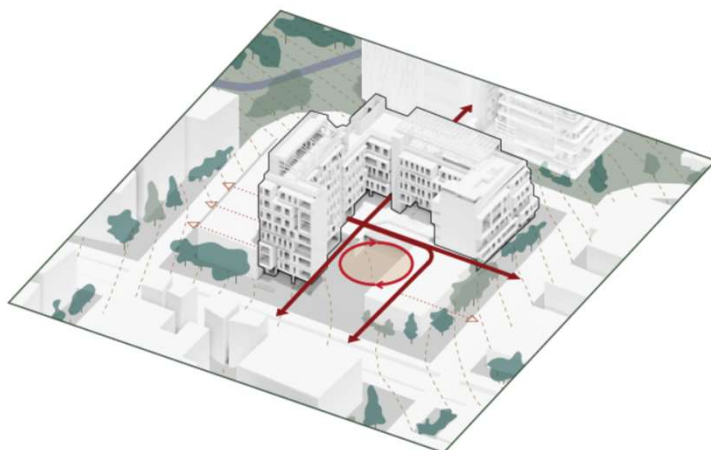

A Vortex
The flow of guests, visitors and staff will revolve around 10A

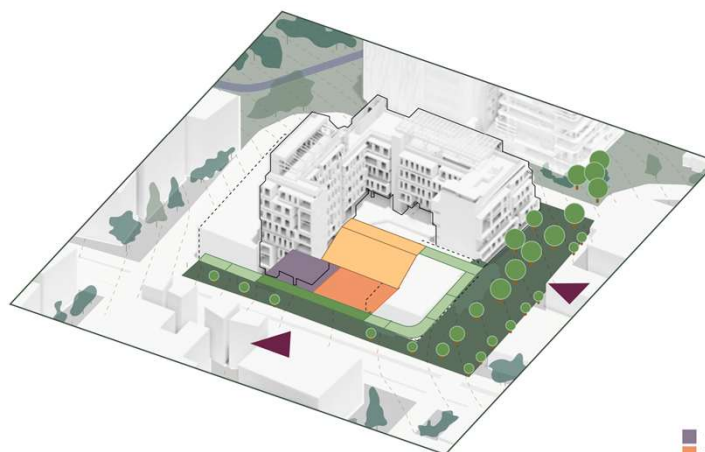

Blending
Court - Stage - Fronts as a whole

- Gallery
- 10A Stage
- Terraced Buffer
- ▲ Click Clack Faces
- Shared Zone

TODO ES UN ESCENARIO

7


[Venue Building] Click Clack by Kengo Kuma

::

Enero
'26


!

confidencial

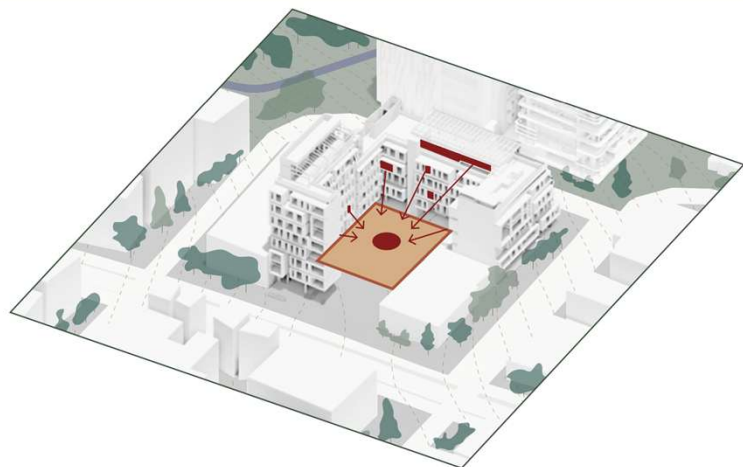


Open-Air

Turning all CKCK rooms into private theater lounges

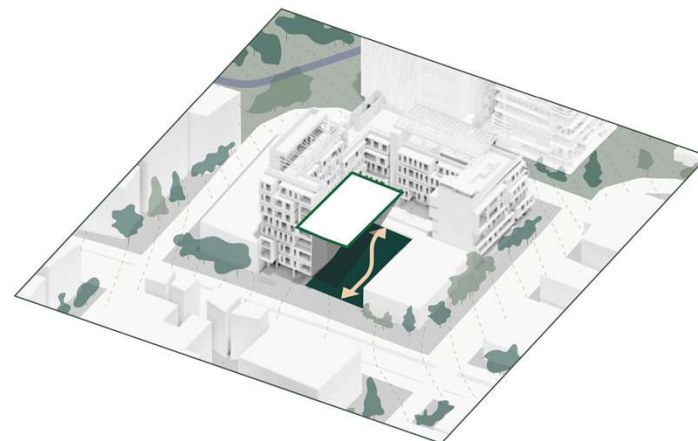

Covered

A flexible performative space for music / concerts / exhibitions / everyday life

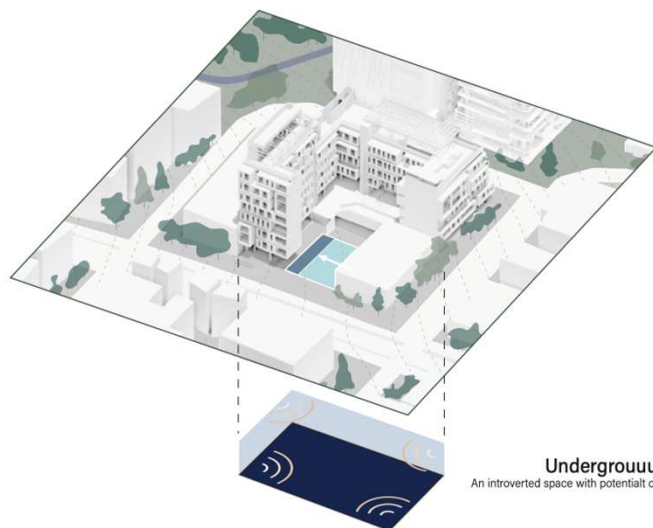


Undergrouuund


An introverted space with potentialt connections to above





PLANIMETRÍA


-  OBRA NUEVA EN LOTE NUEVO
-  OBRA NUEVA EN LOTE EXISTENTE
-  REFORMA EN LOTE EXISTENTE

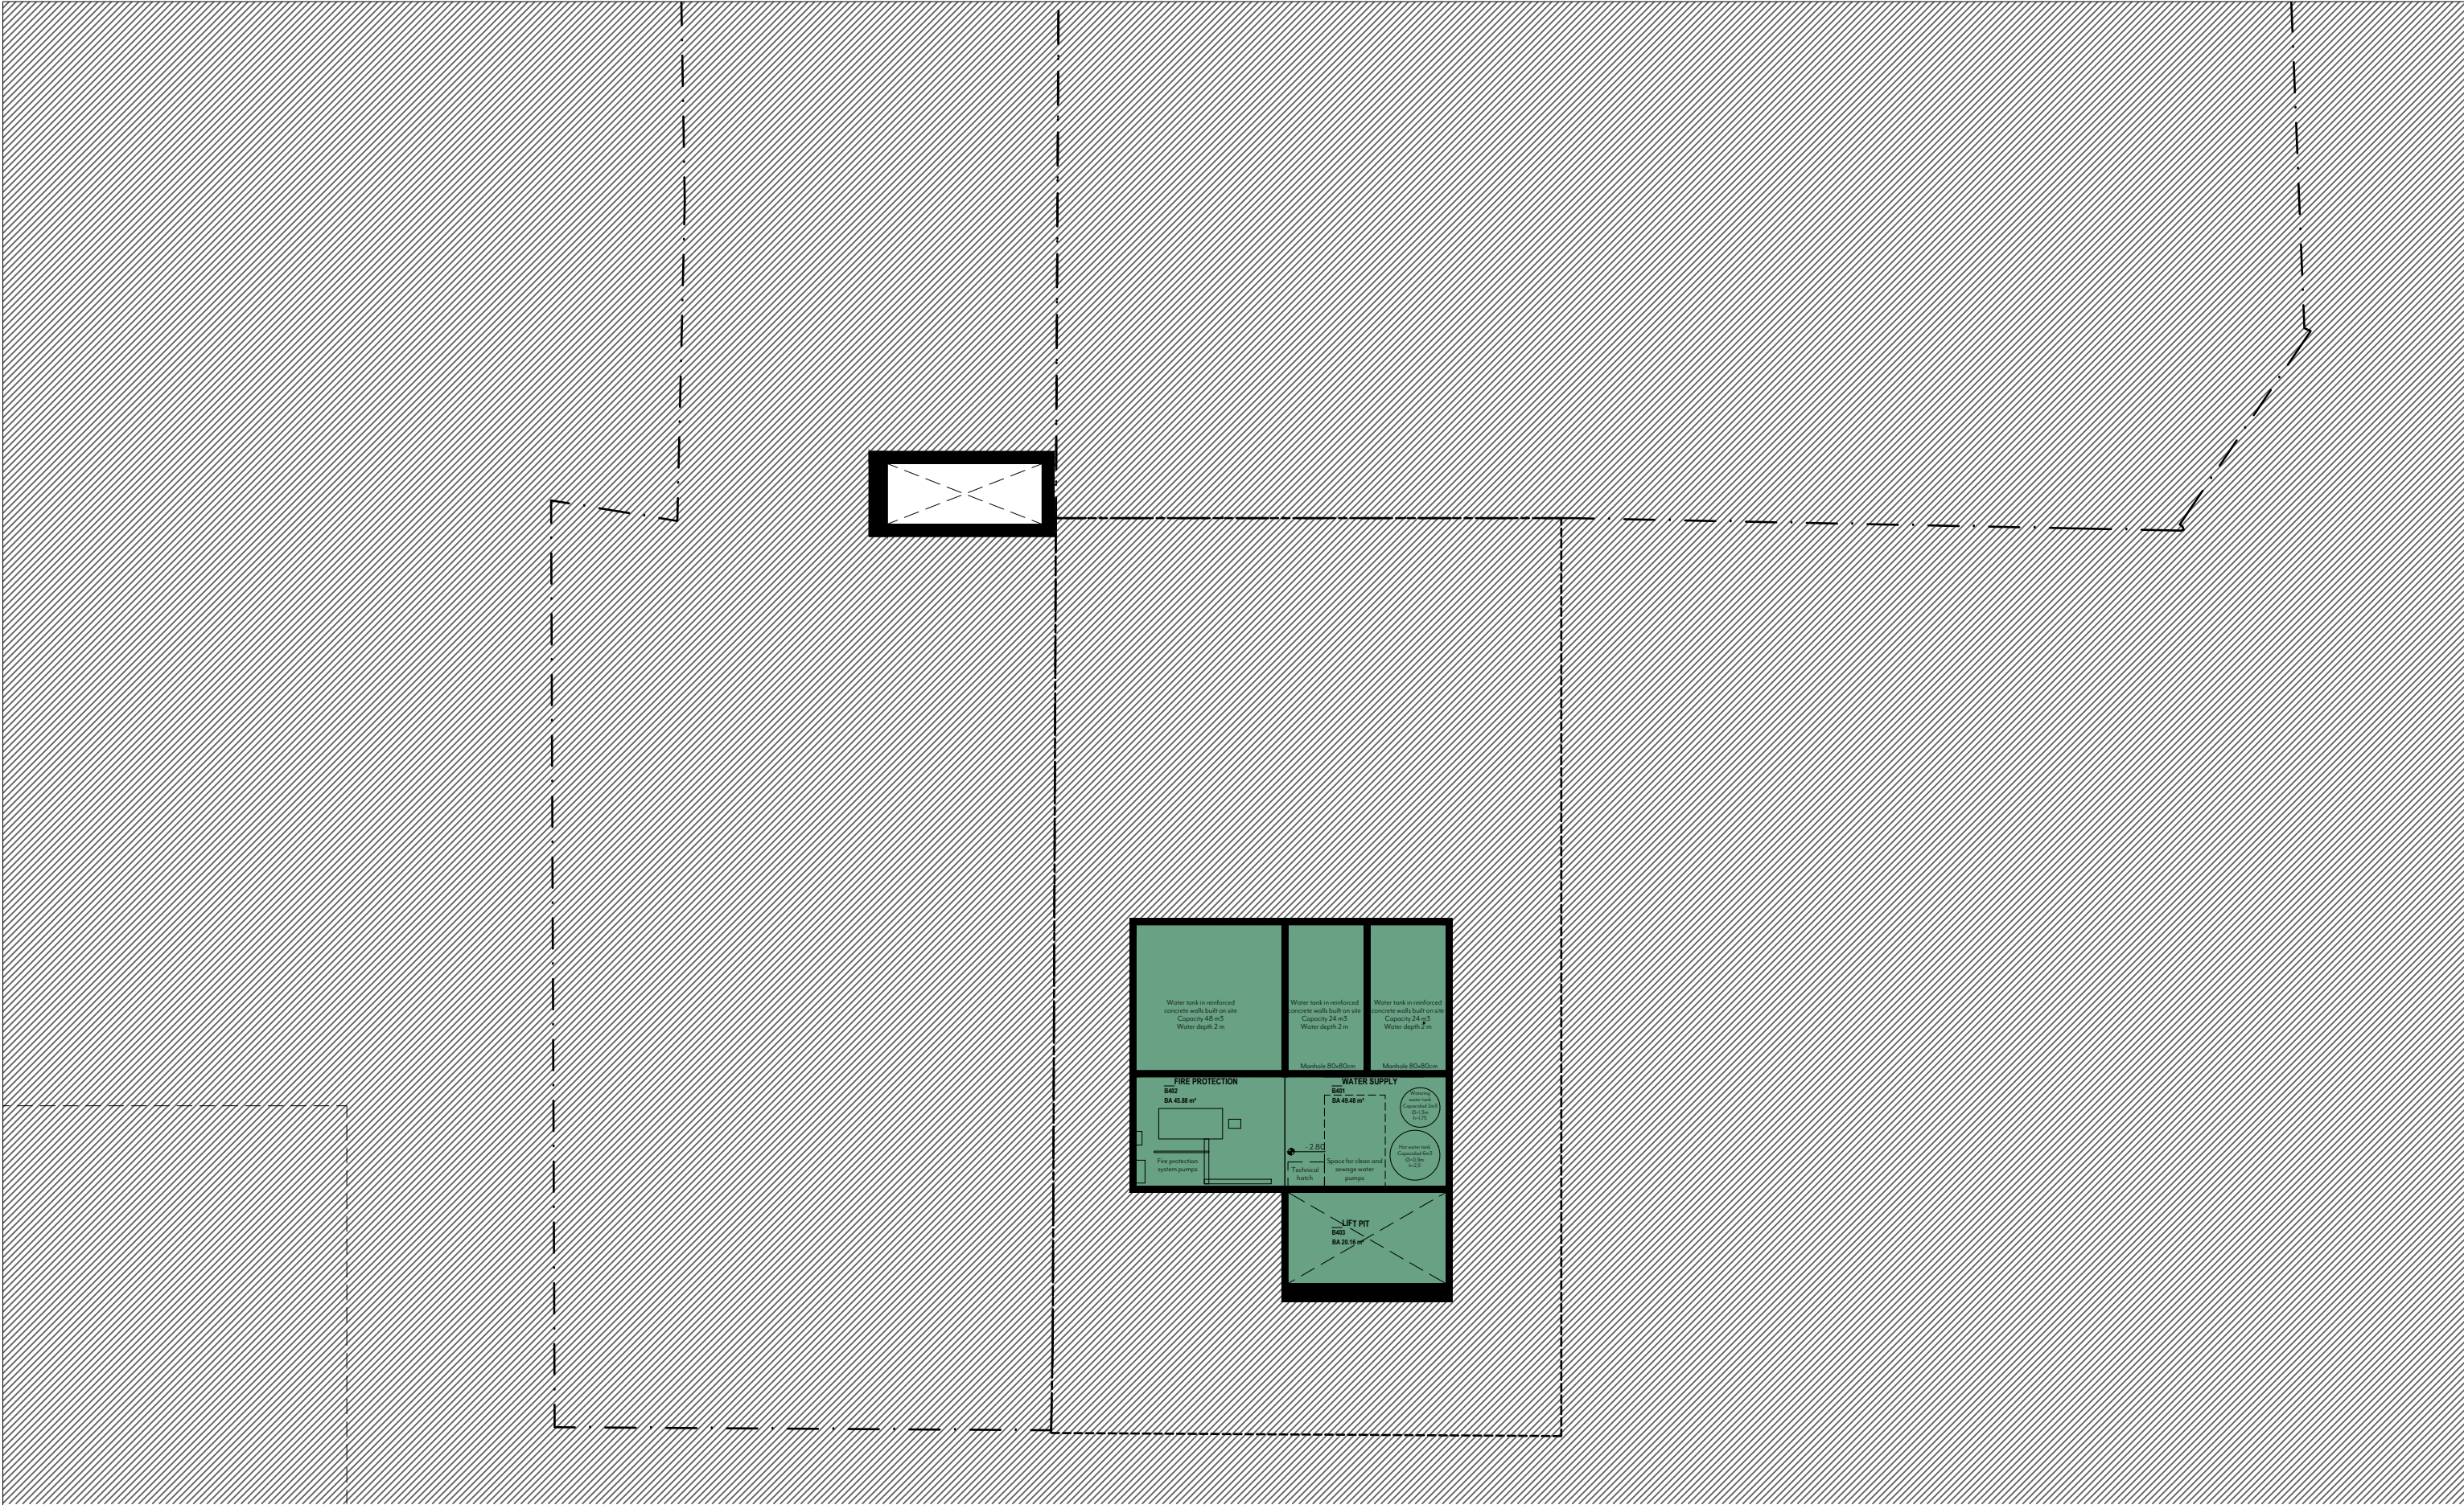


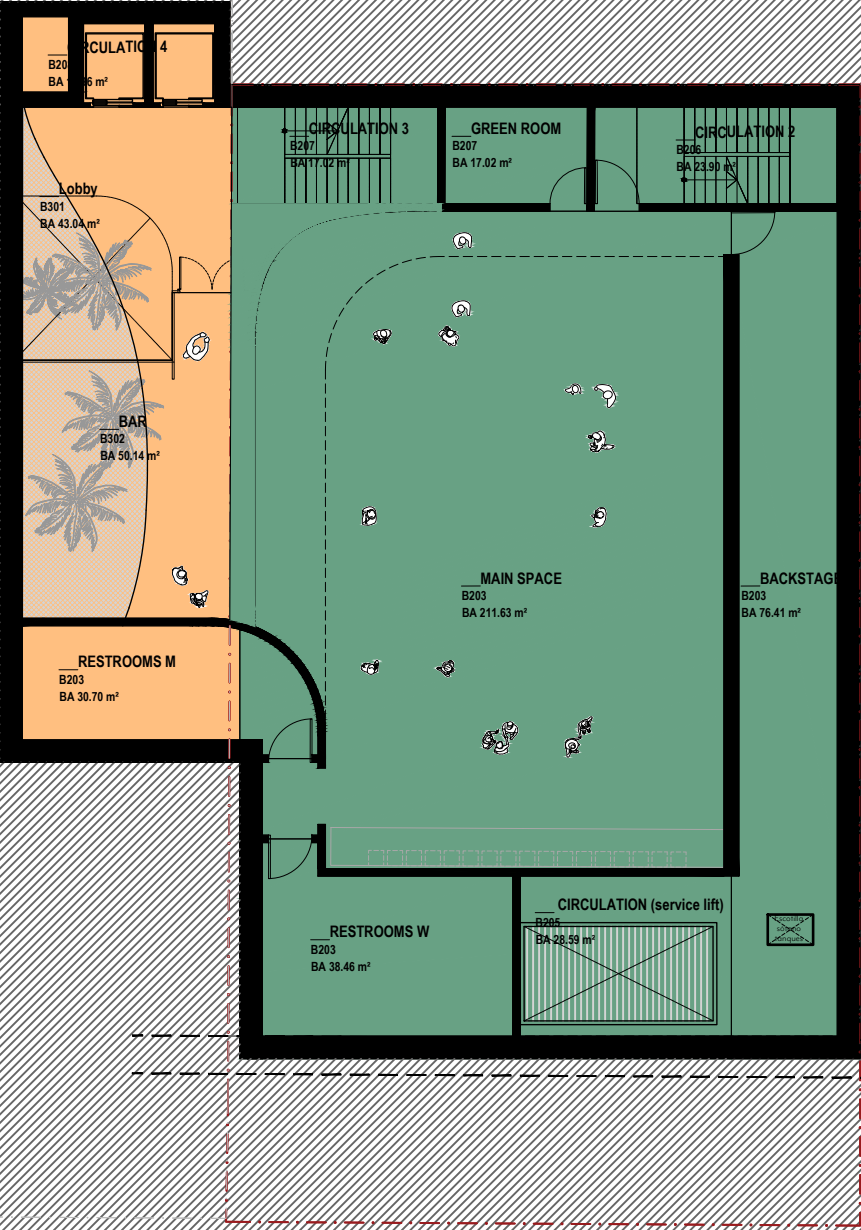

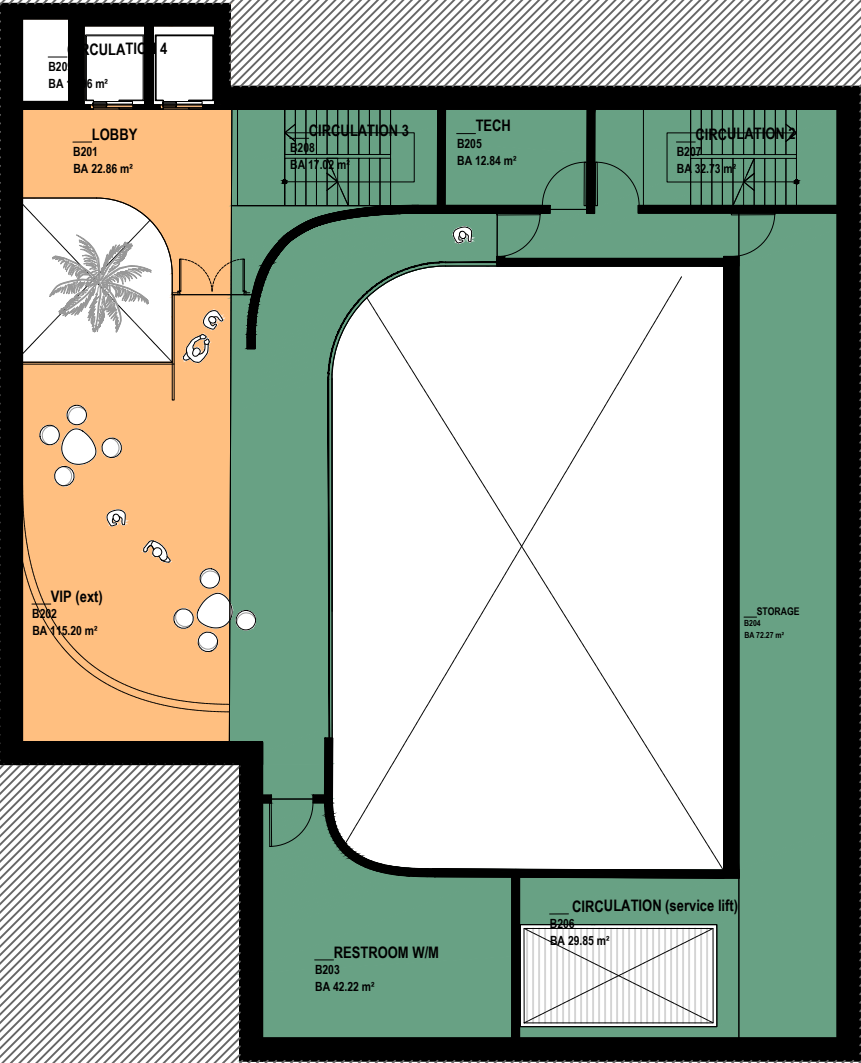

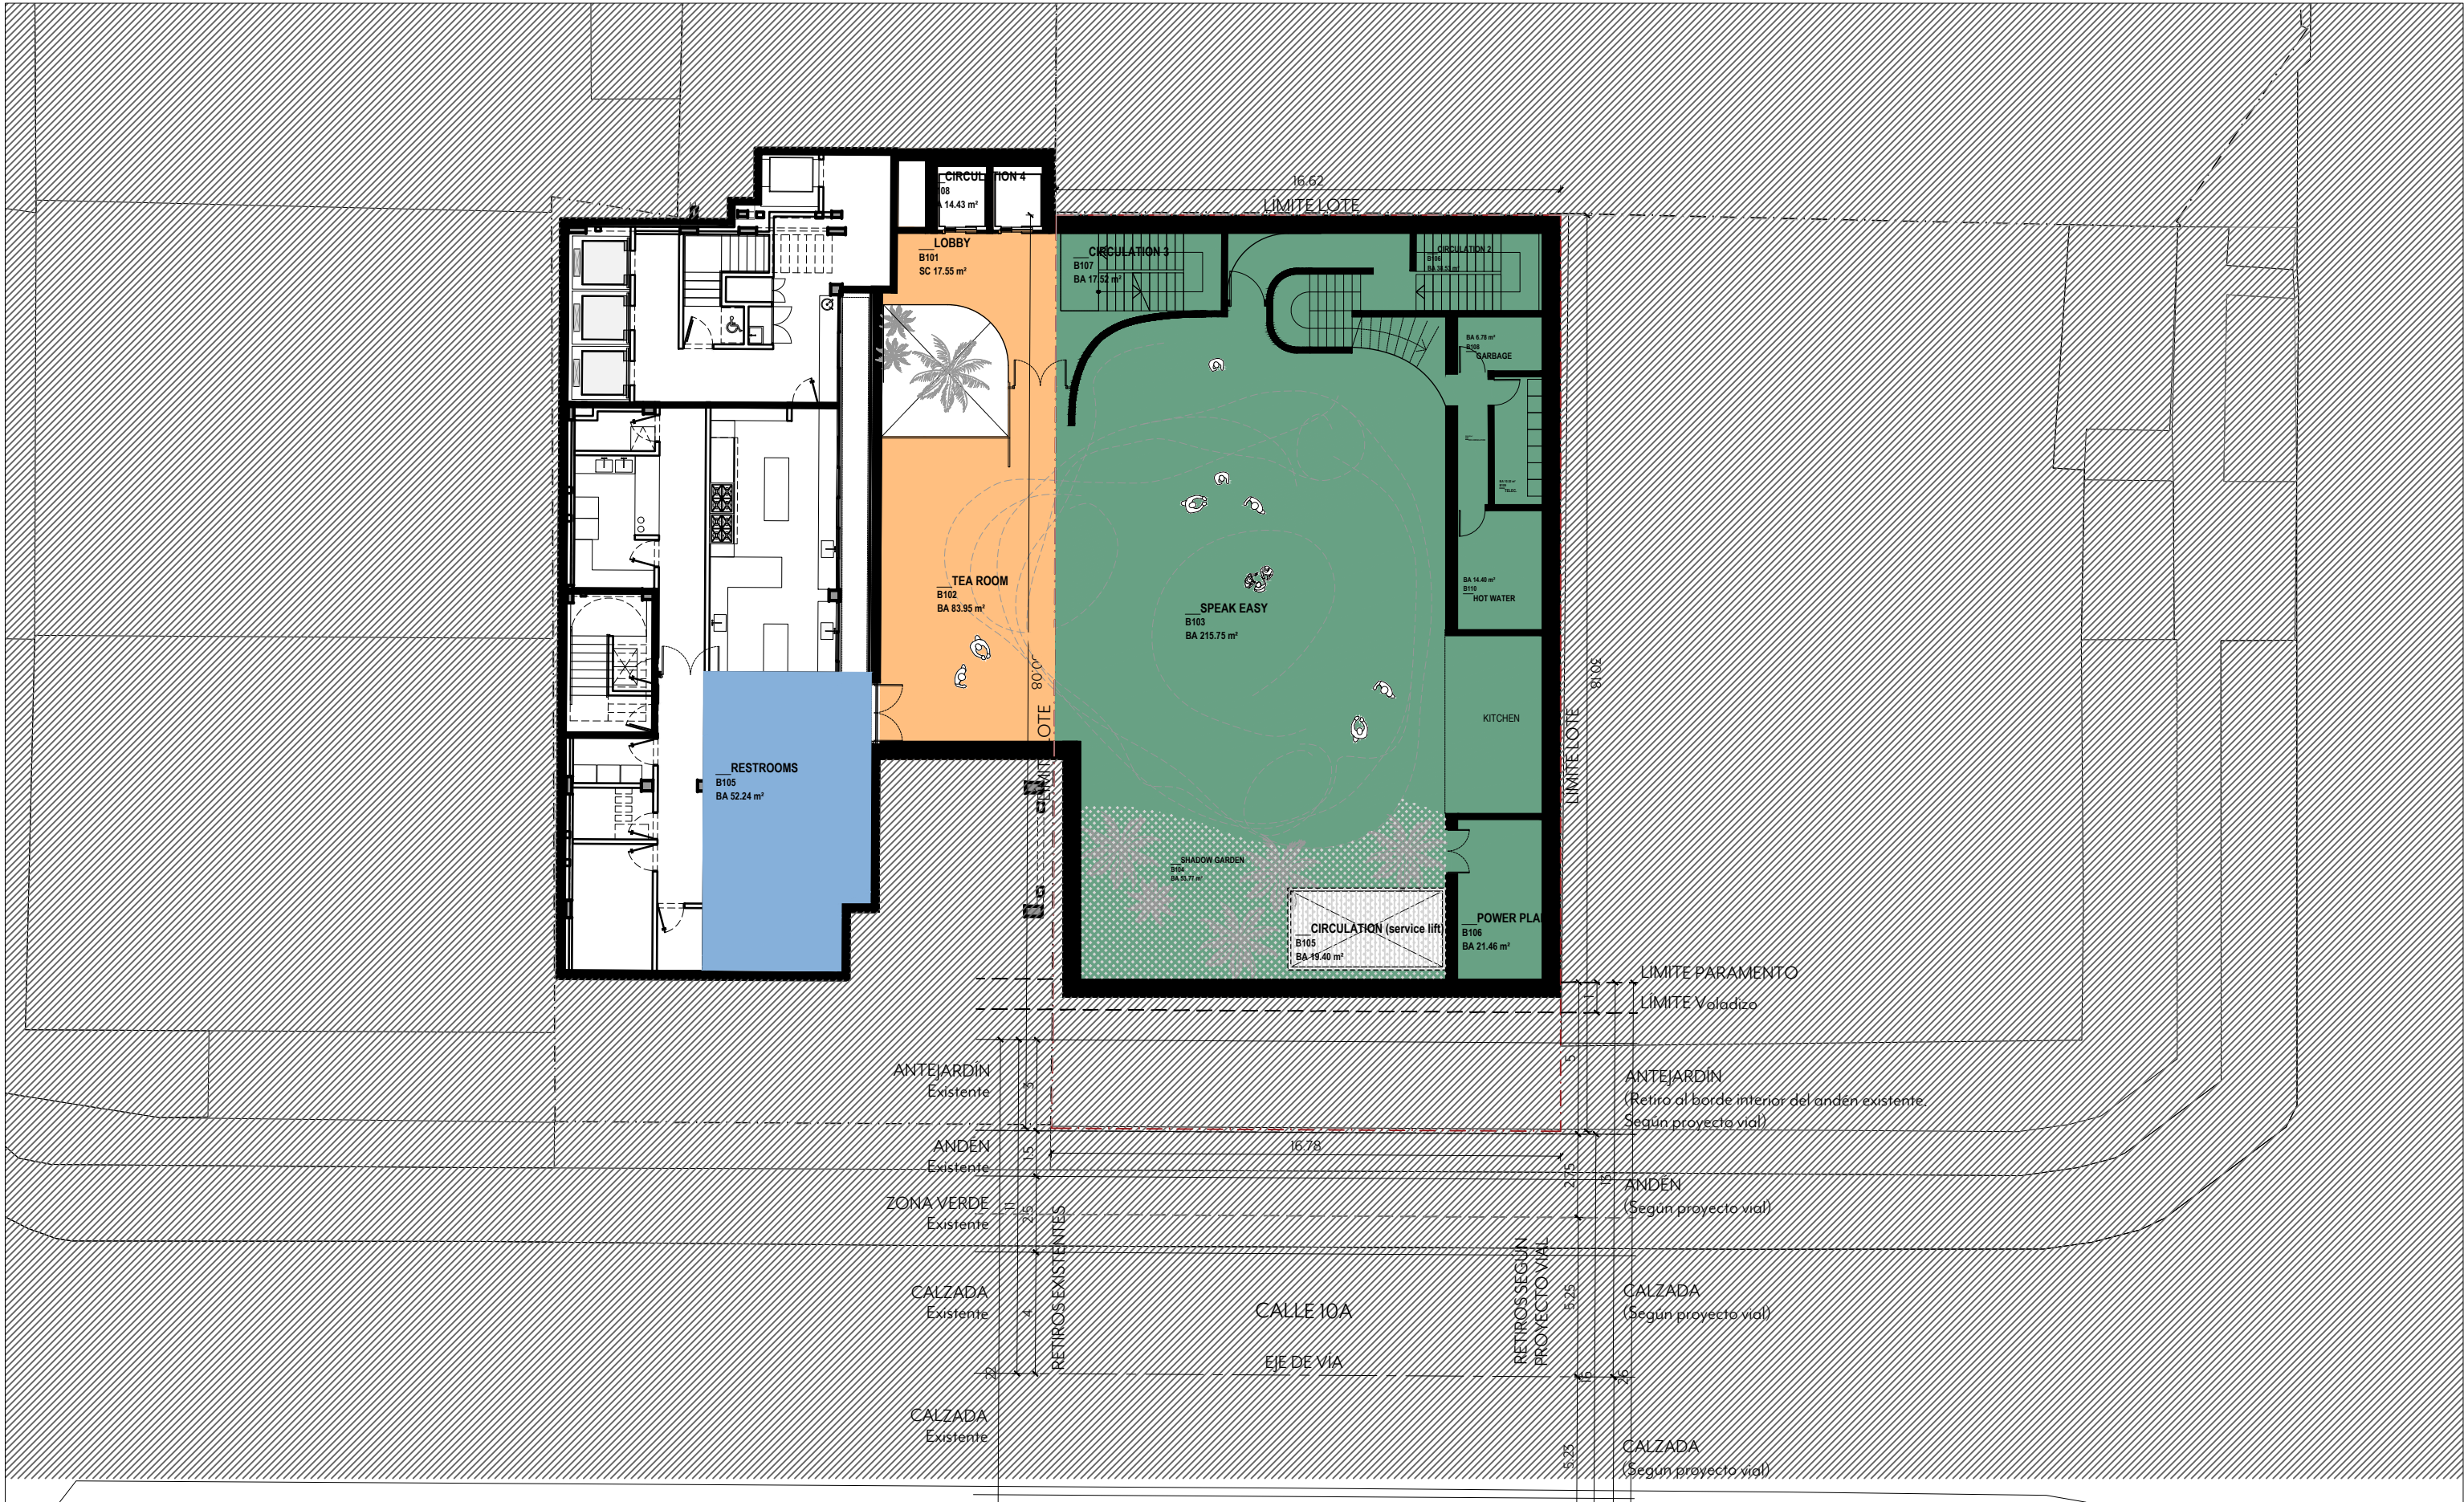

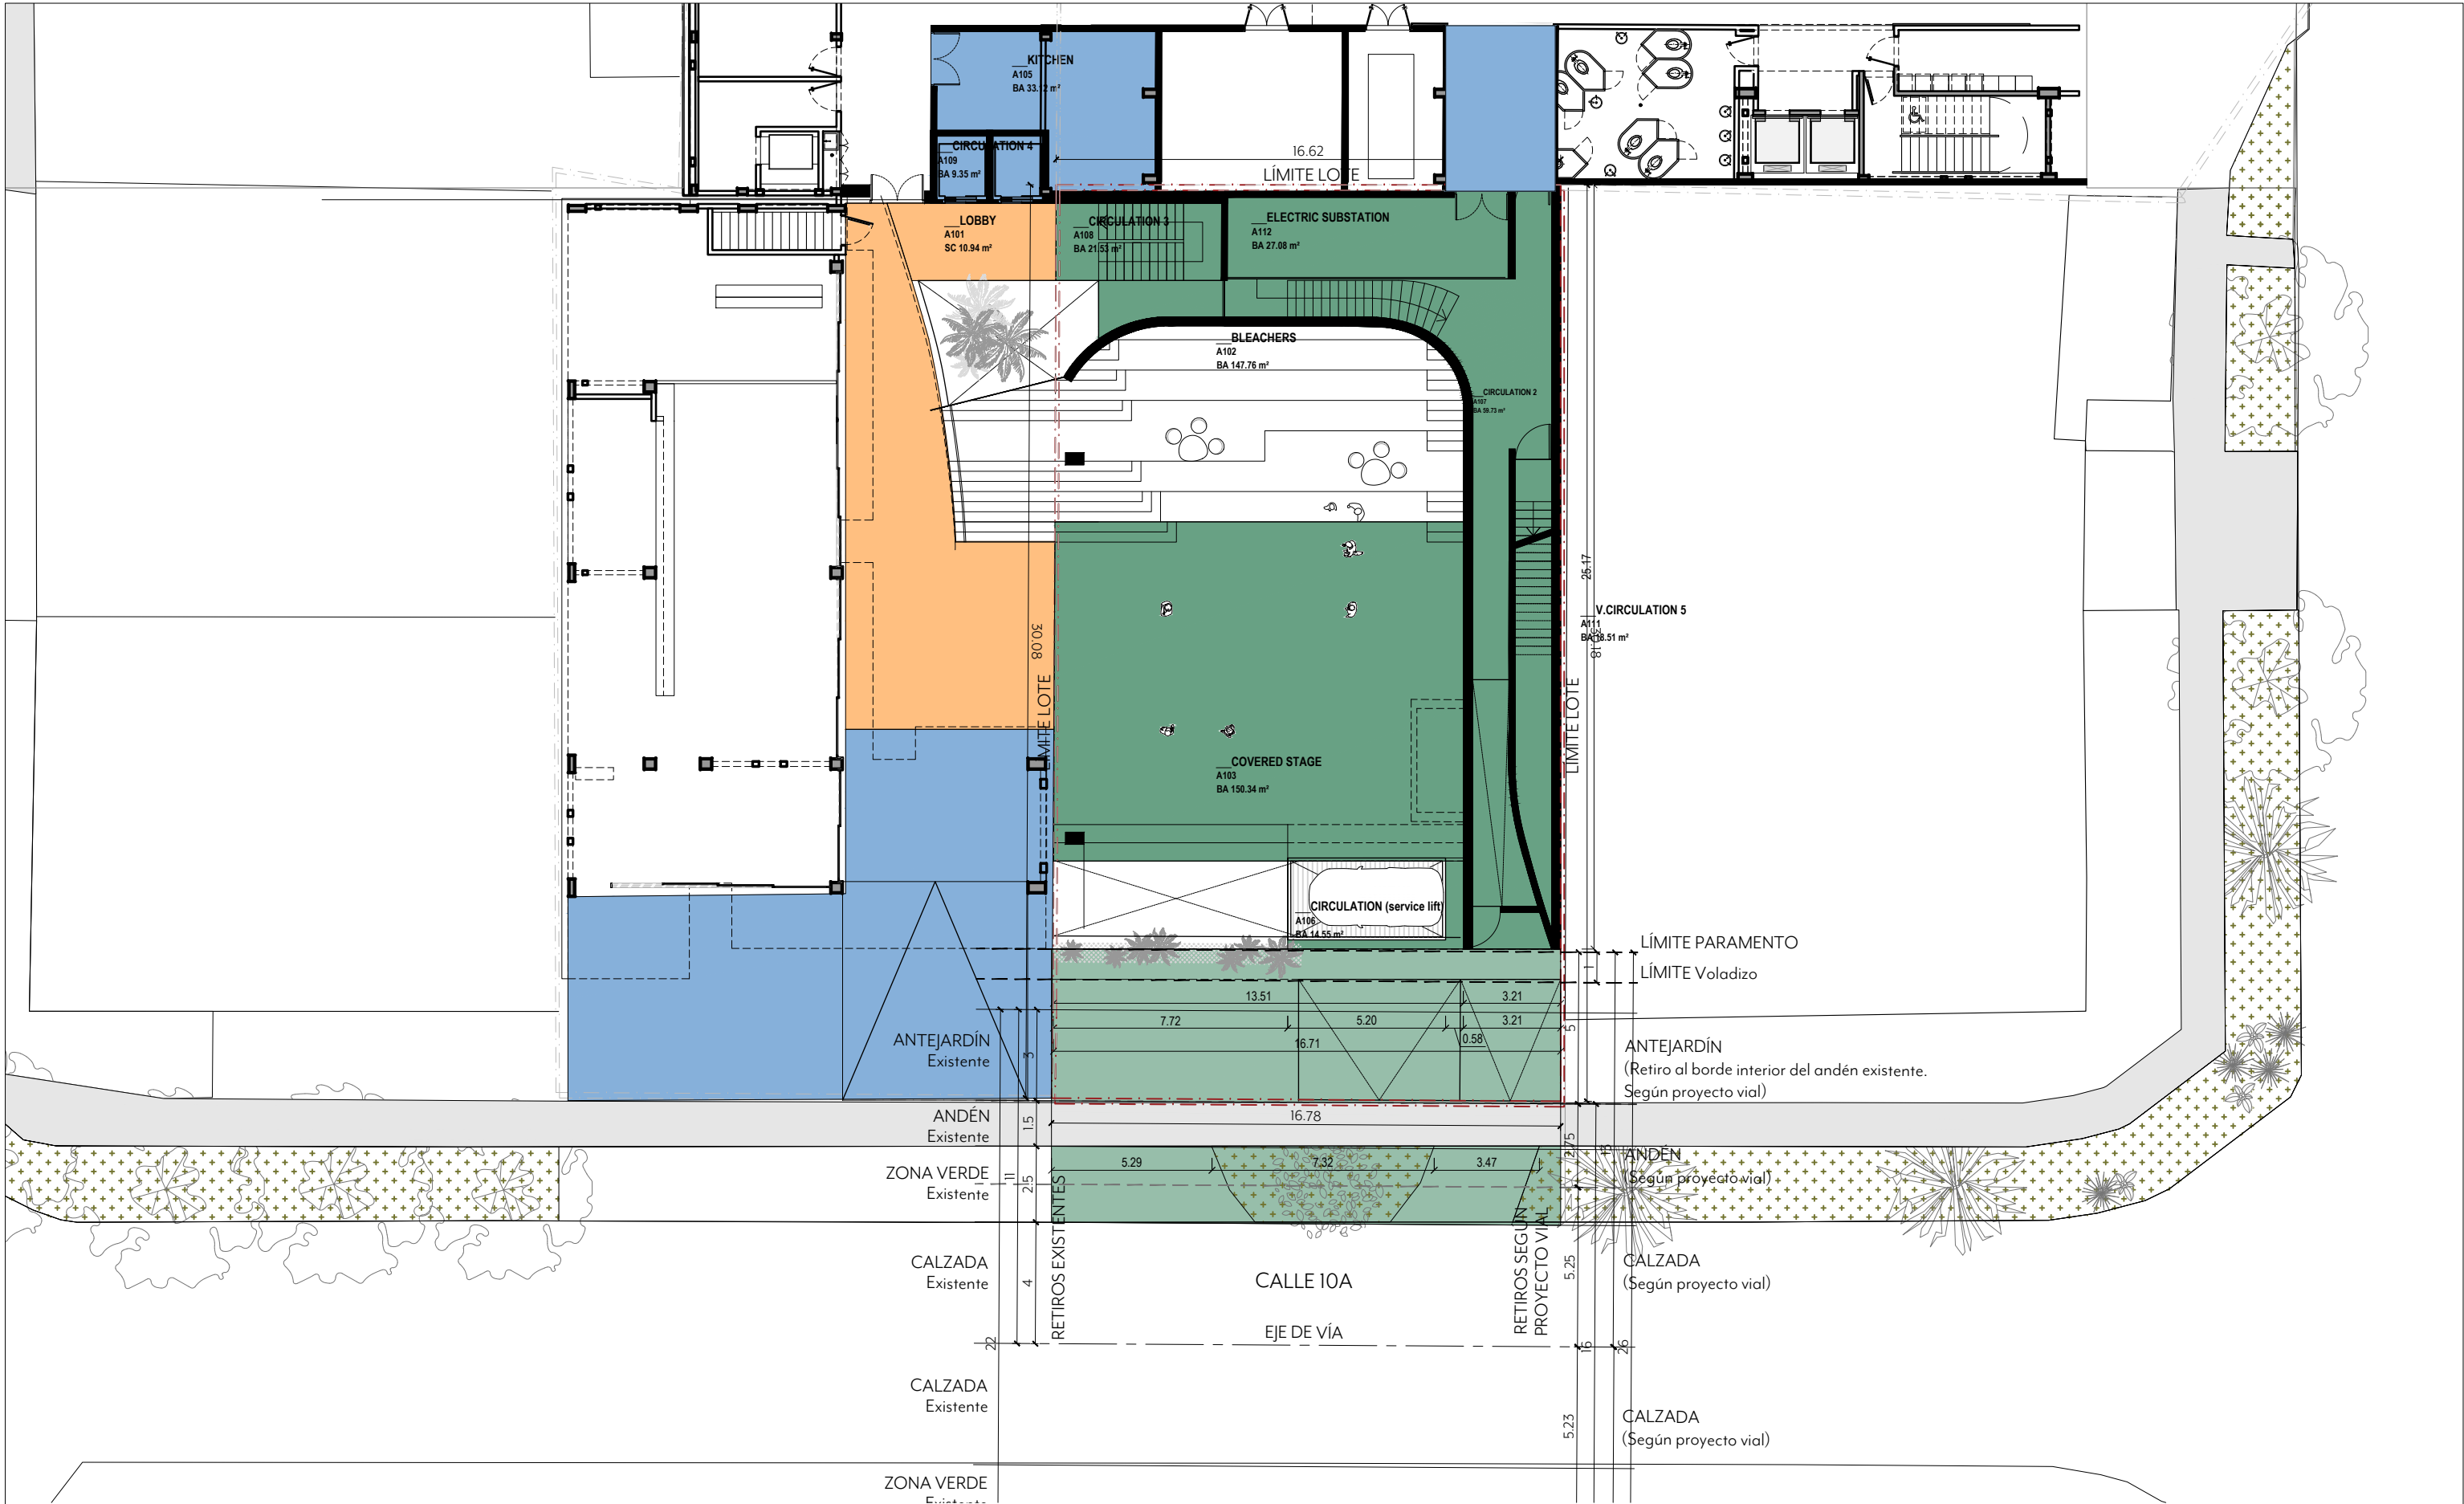

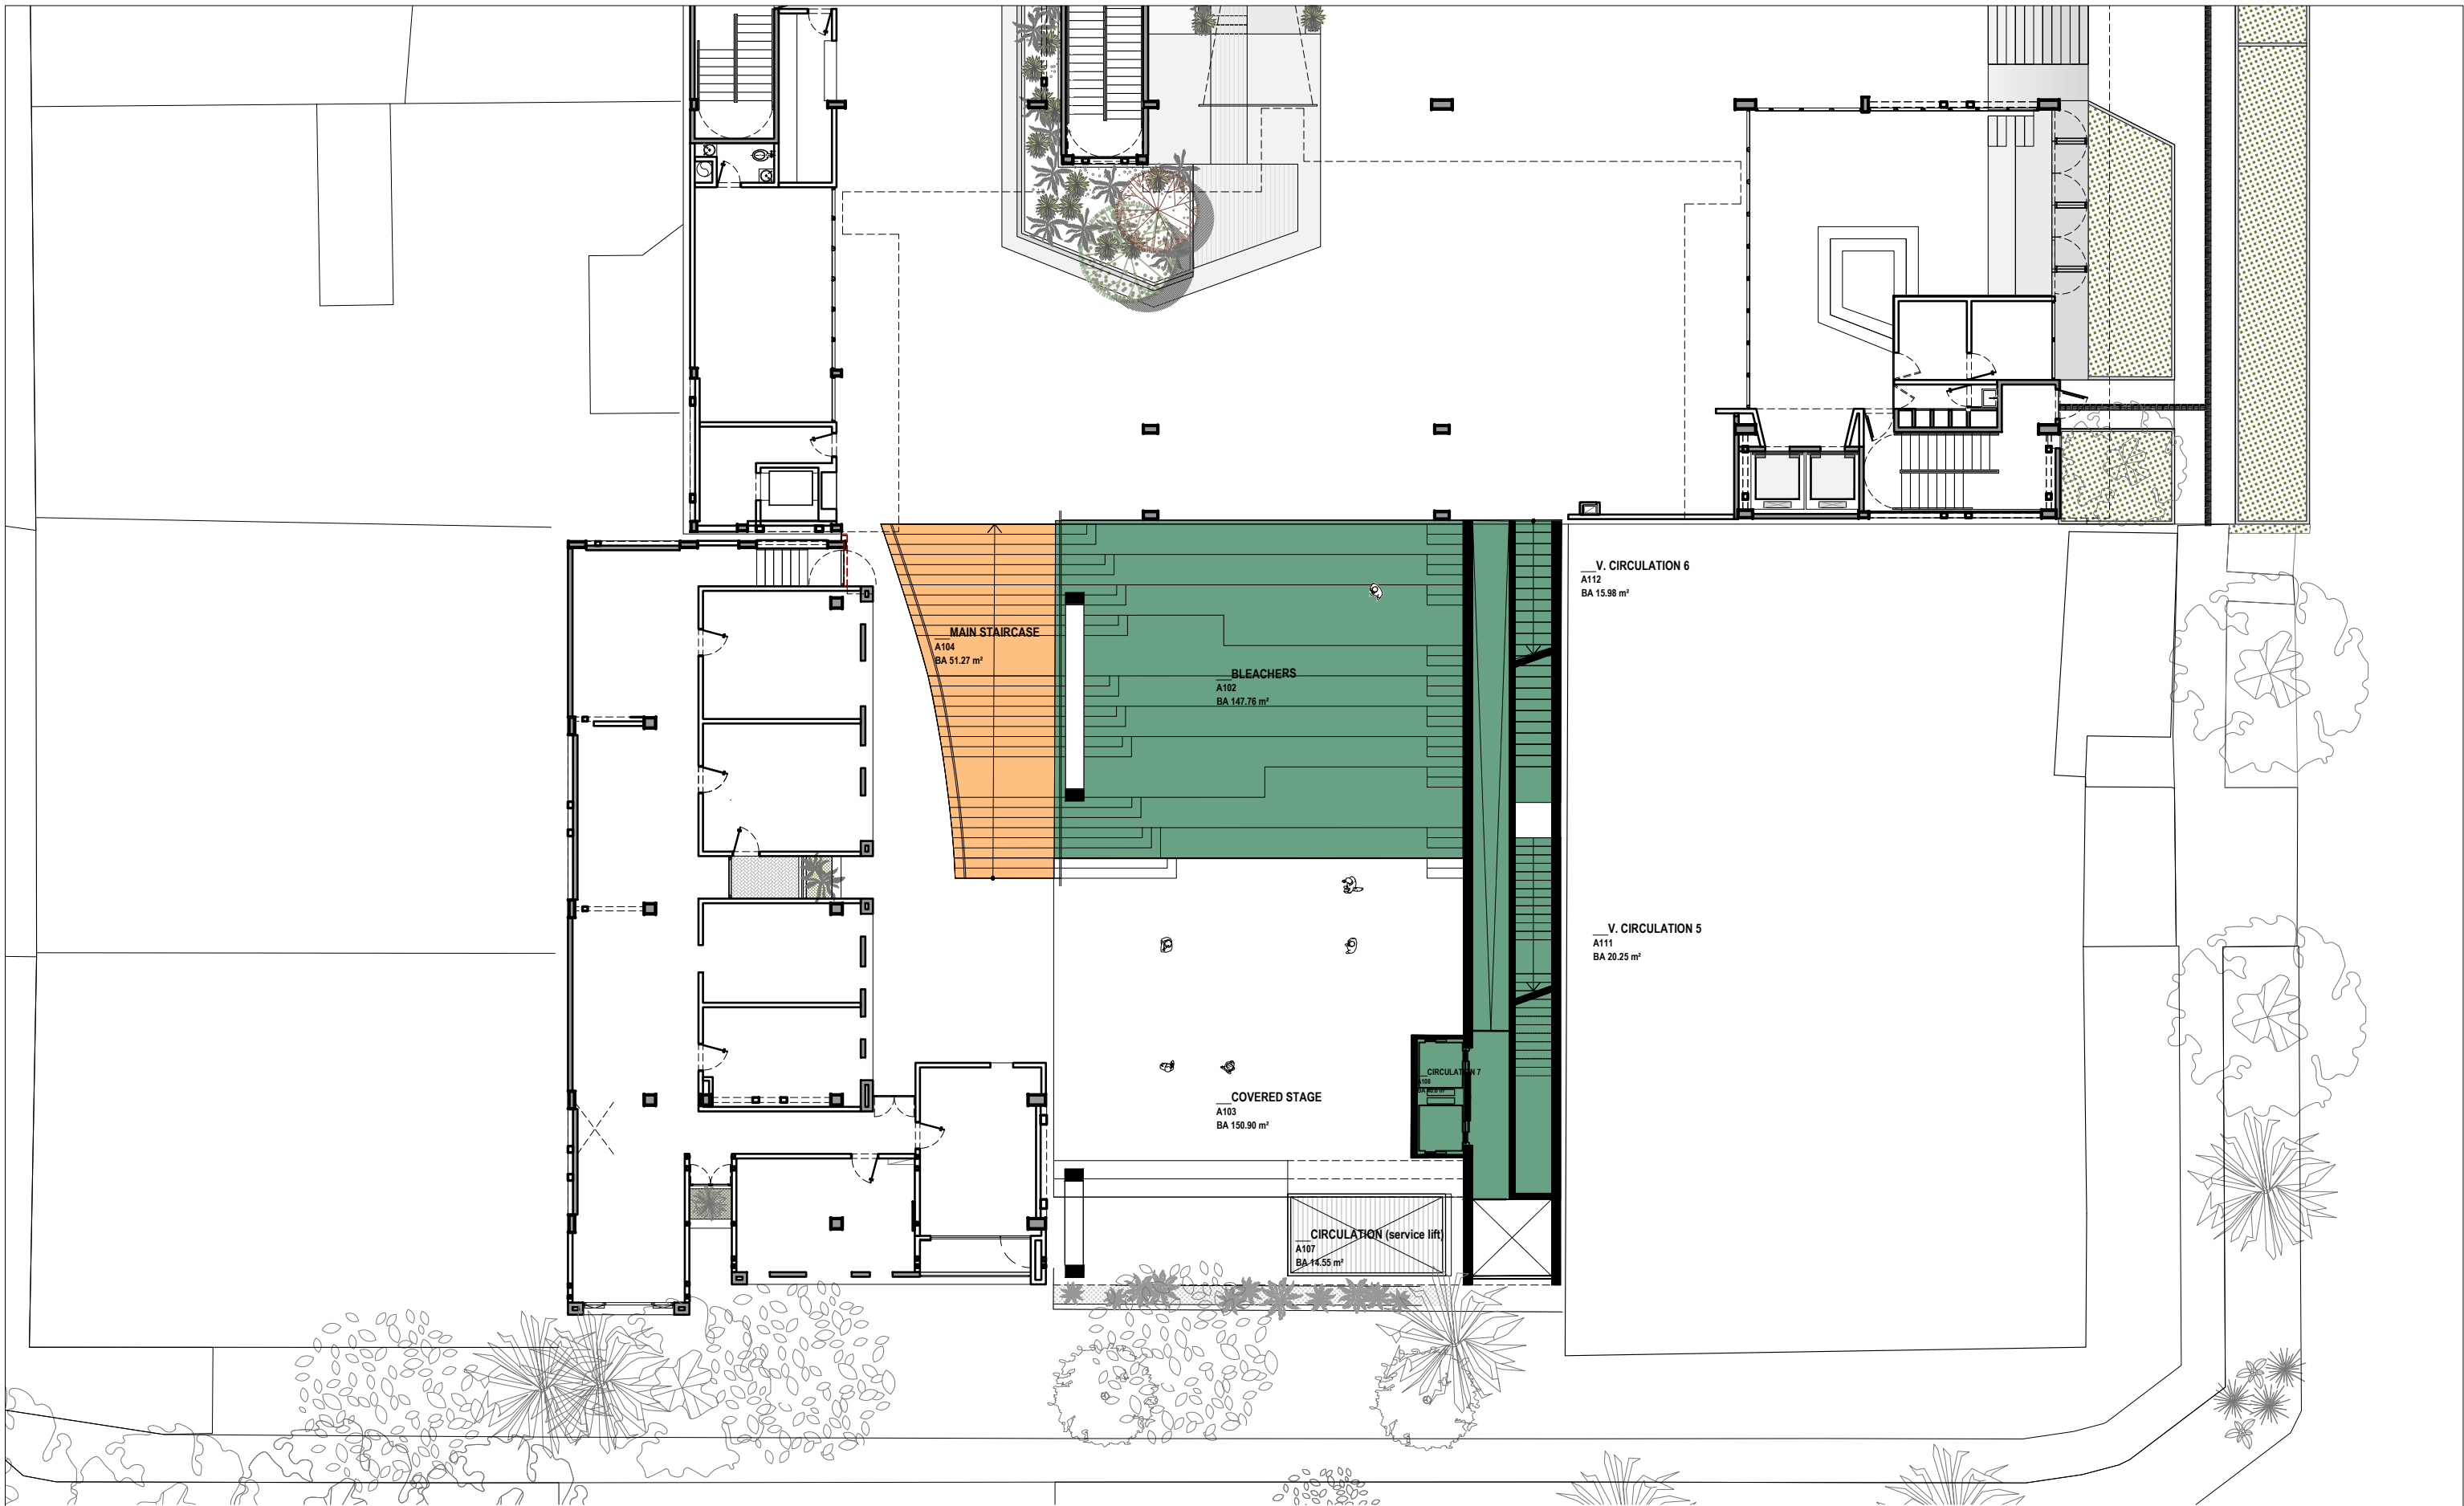

PROJECT

10A

Click Clack Medellín

PHASE

Phase 2

MA

KENGO KUMA & ASSOCIATES

104, rue Oberkampf 75 011 Paris
2-24-8 Minato-ku Minamioyama 107-0062 Tokyo

DRAWING TITLE

Level 1 Parque

SHEET NO

001

SCALE


1/200


DATE

DEC 2025

INDICE

0

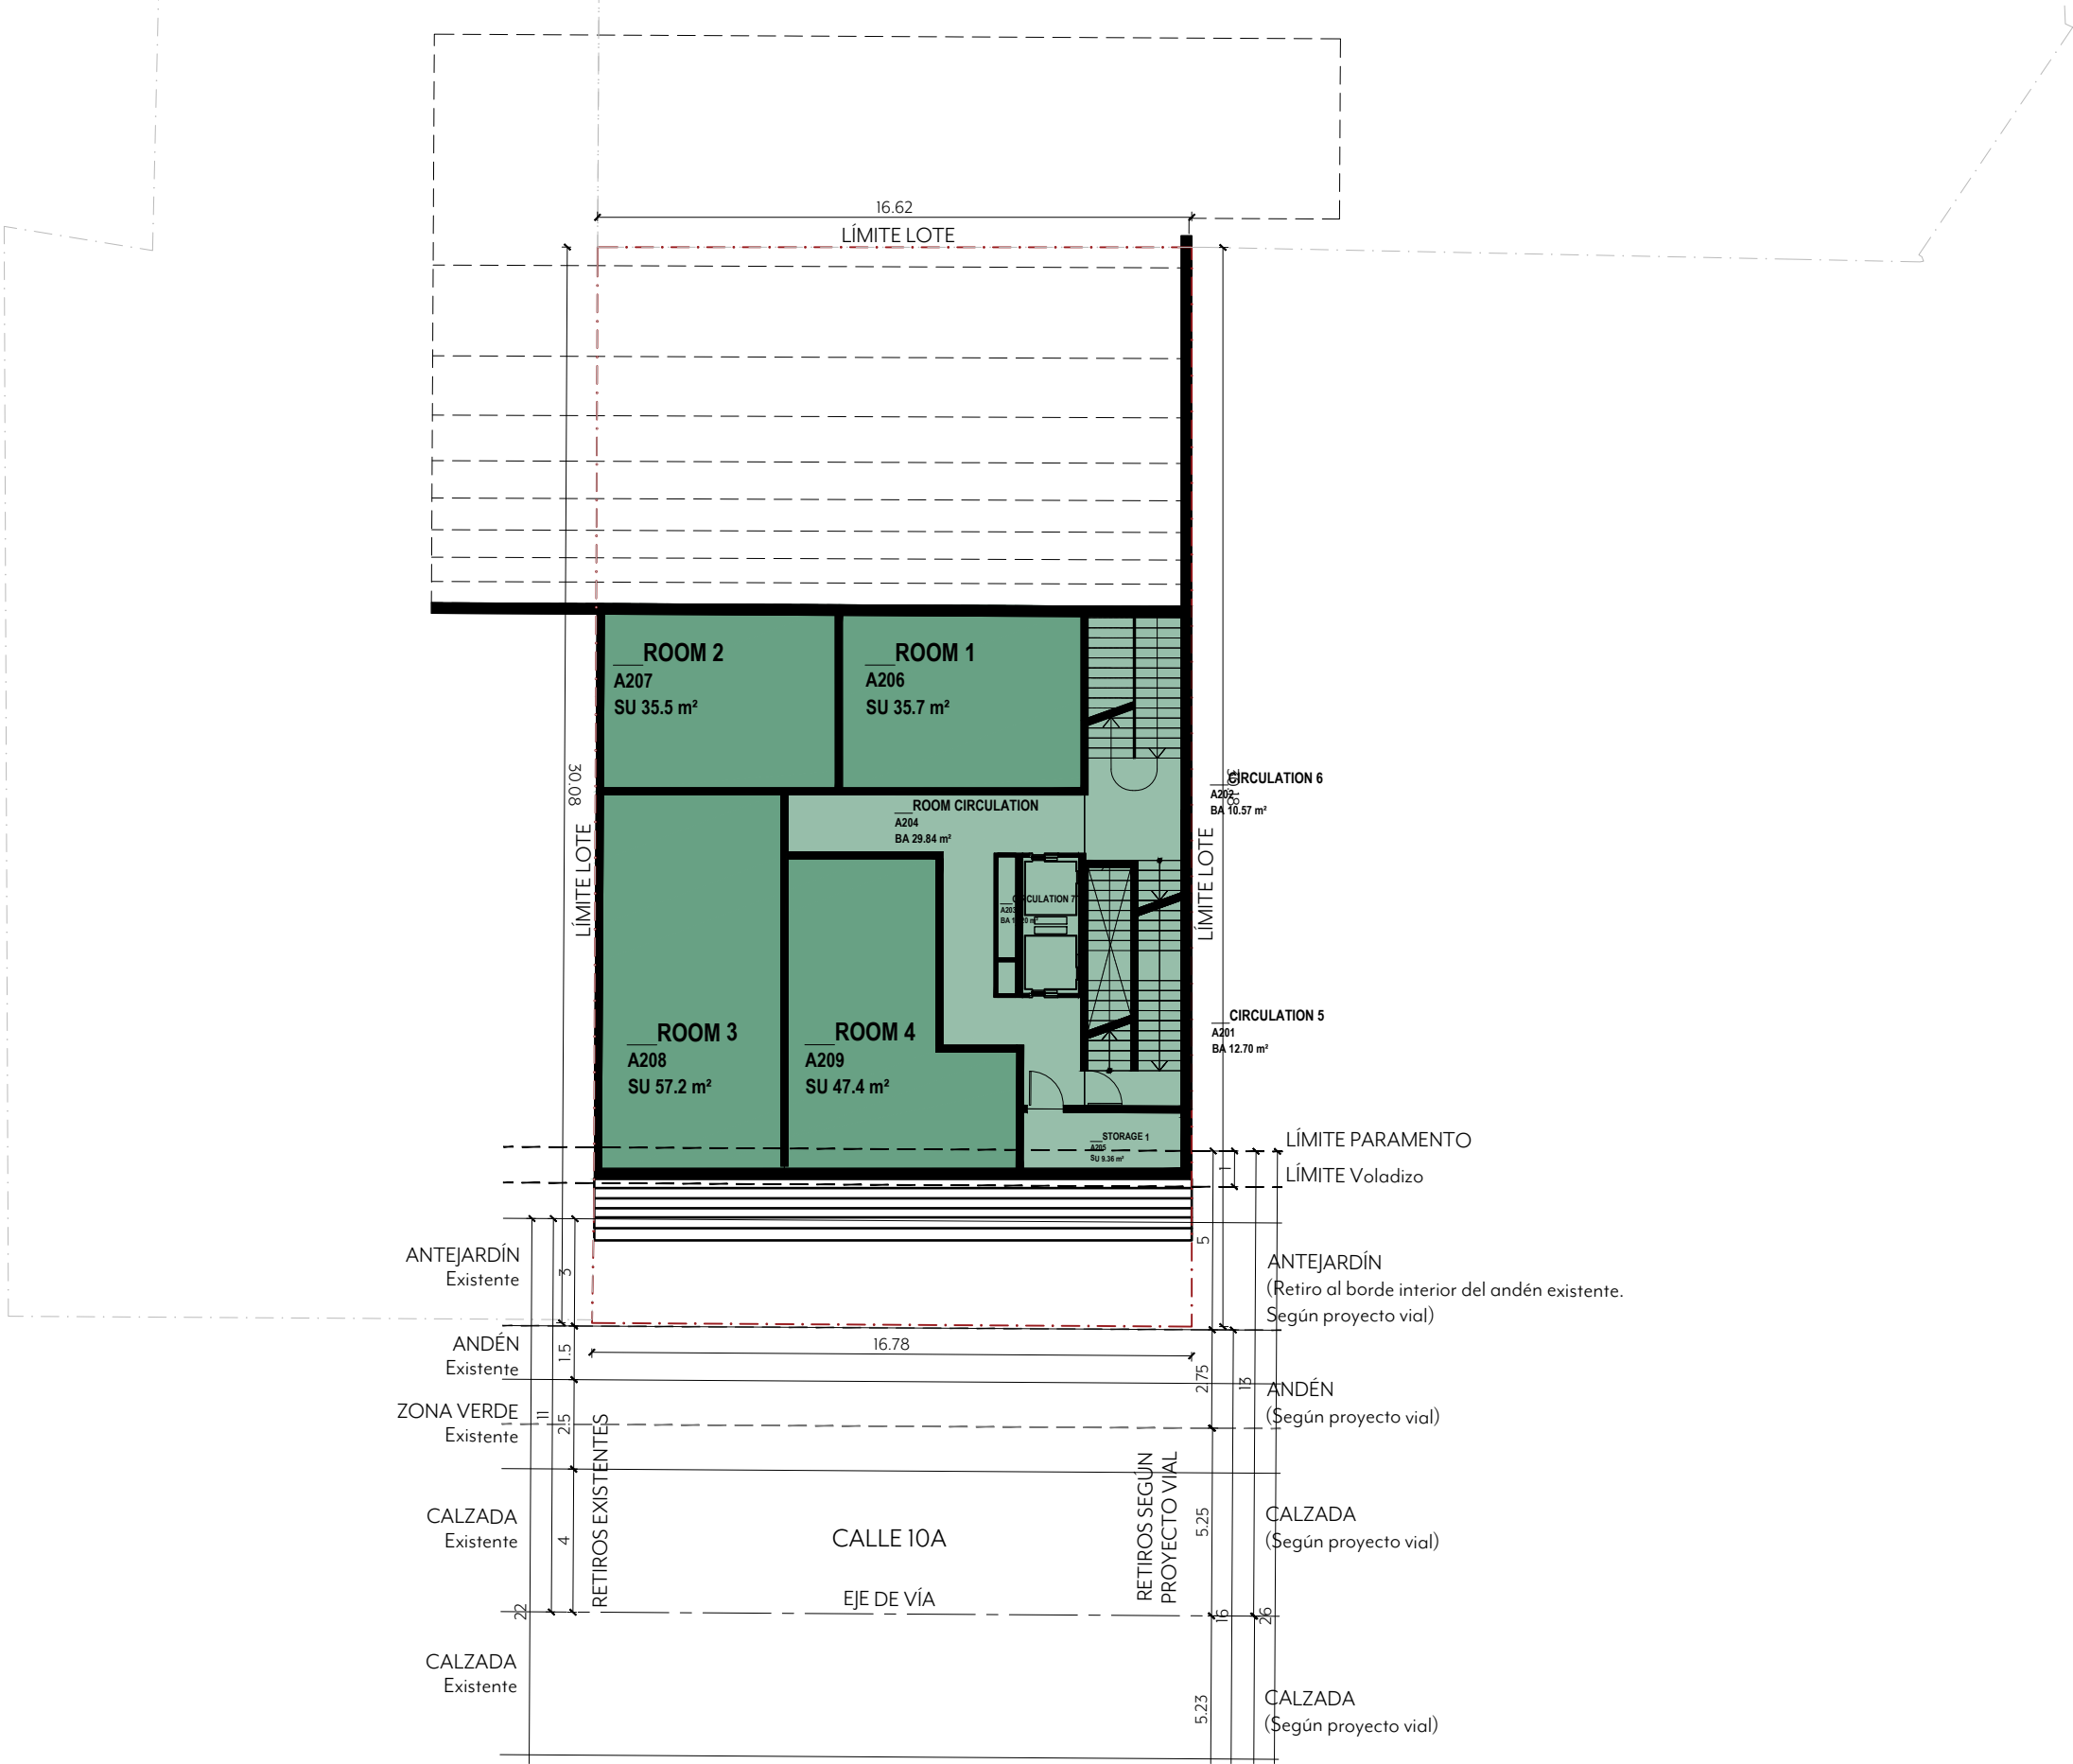

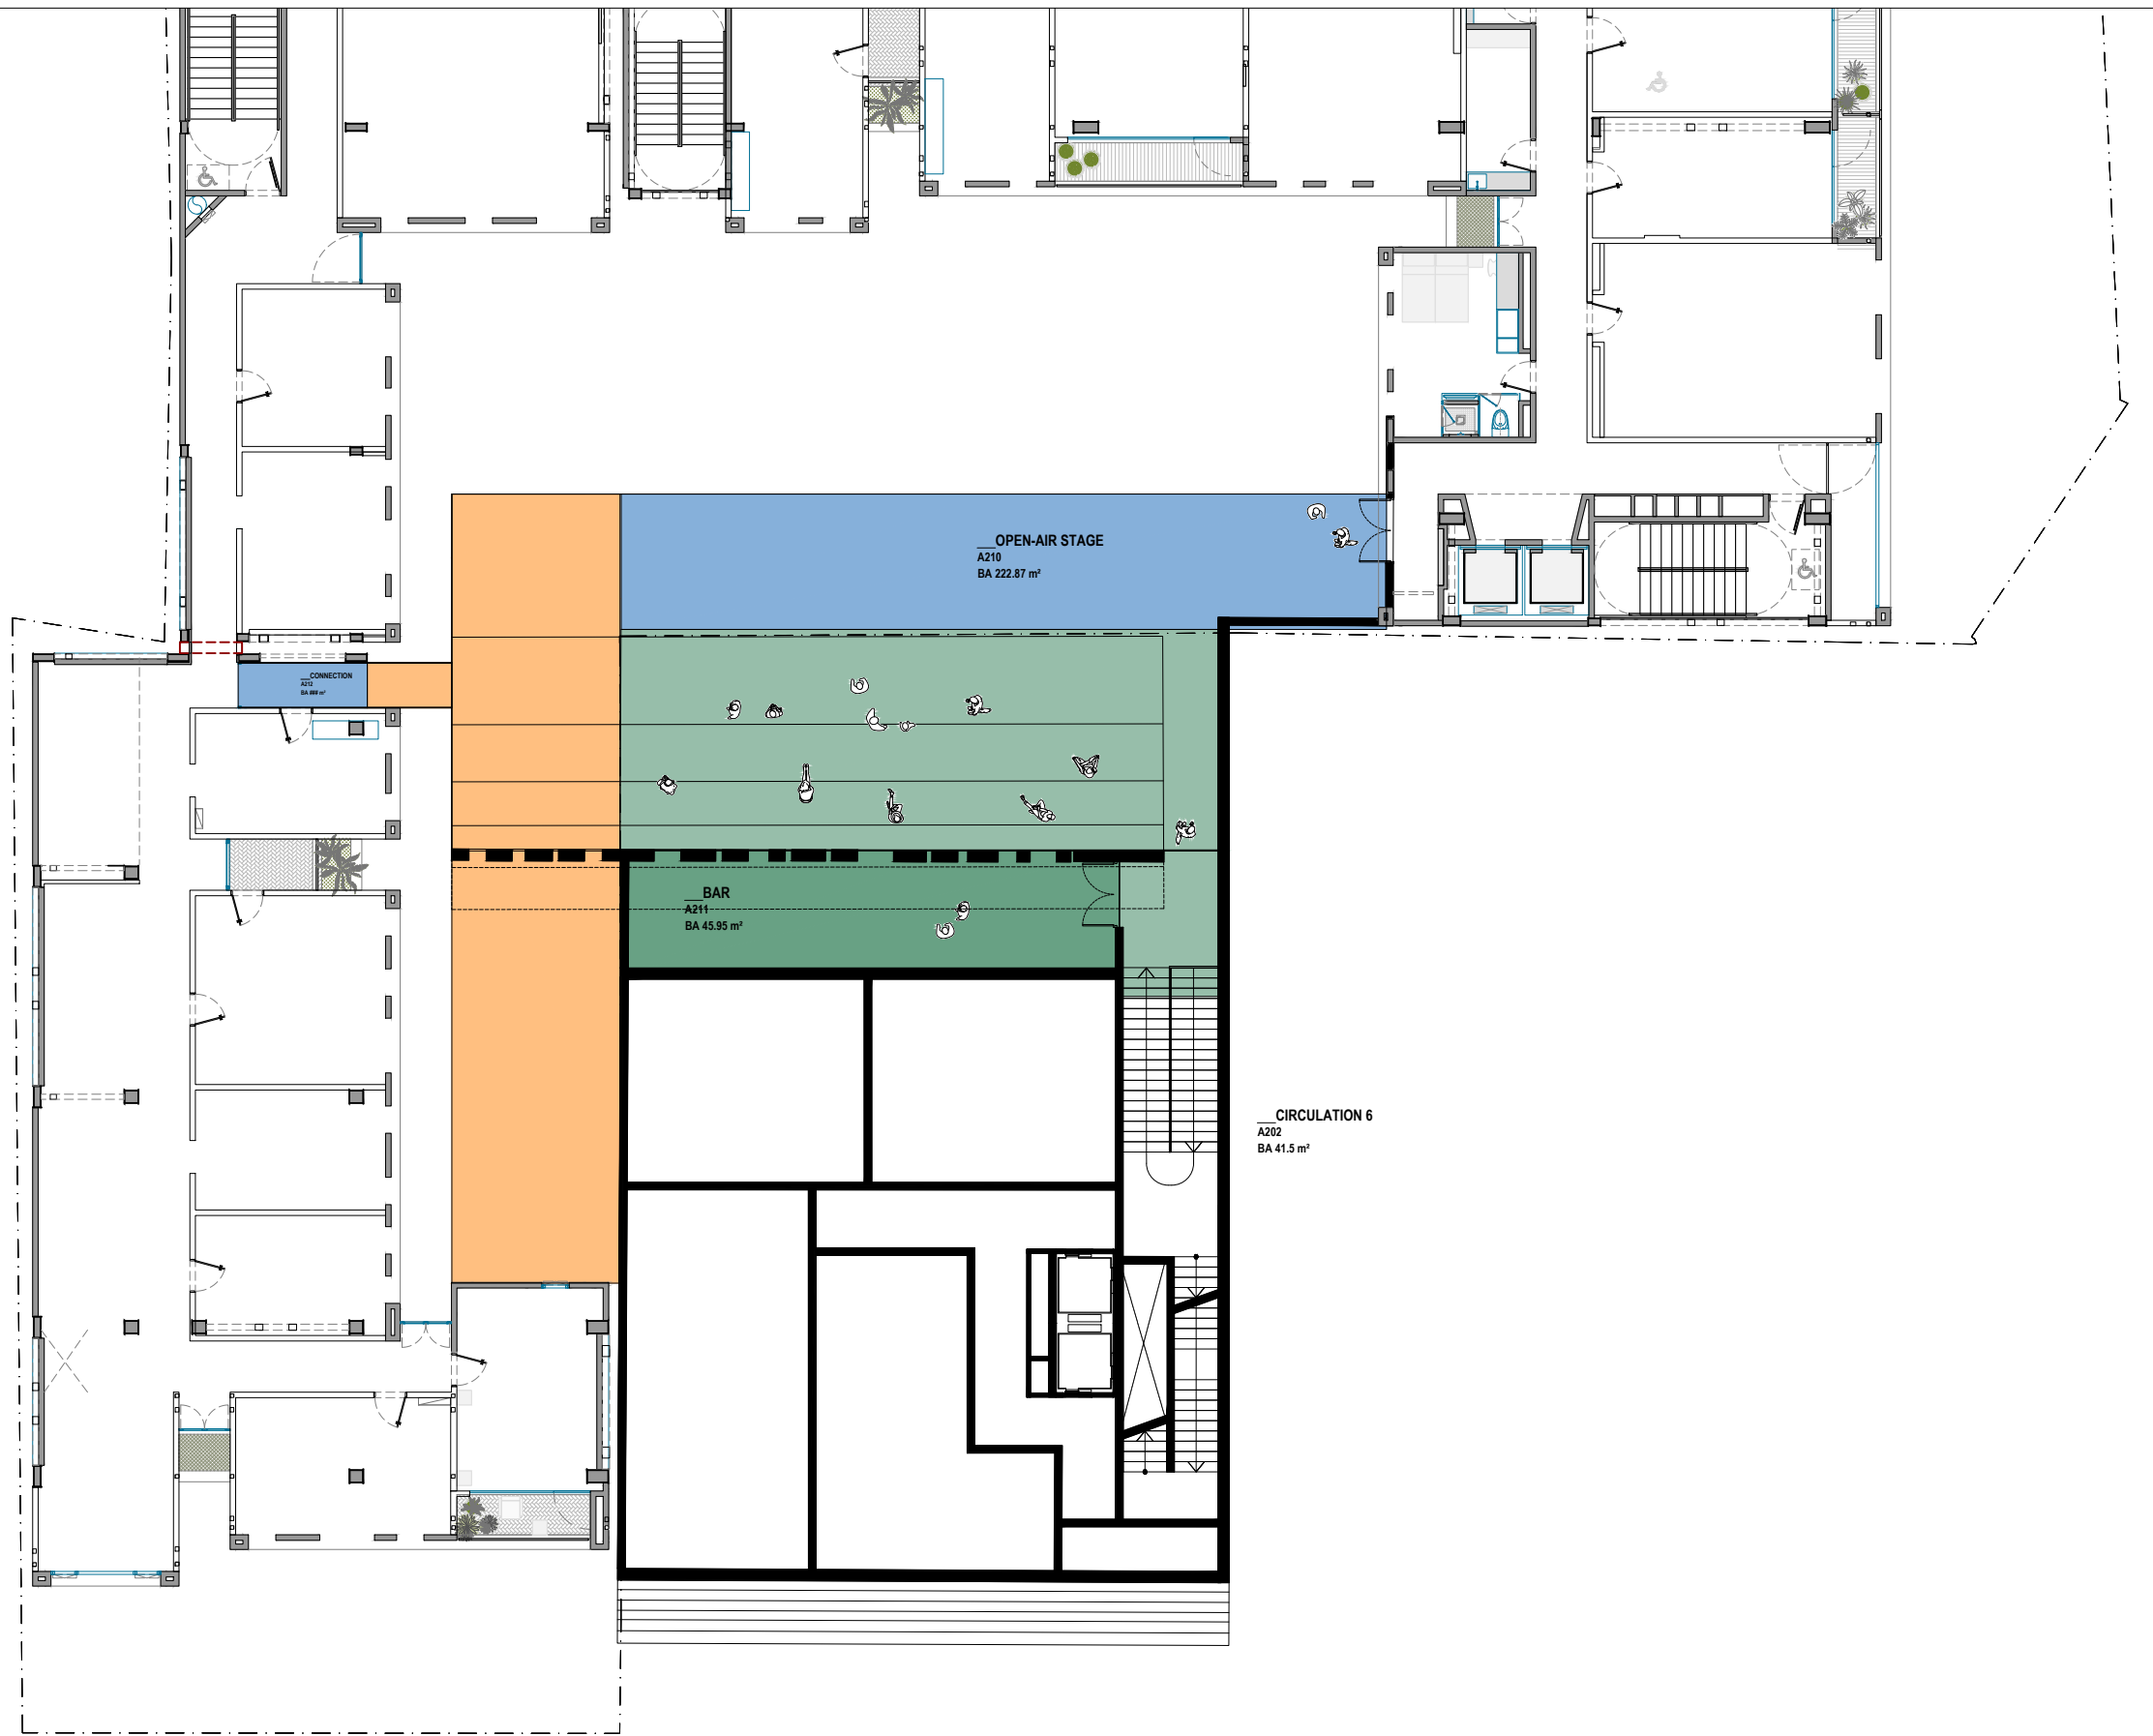

PROJECT

10A

Click Clack Medellín

PHASE

Phase 2

MA

KENGO KUMA & ASSOCIATES

104, rue Oberkampf 75 011 Paris
2-24-8 Minato-ku Minamioyama 107-0062 Tokyo

DRAWING TITLE

Level 2 Open-Air Stage

SHEET NO

001

SCALE


1/200


DATE


DEC 2025


INDICE


0

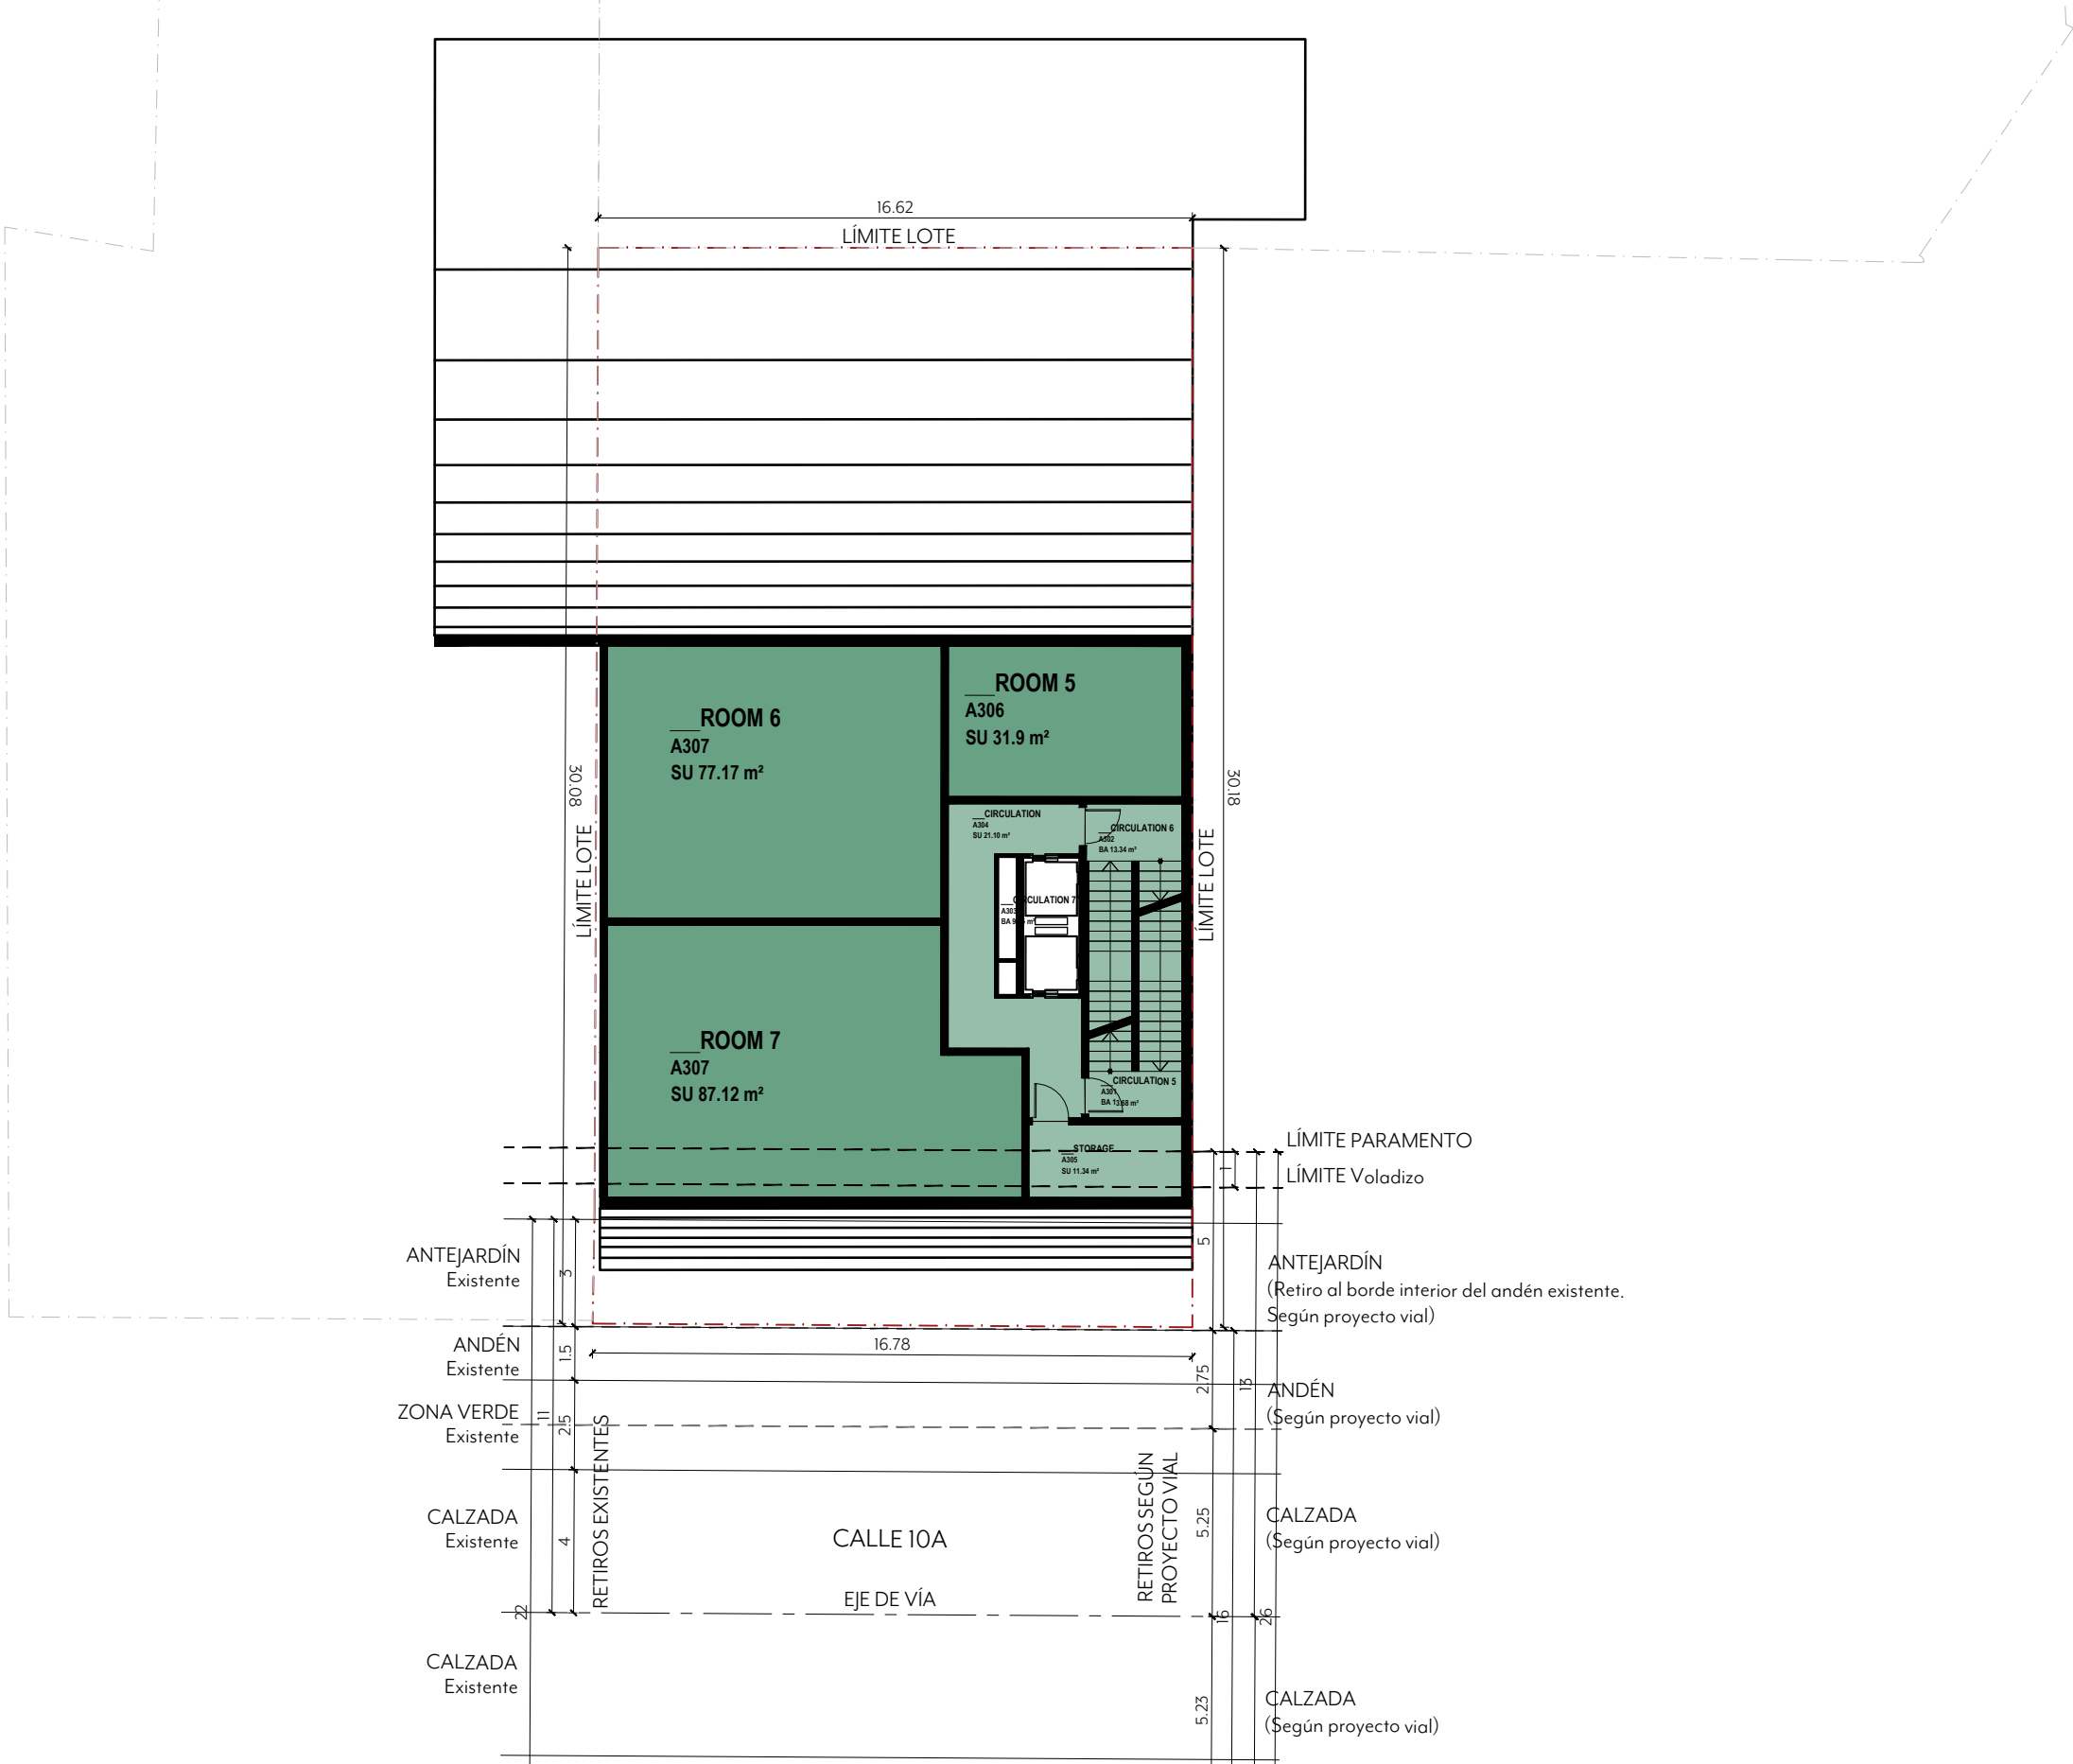

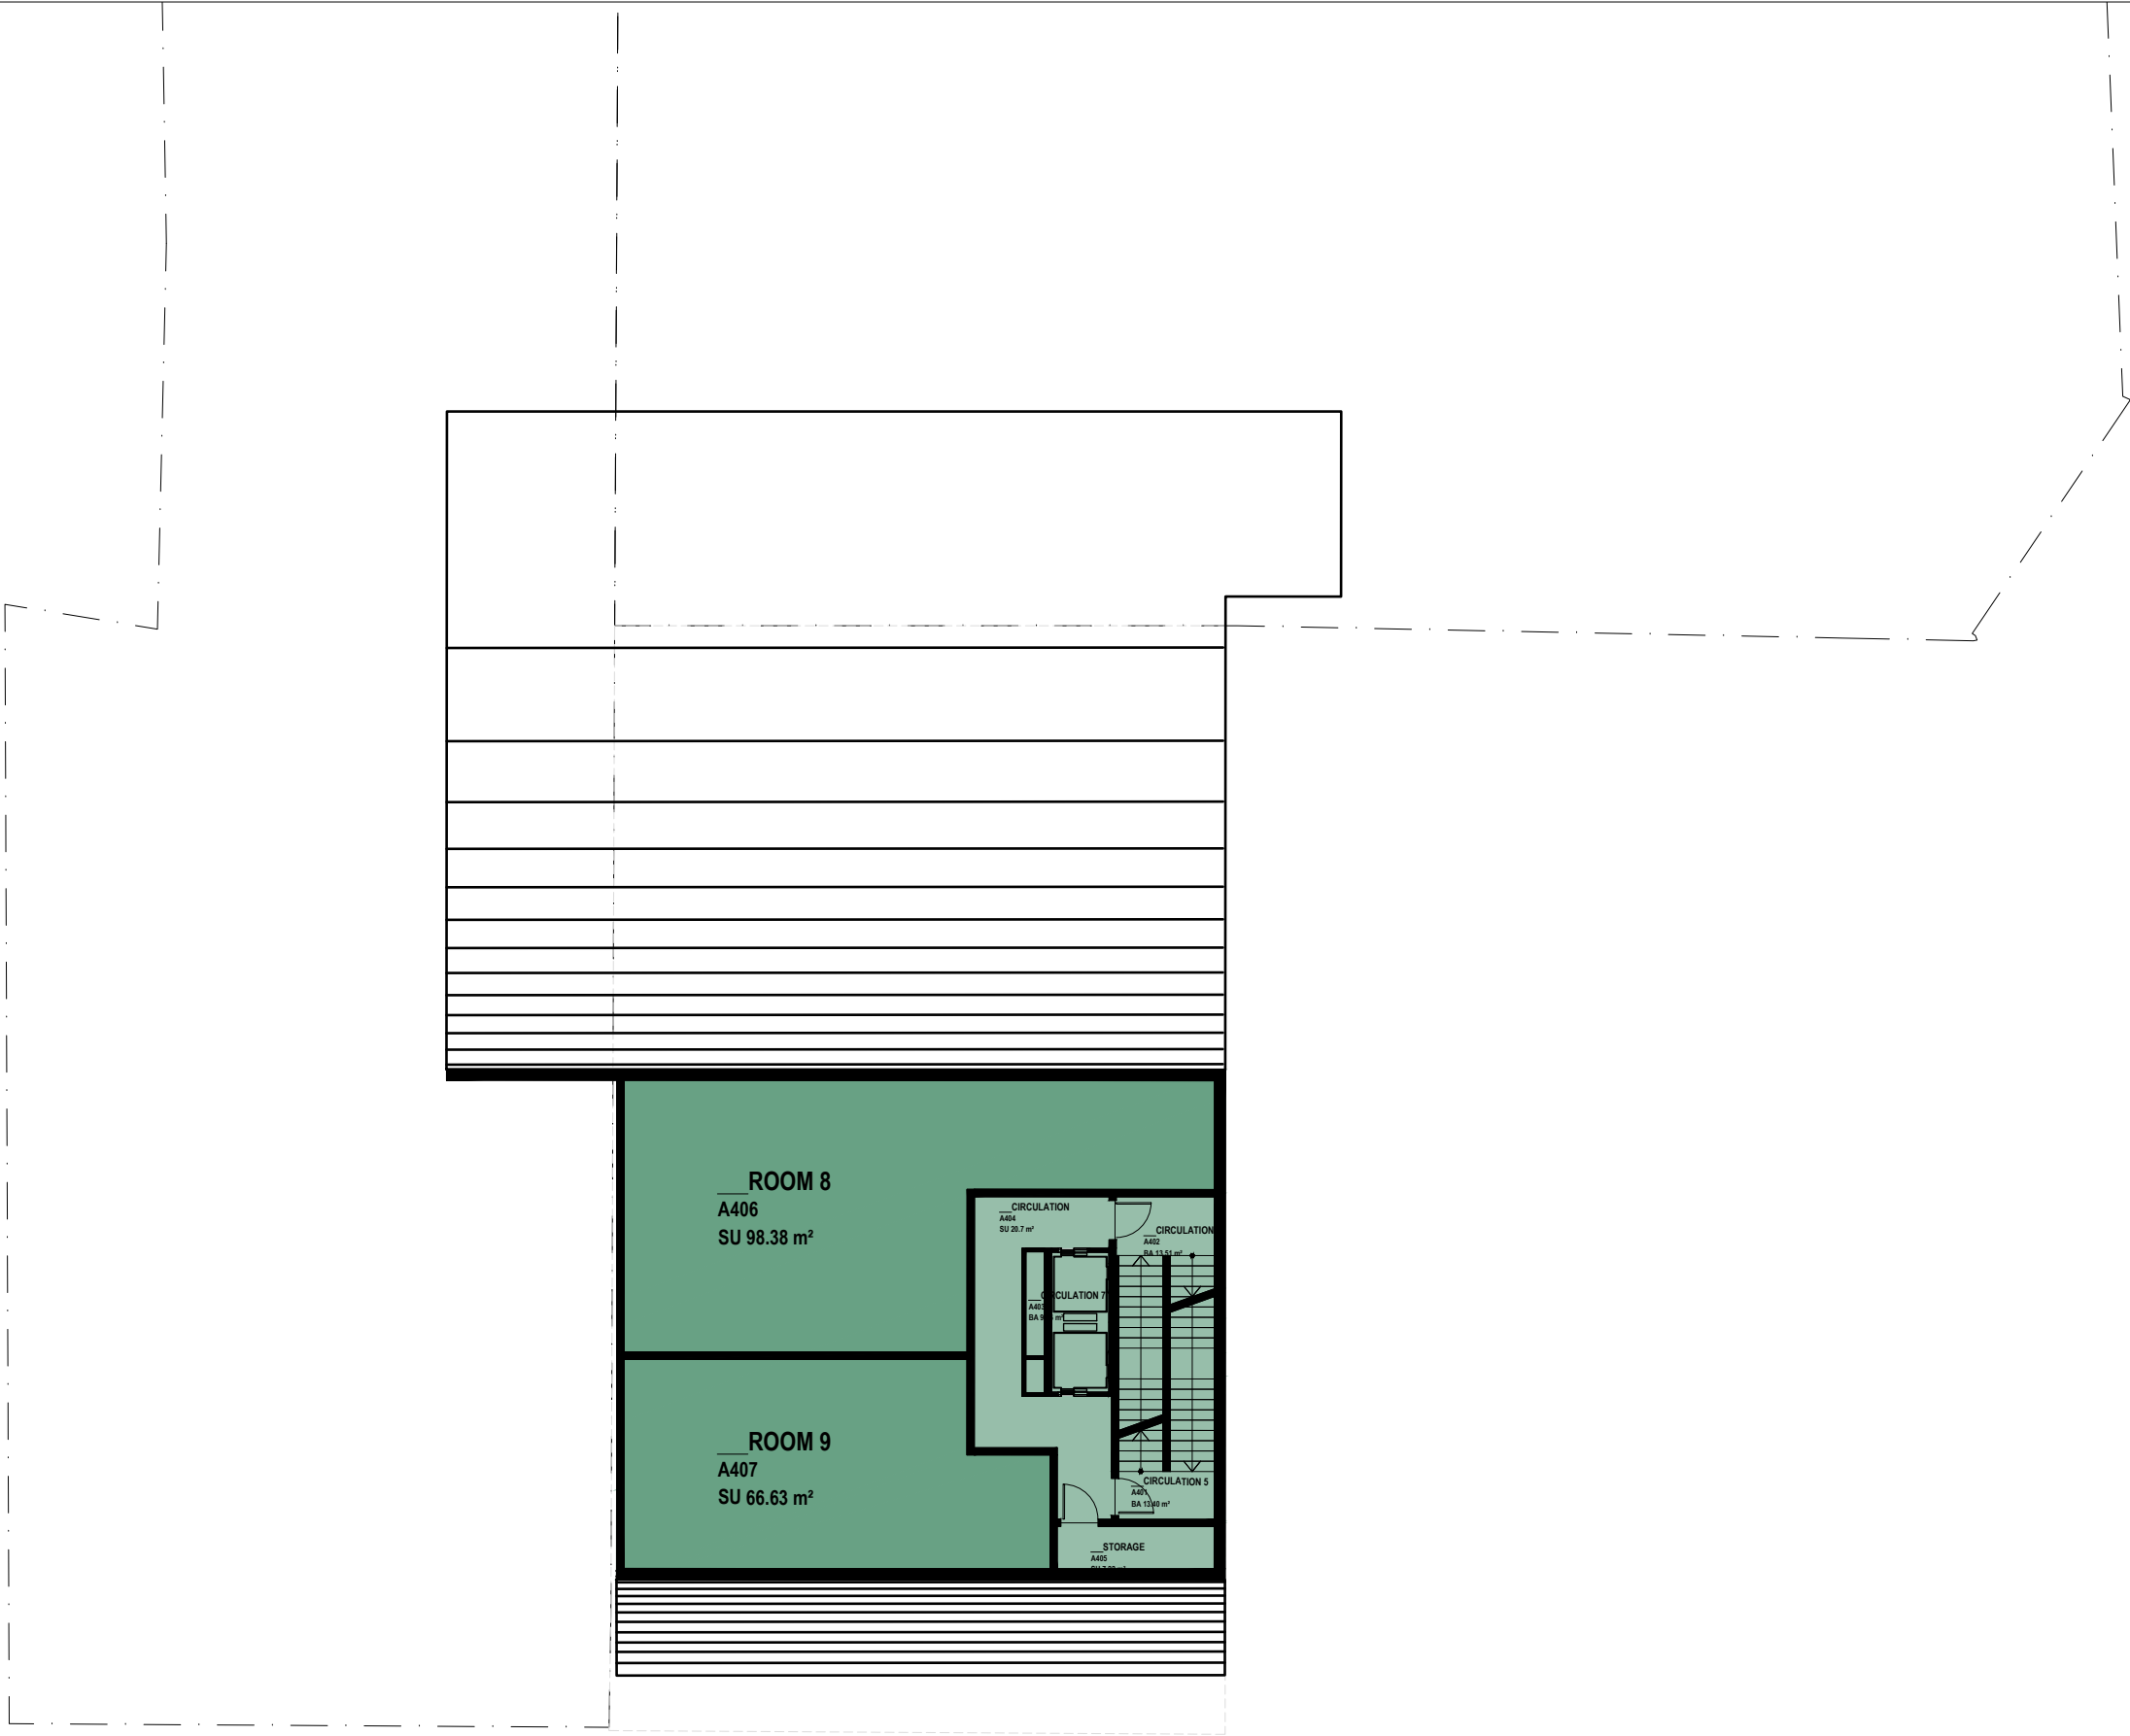

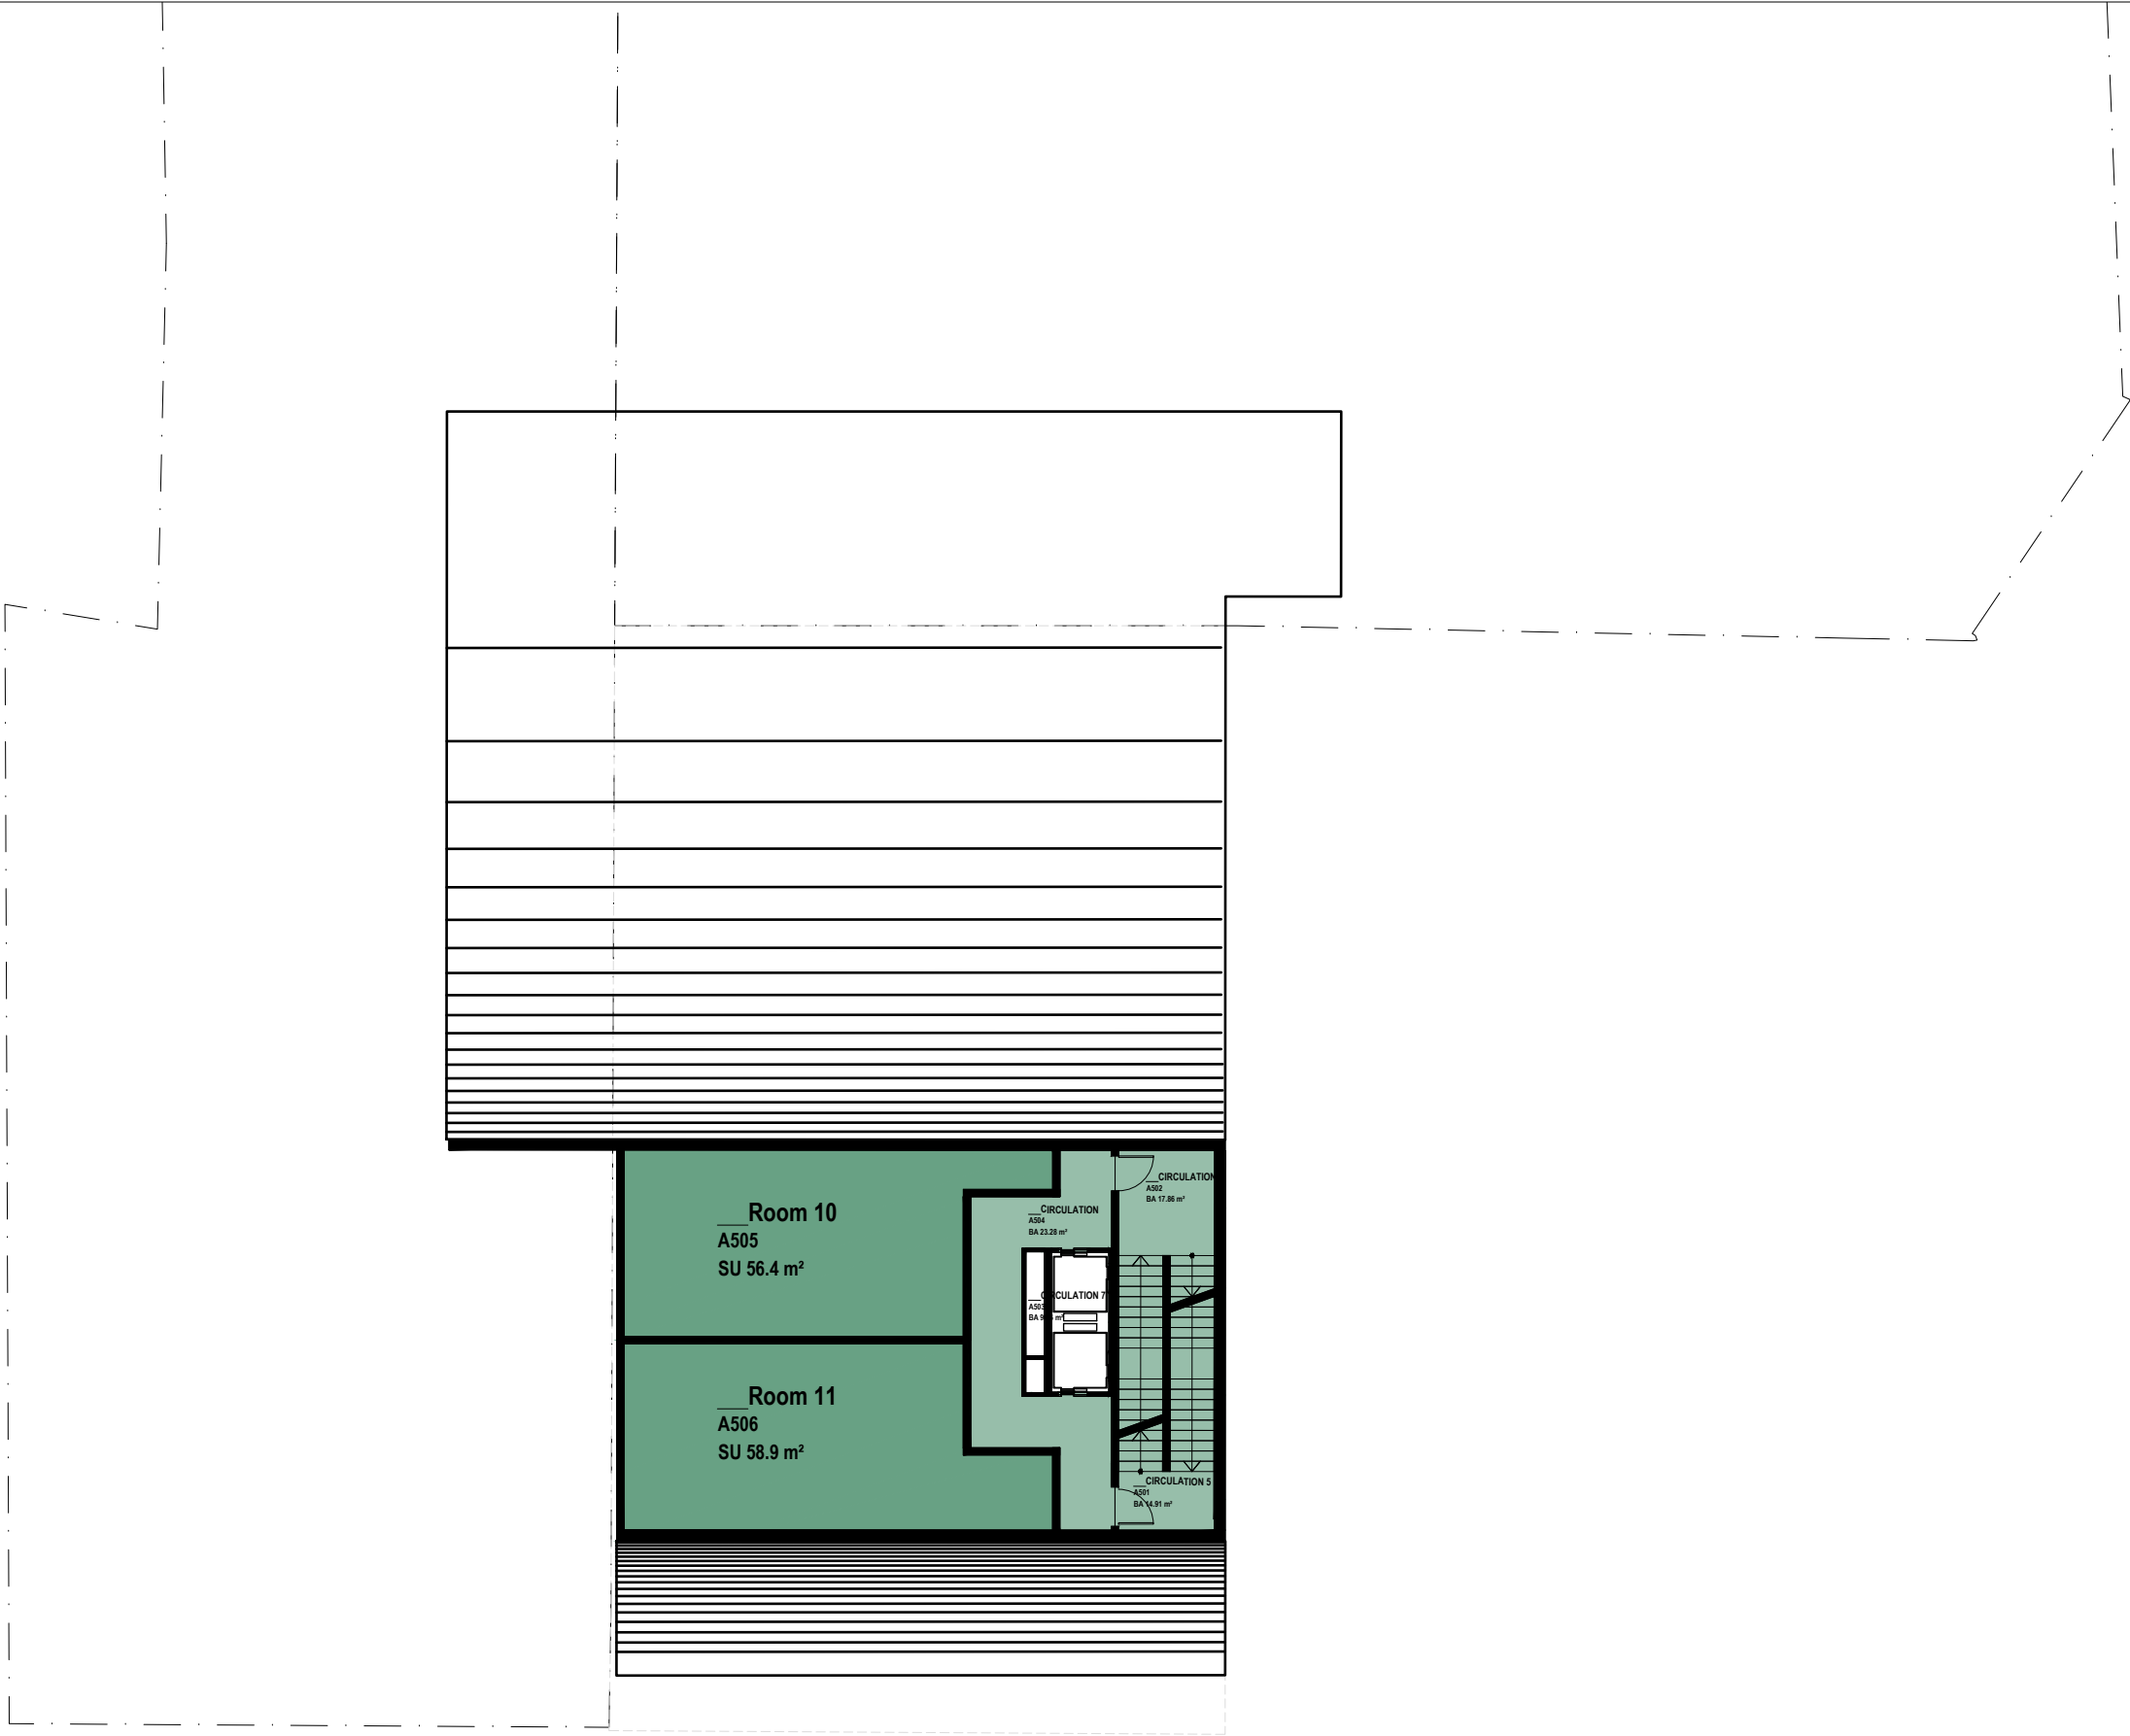

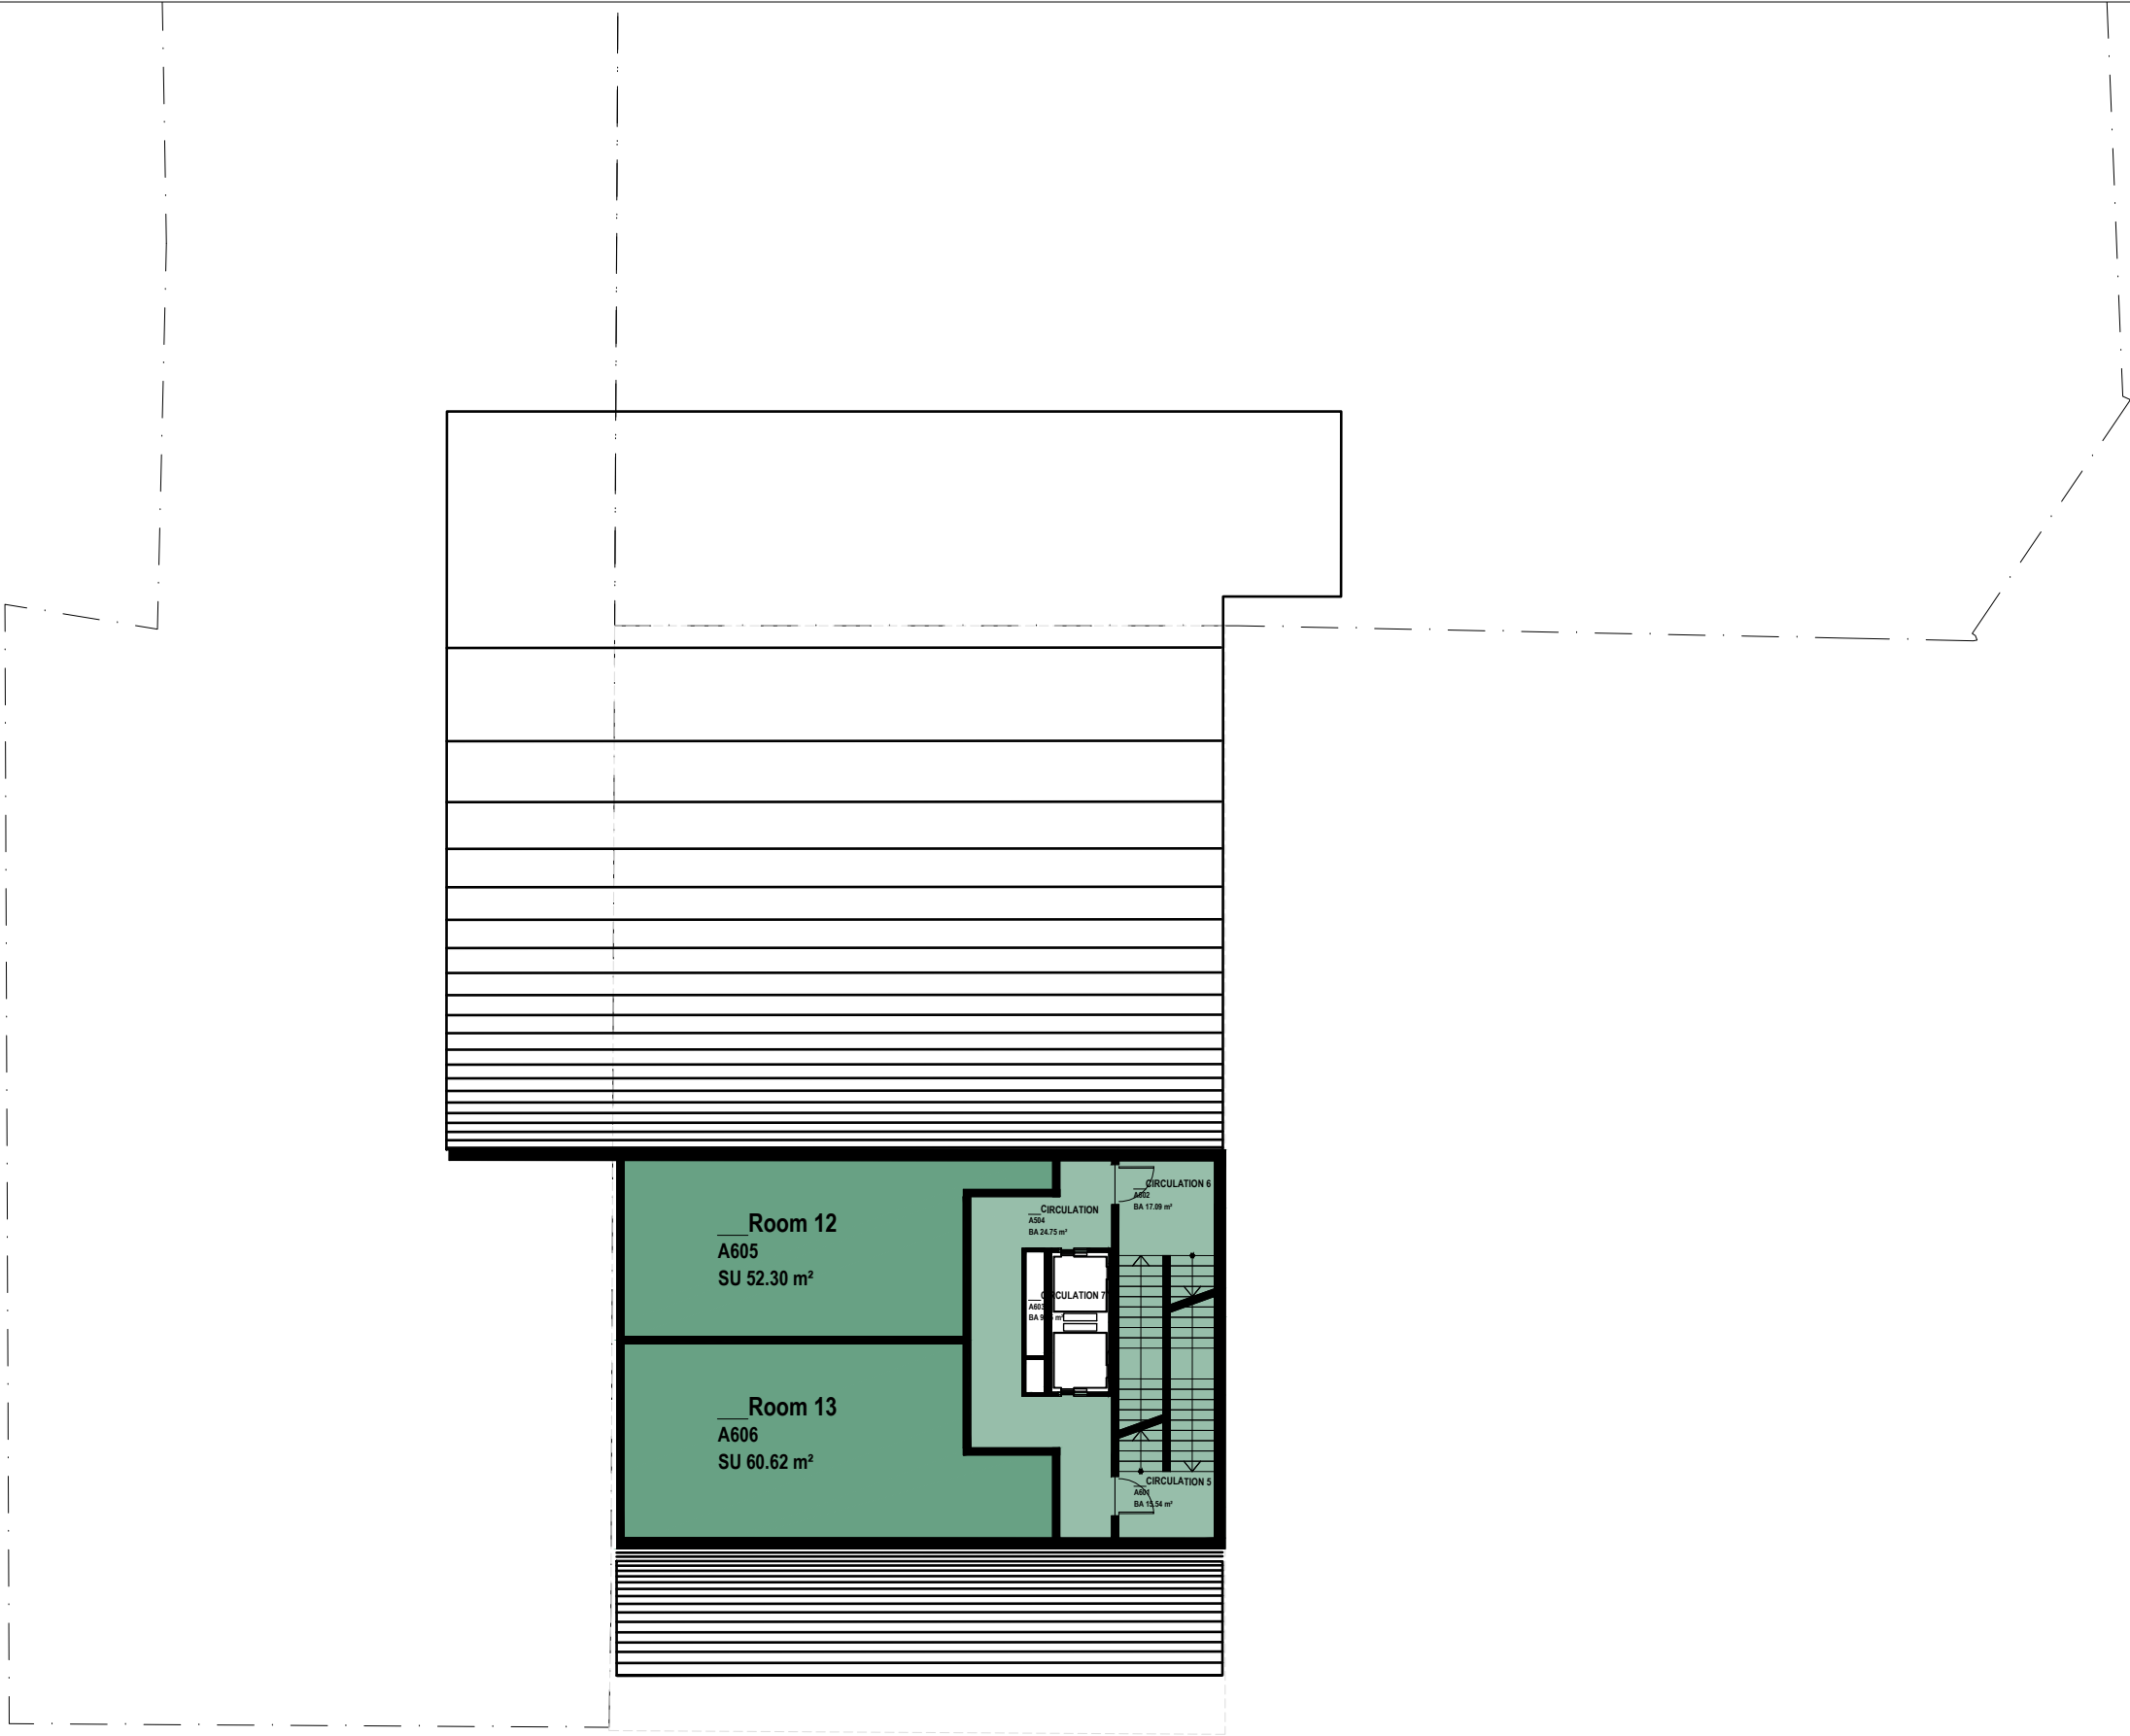

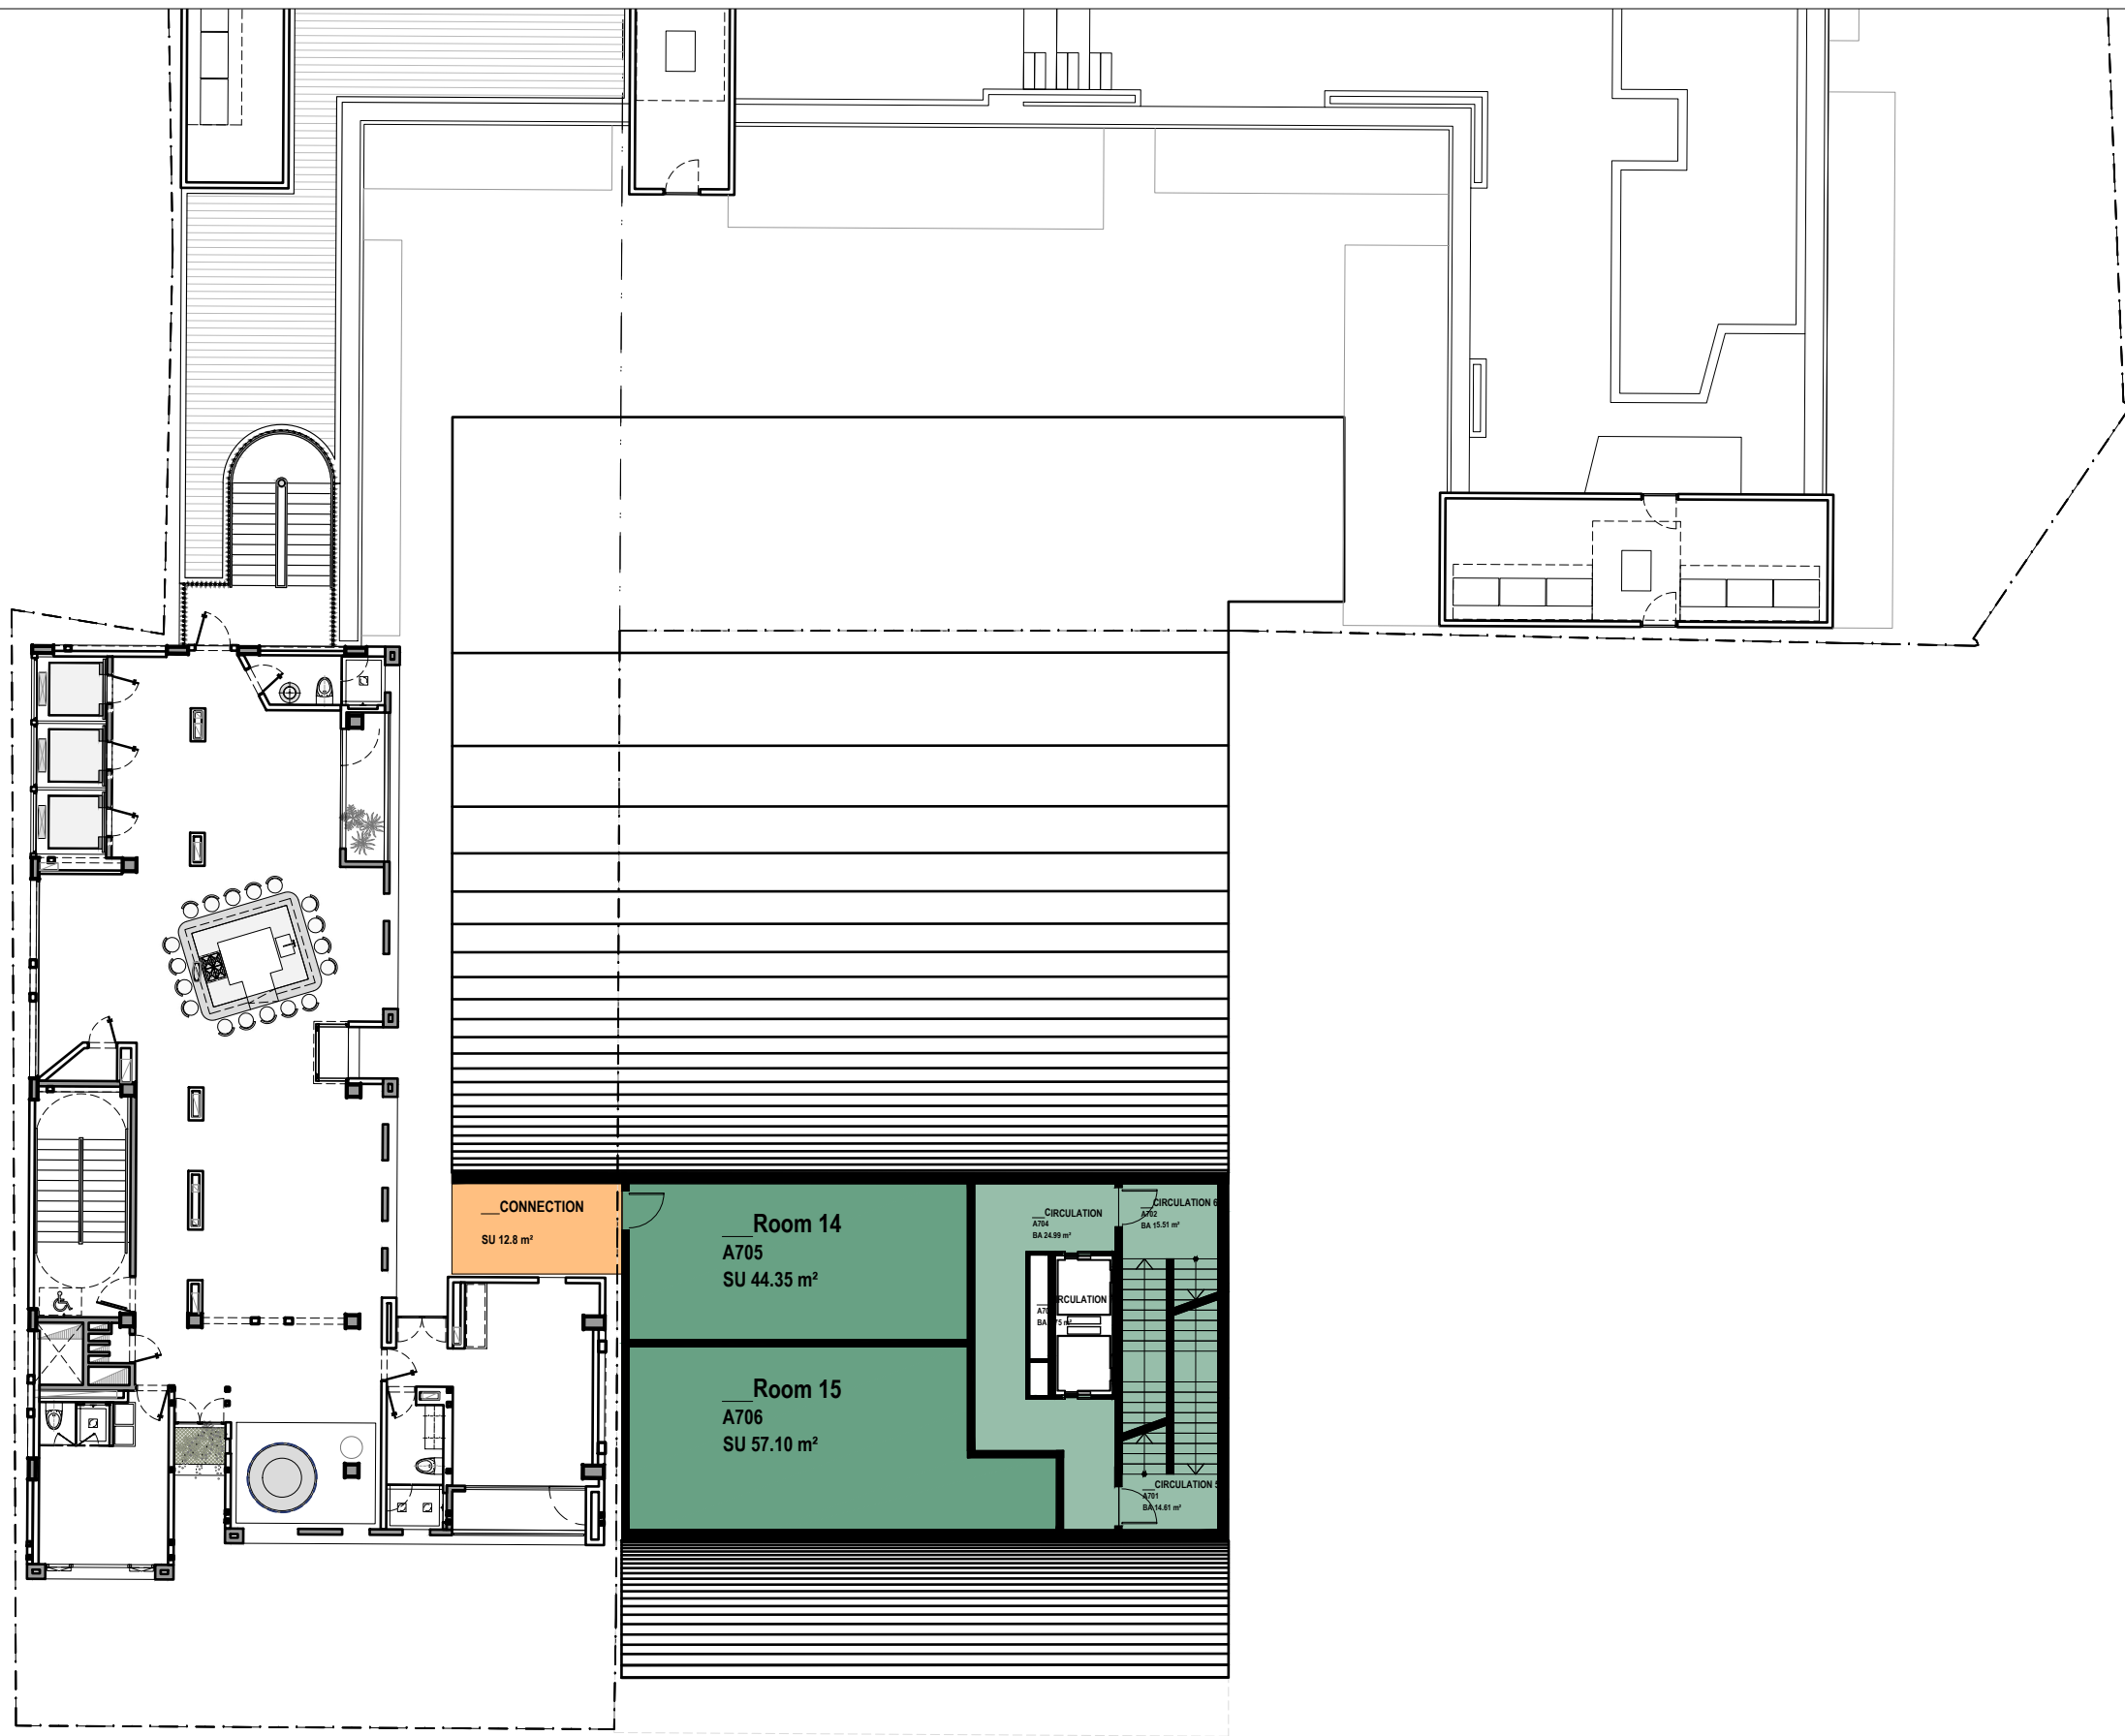

PROJECT

10A

Click Clack Medellín

PHASE

Phase 2

MA

KENGO KUMA & ASSOCIATES

104, rue Oberkampf 75 011 Paris
2-24-8 Minato-ku Minamioyama 107-0062 Tokyo

DRAWING TITLE

Level 7

SHEET NO

001

SCALE


1/200


DATE

DEC 2025

INDEX

0

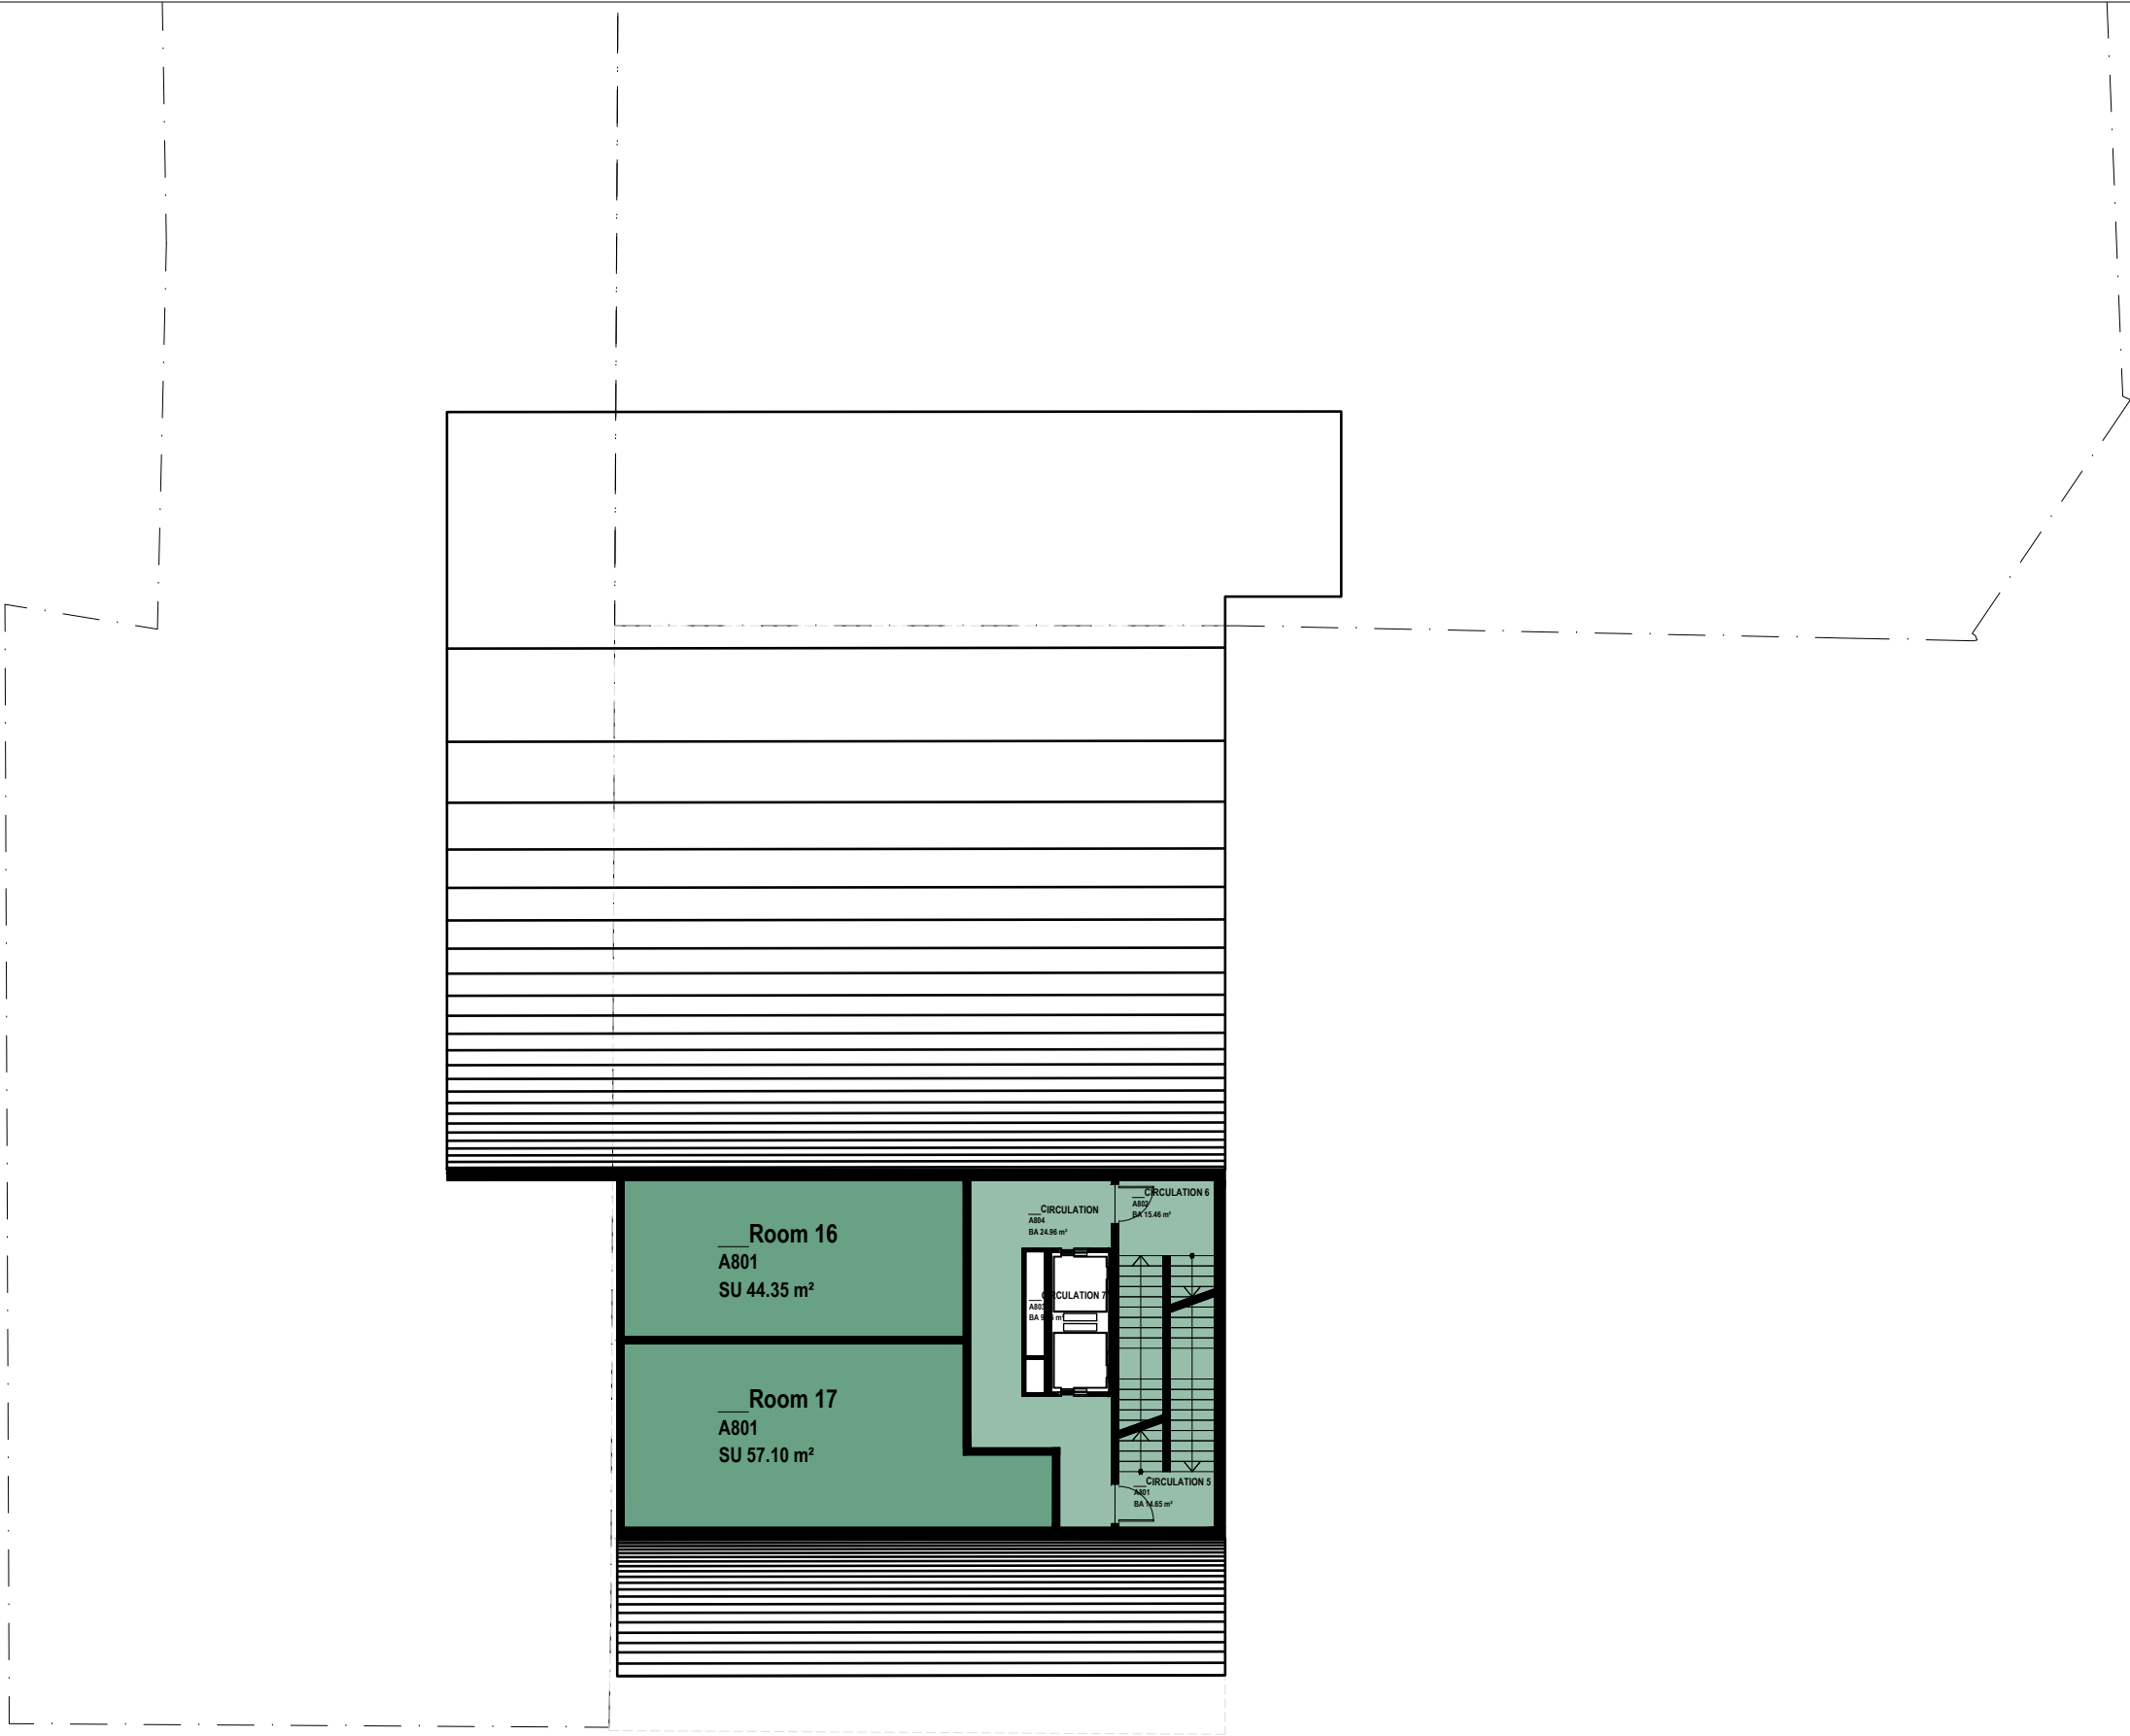

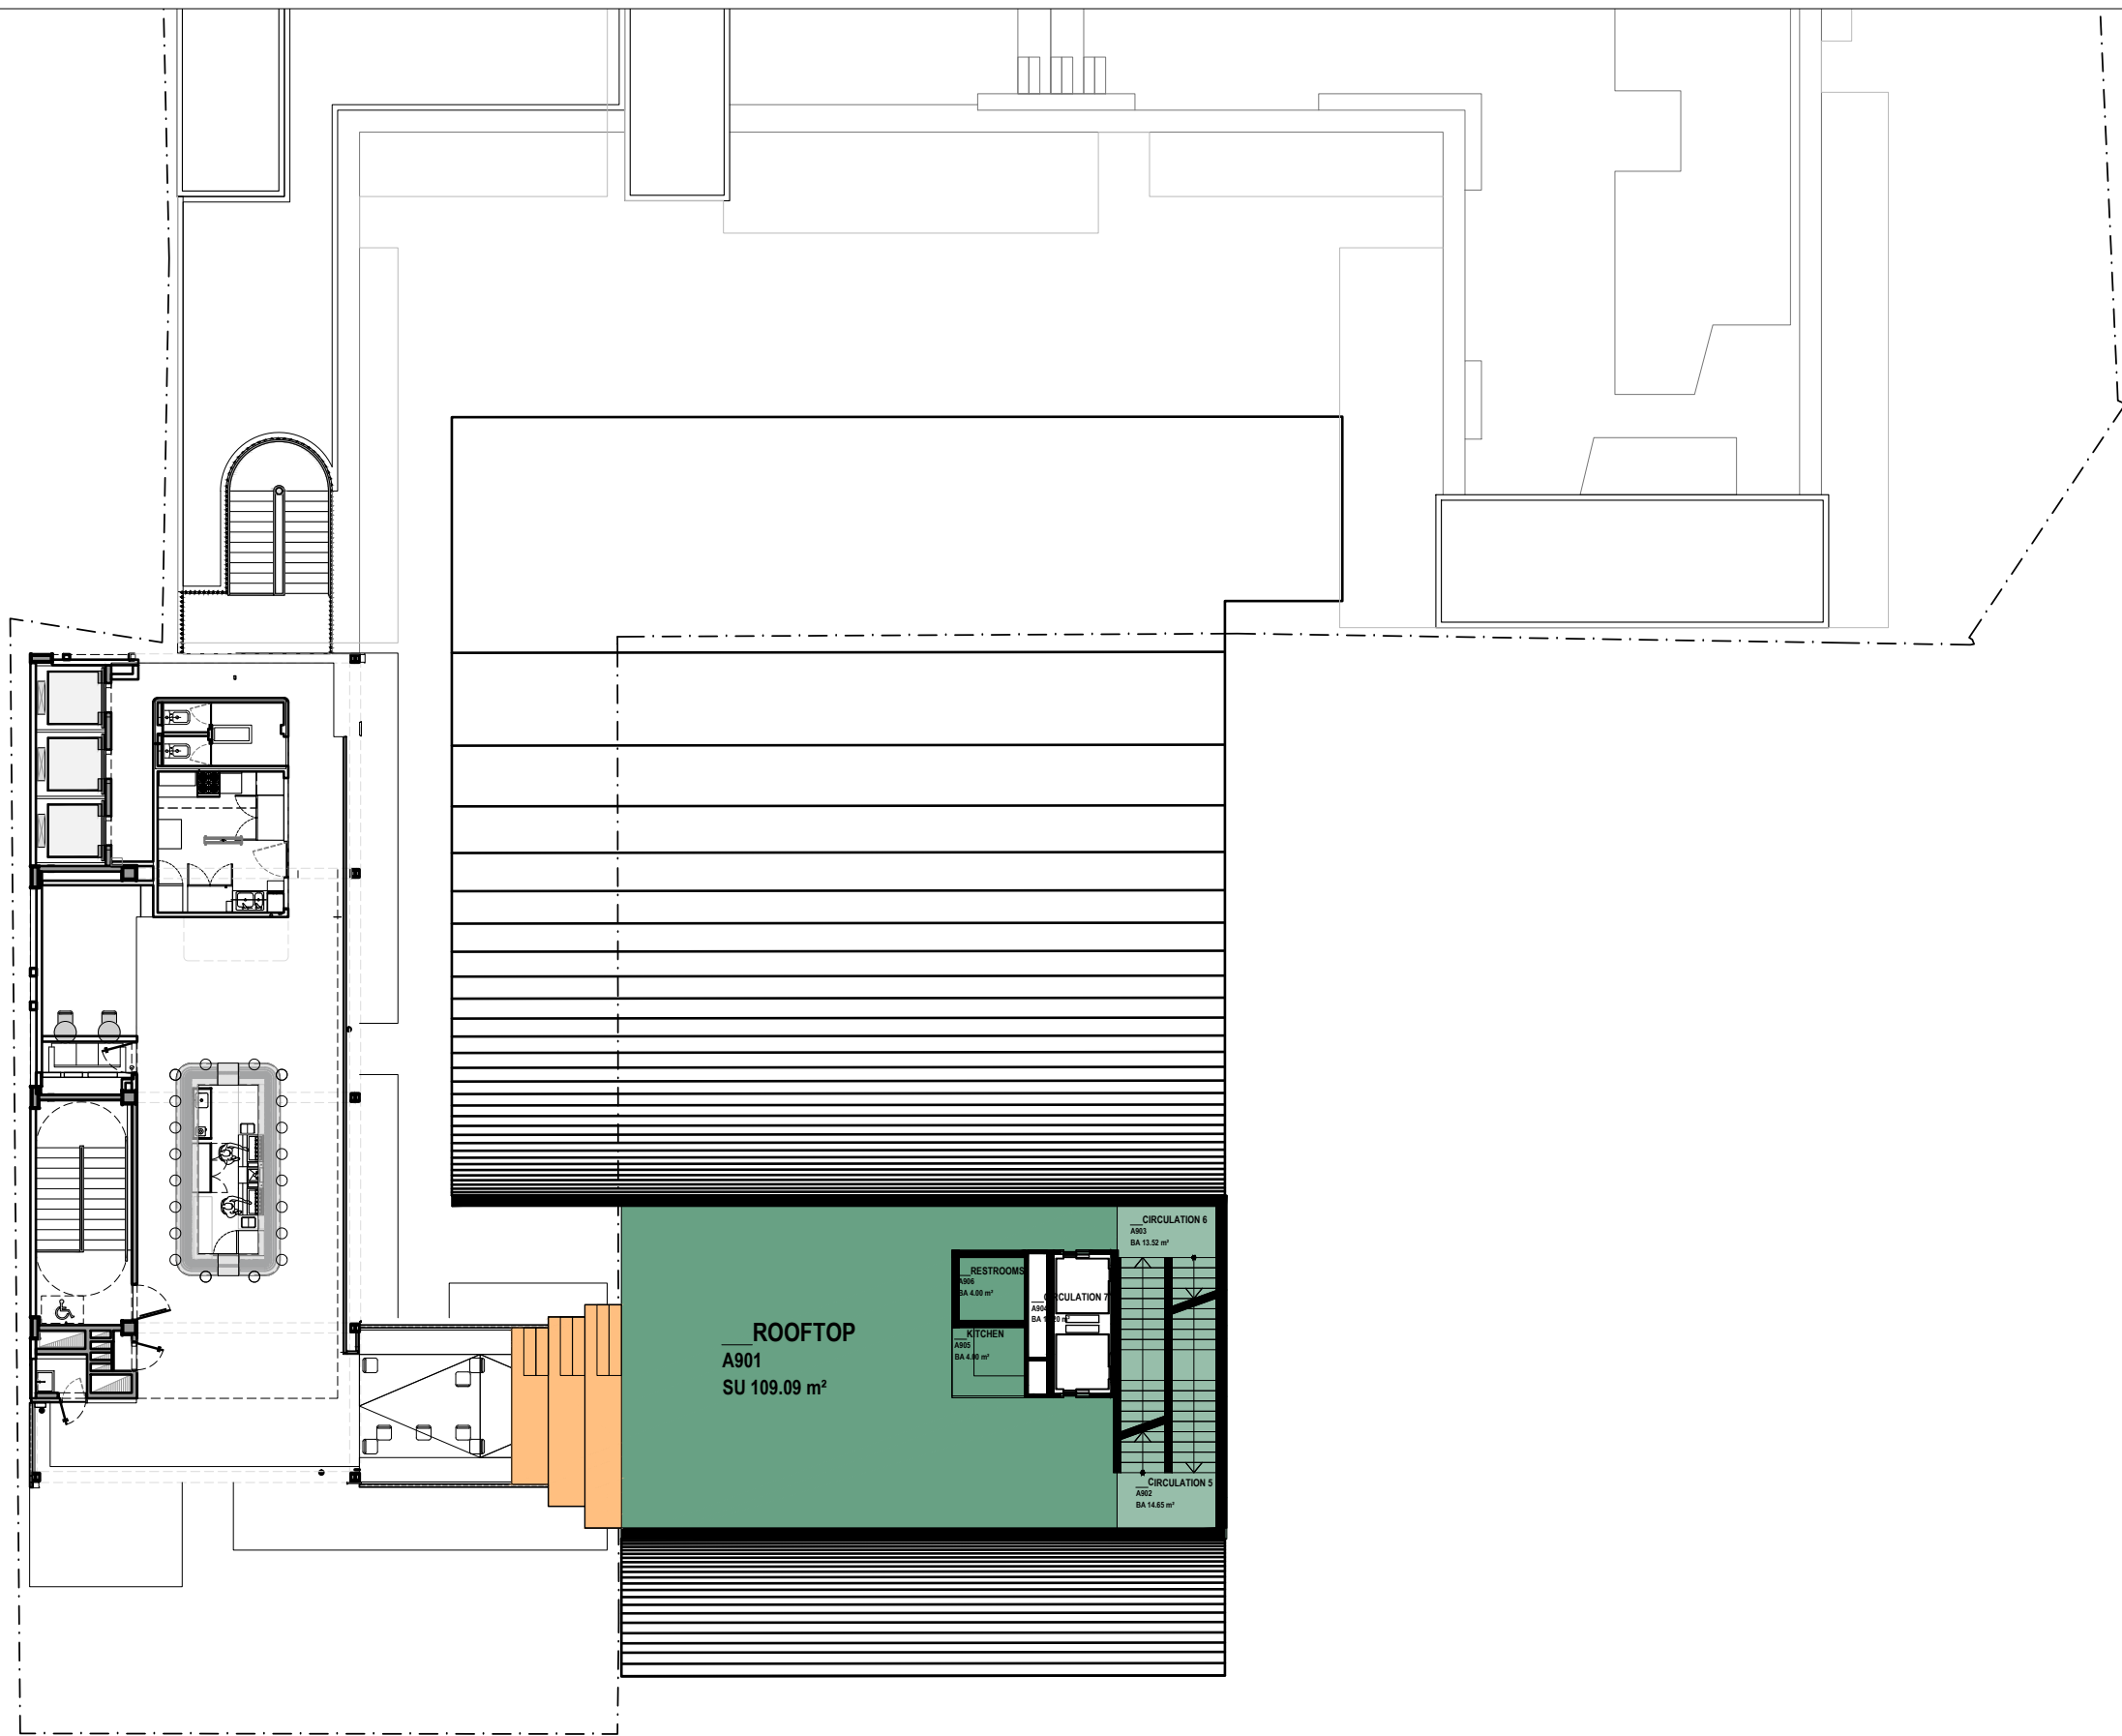

PROJECT

10A

Click Clack Medellín

PHASE

Phase 2

MA

KENGO KUMA & ASSOCIATES

104, rue Oberkampf 75 011 Paris
2-24-8 Minato-ku Minamioyama 107-0062 Tokyo

DRAWING TITLE

B-3

SHEET NO

001

SCALE


1/200


DATE

DEC 2025

INDICE

0

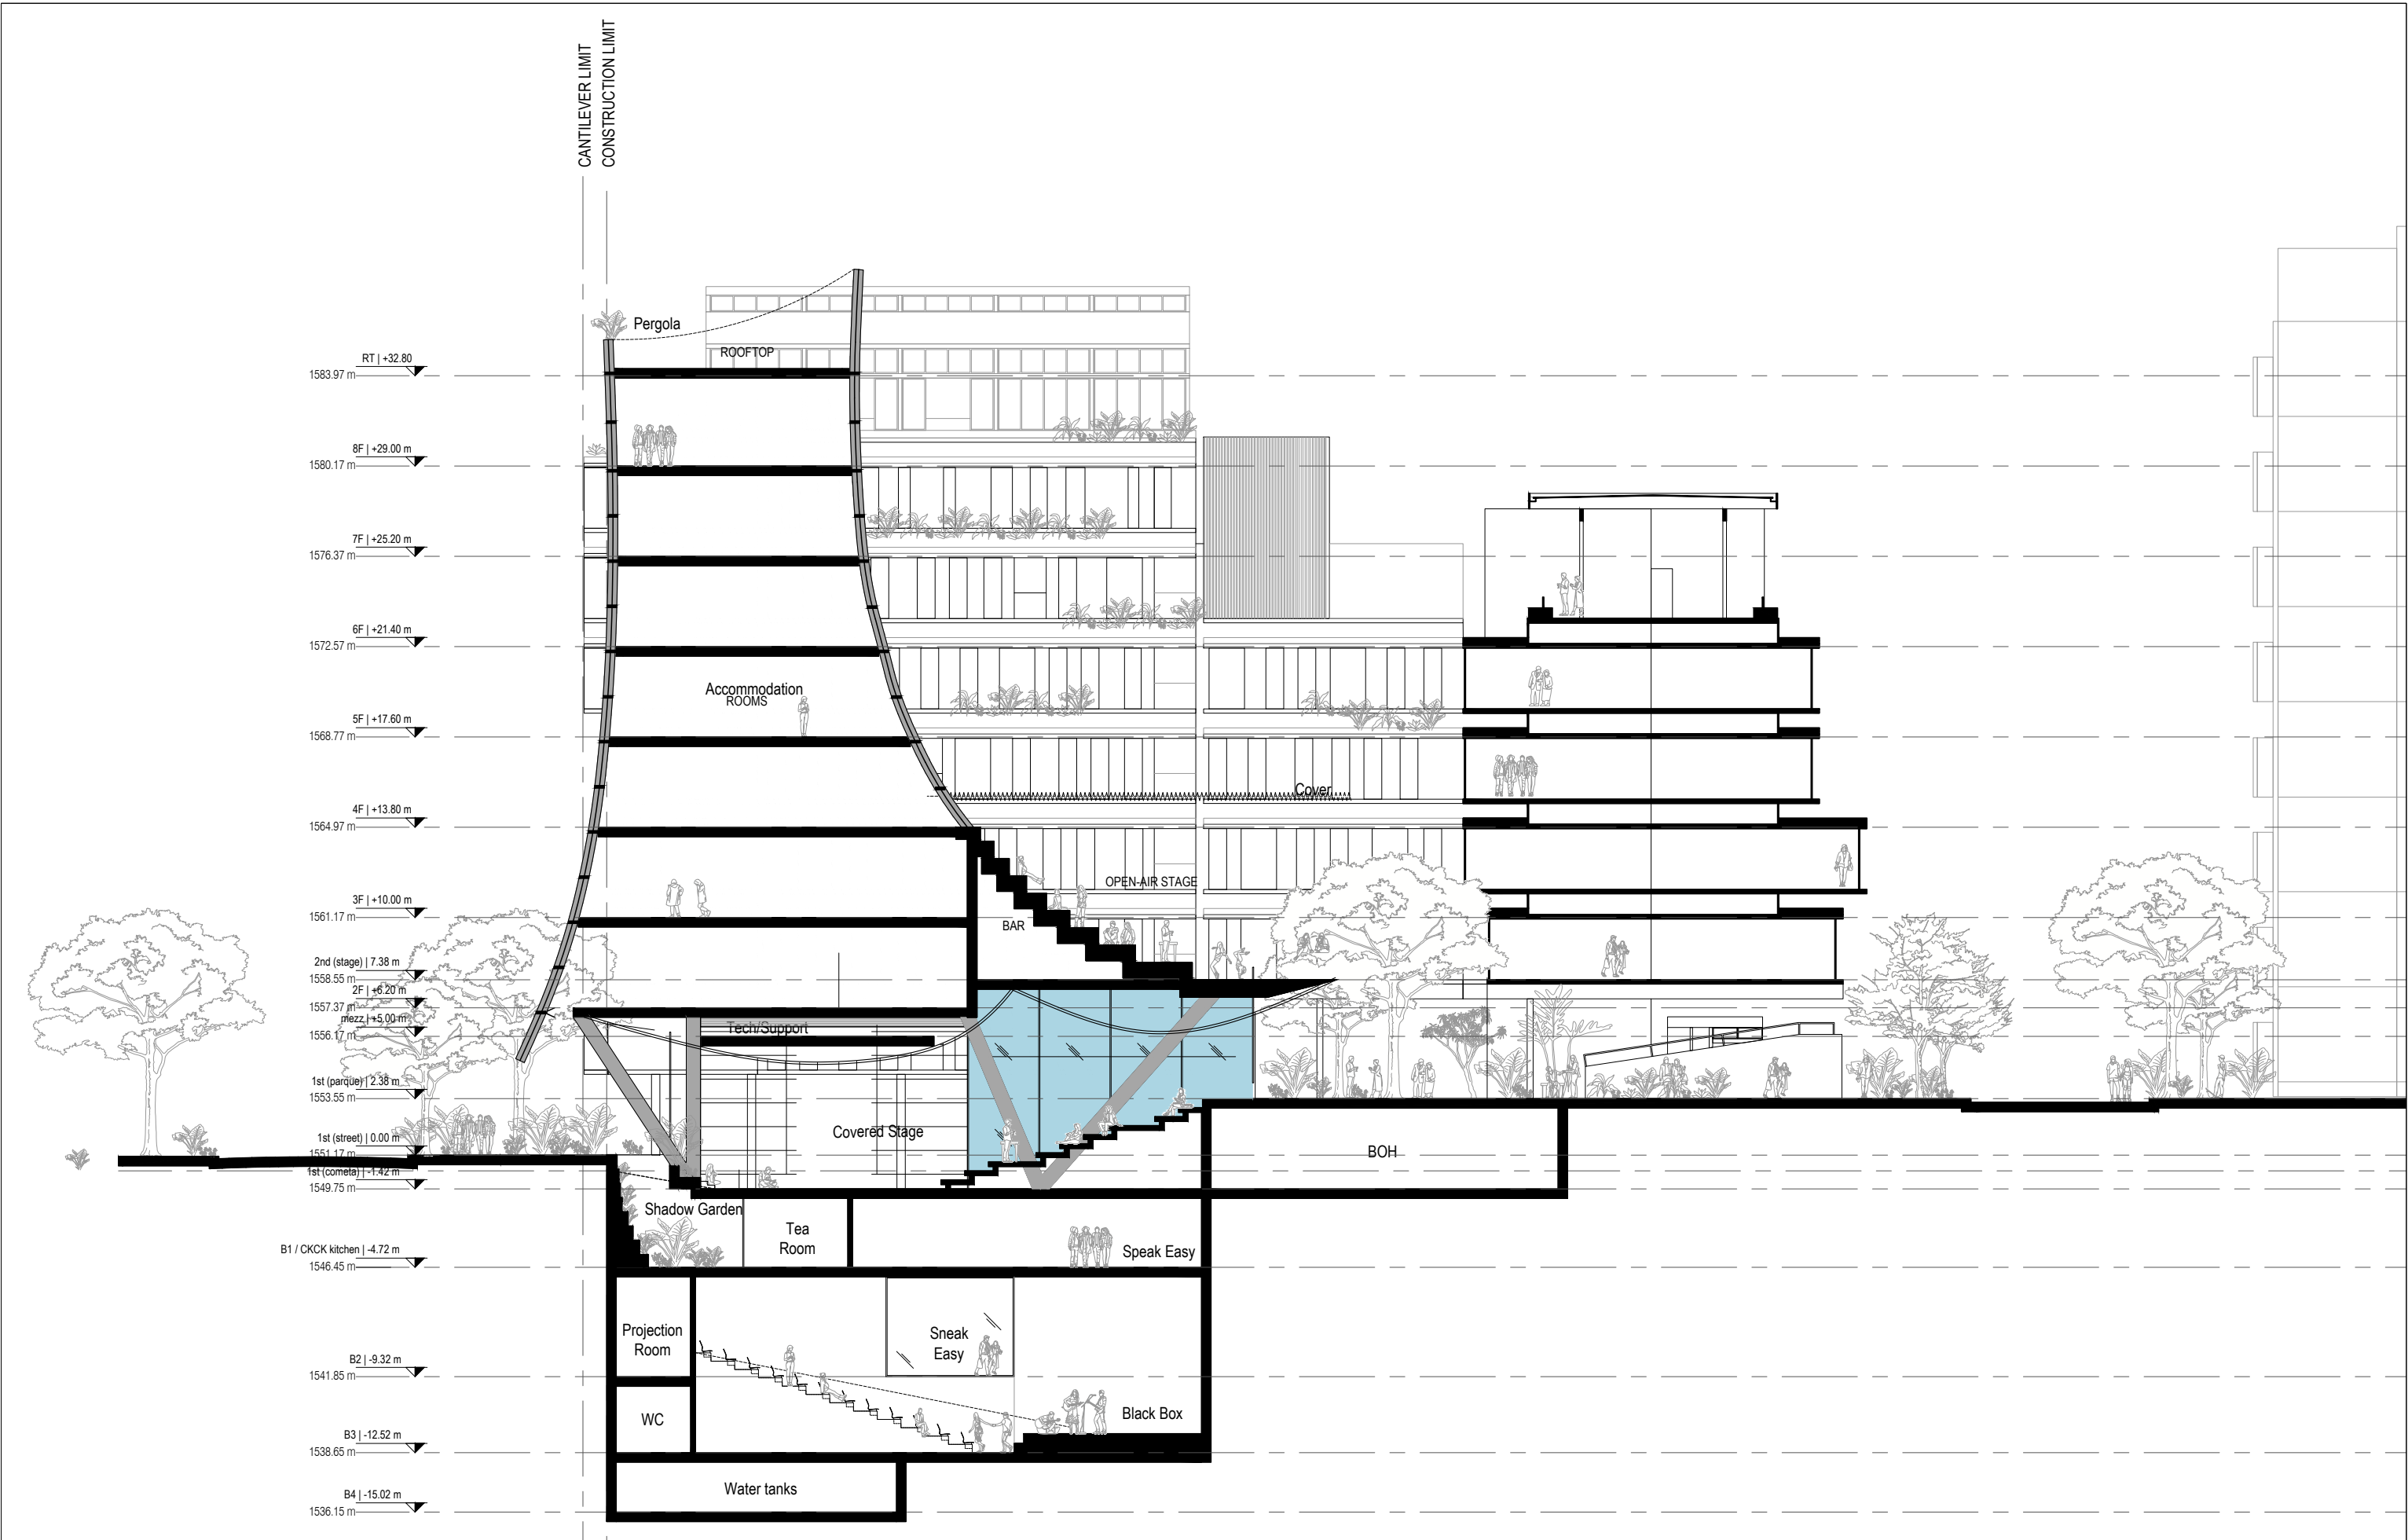


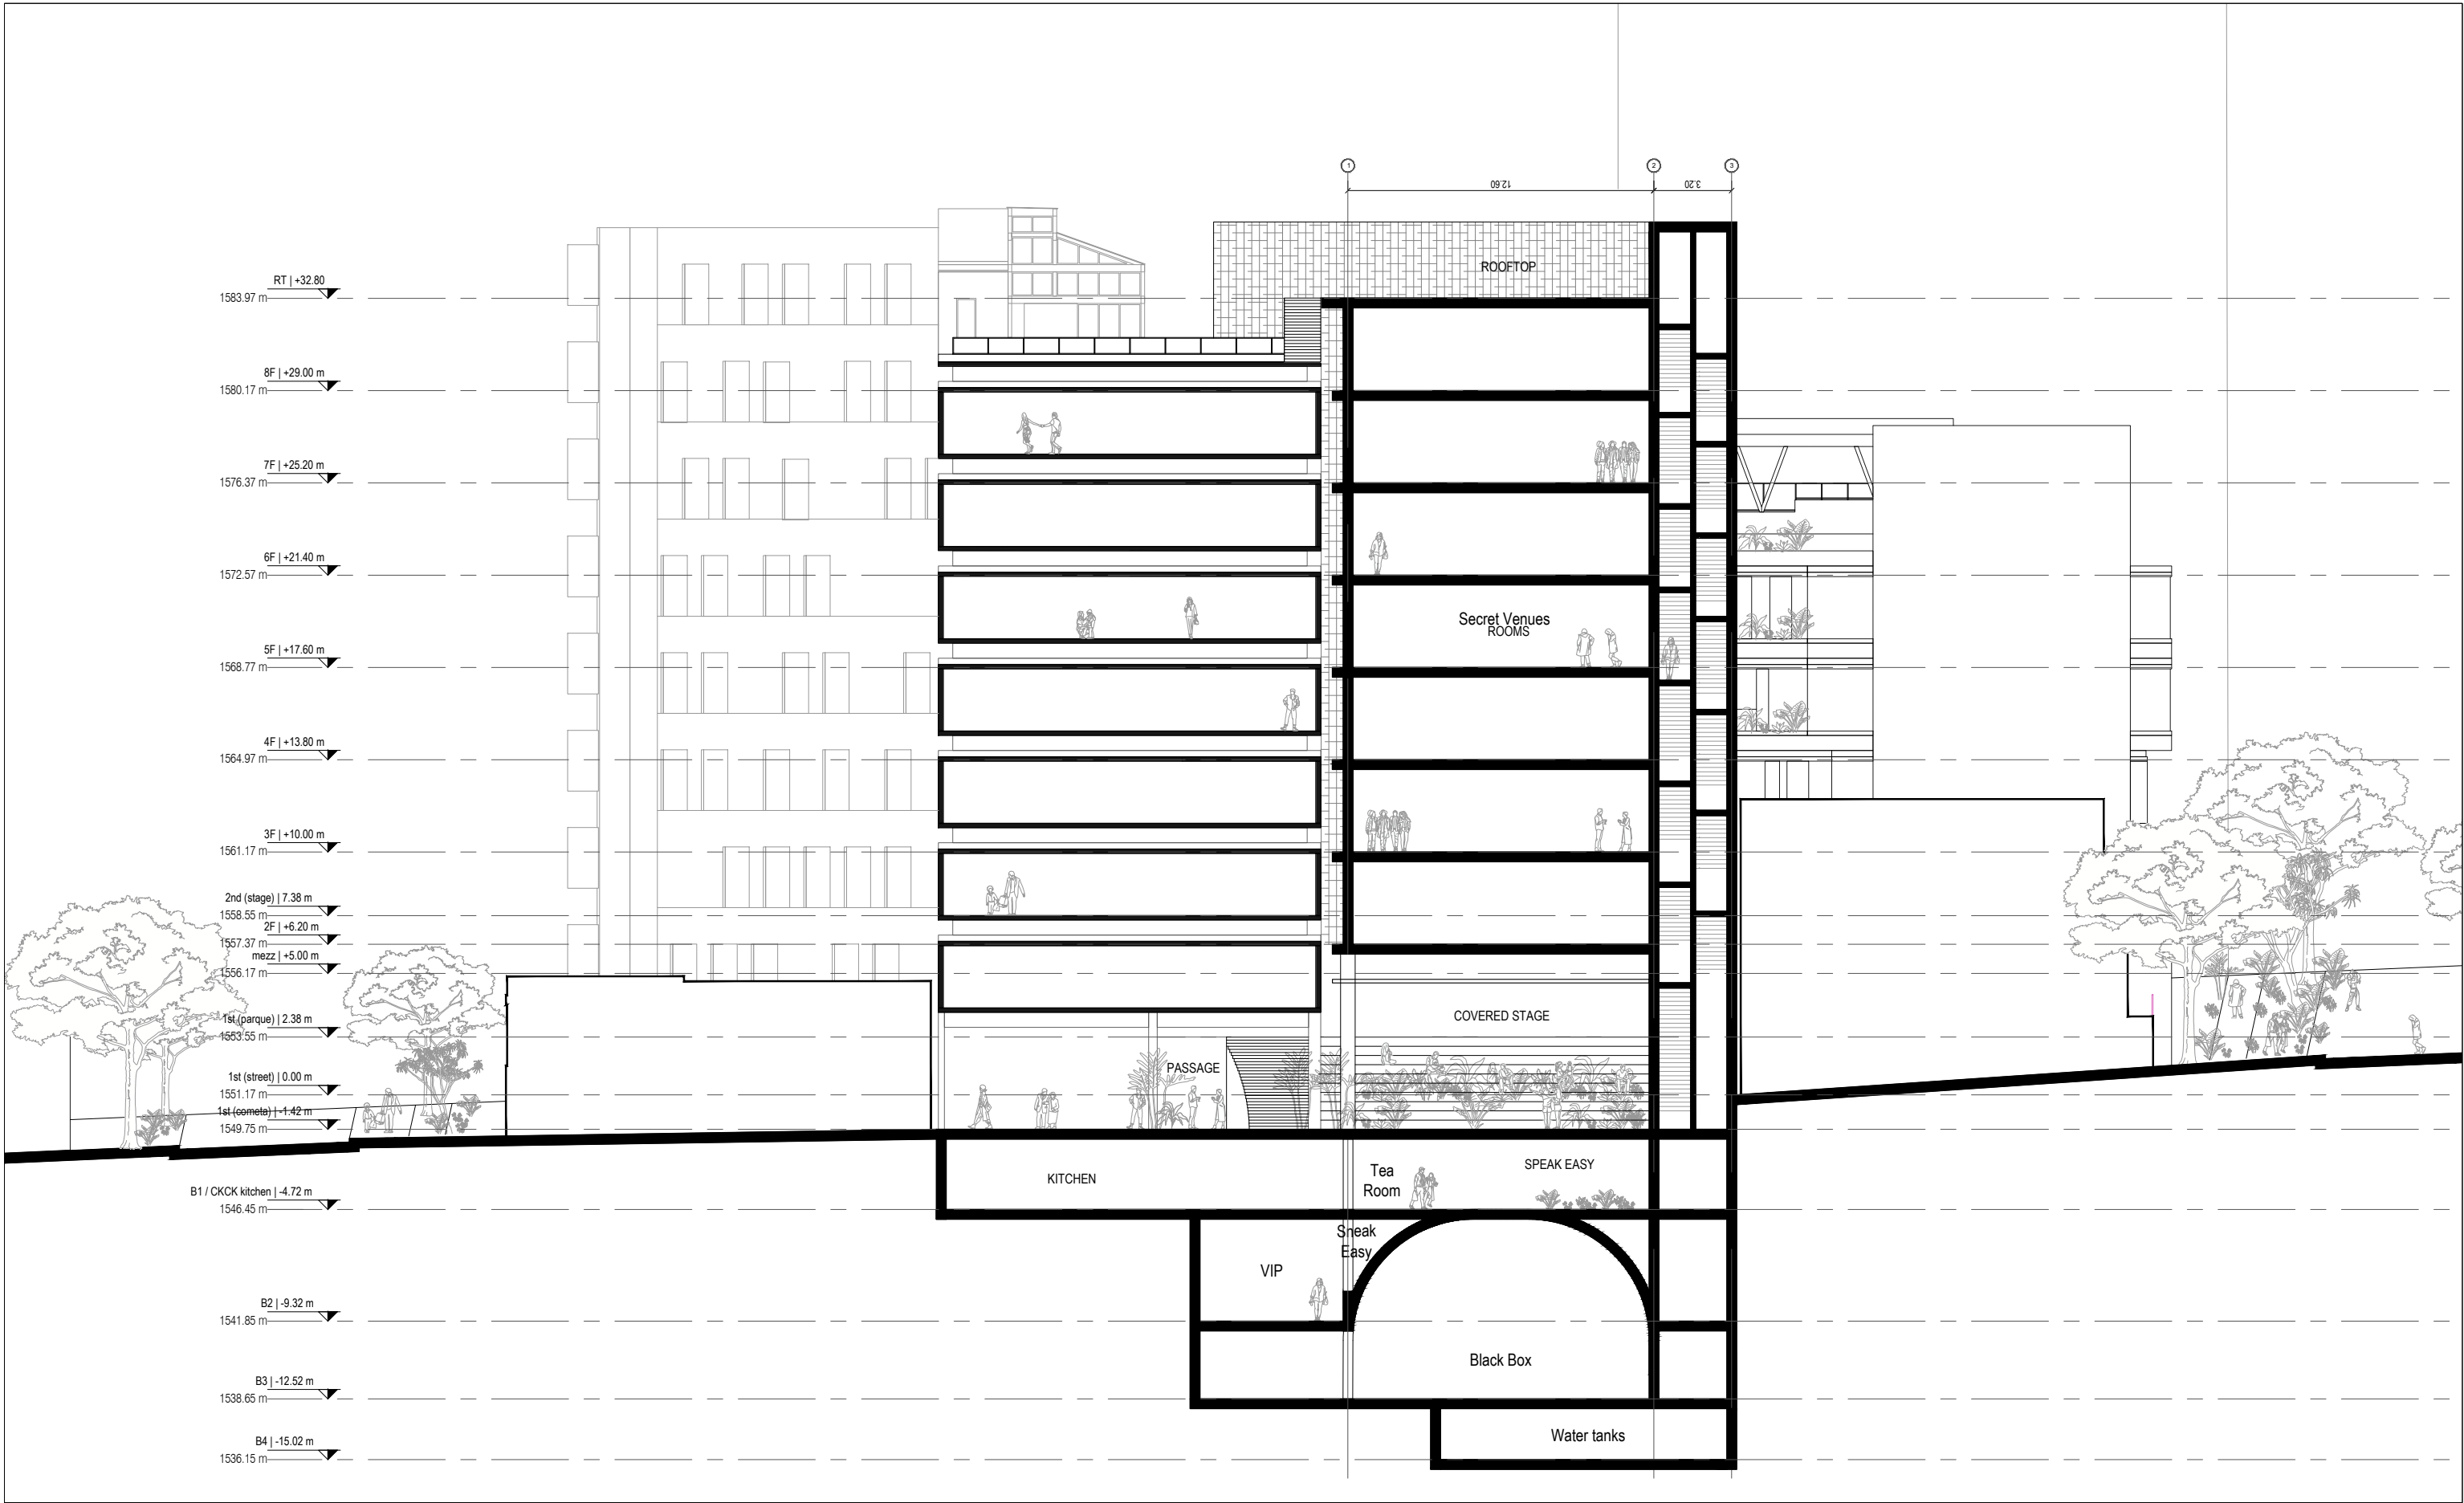


ESQUEMA ACCESO HABITACIONES

[Venue Building] Click Clack by Kengo Kuma

Enero '26

confidencial

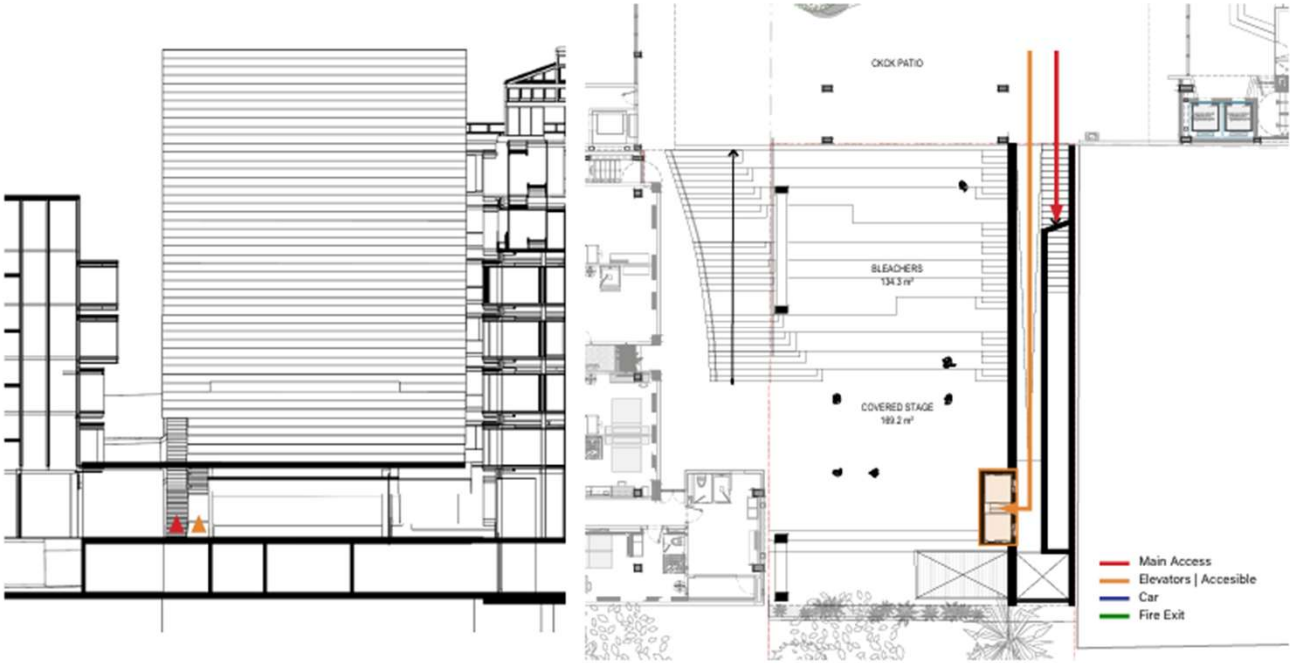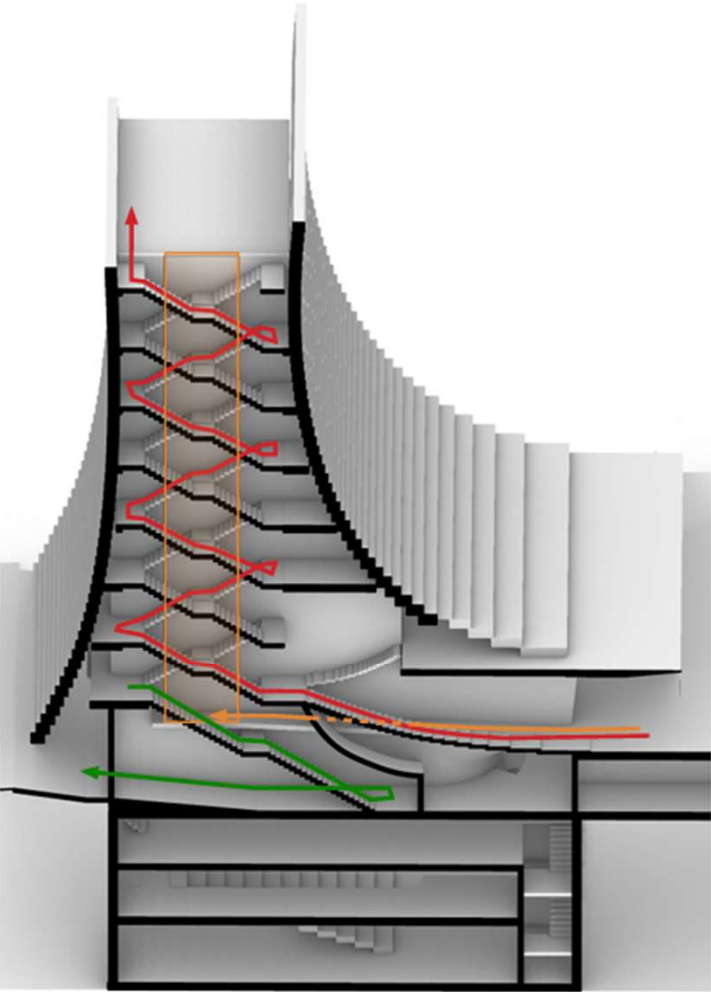


ESQUEMA ACCESO OPEN-AIR STAGE

[Venue Building] Click Clack by Kengo Kuma

Enero
'26

confidencial



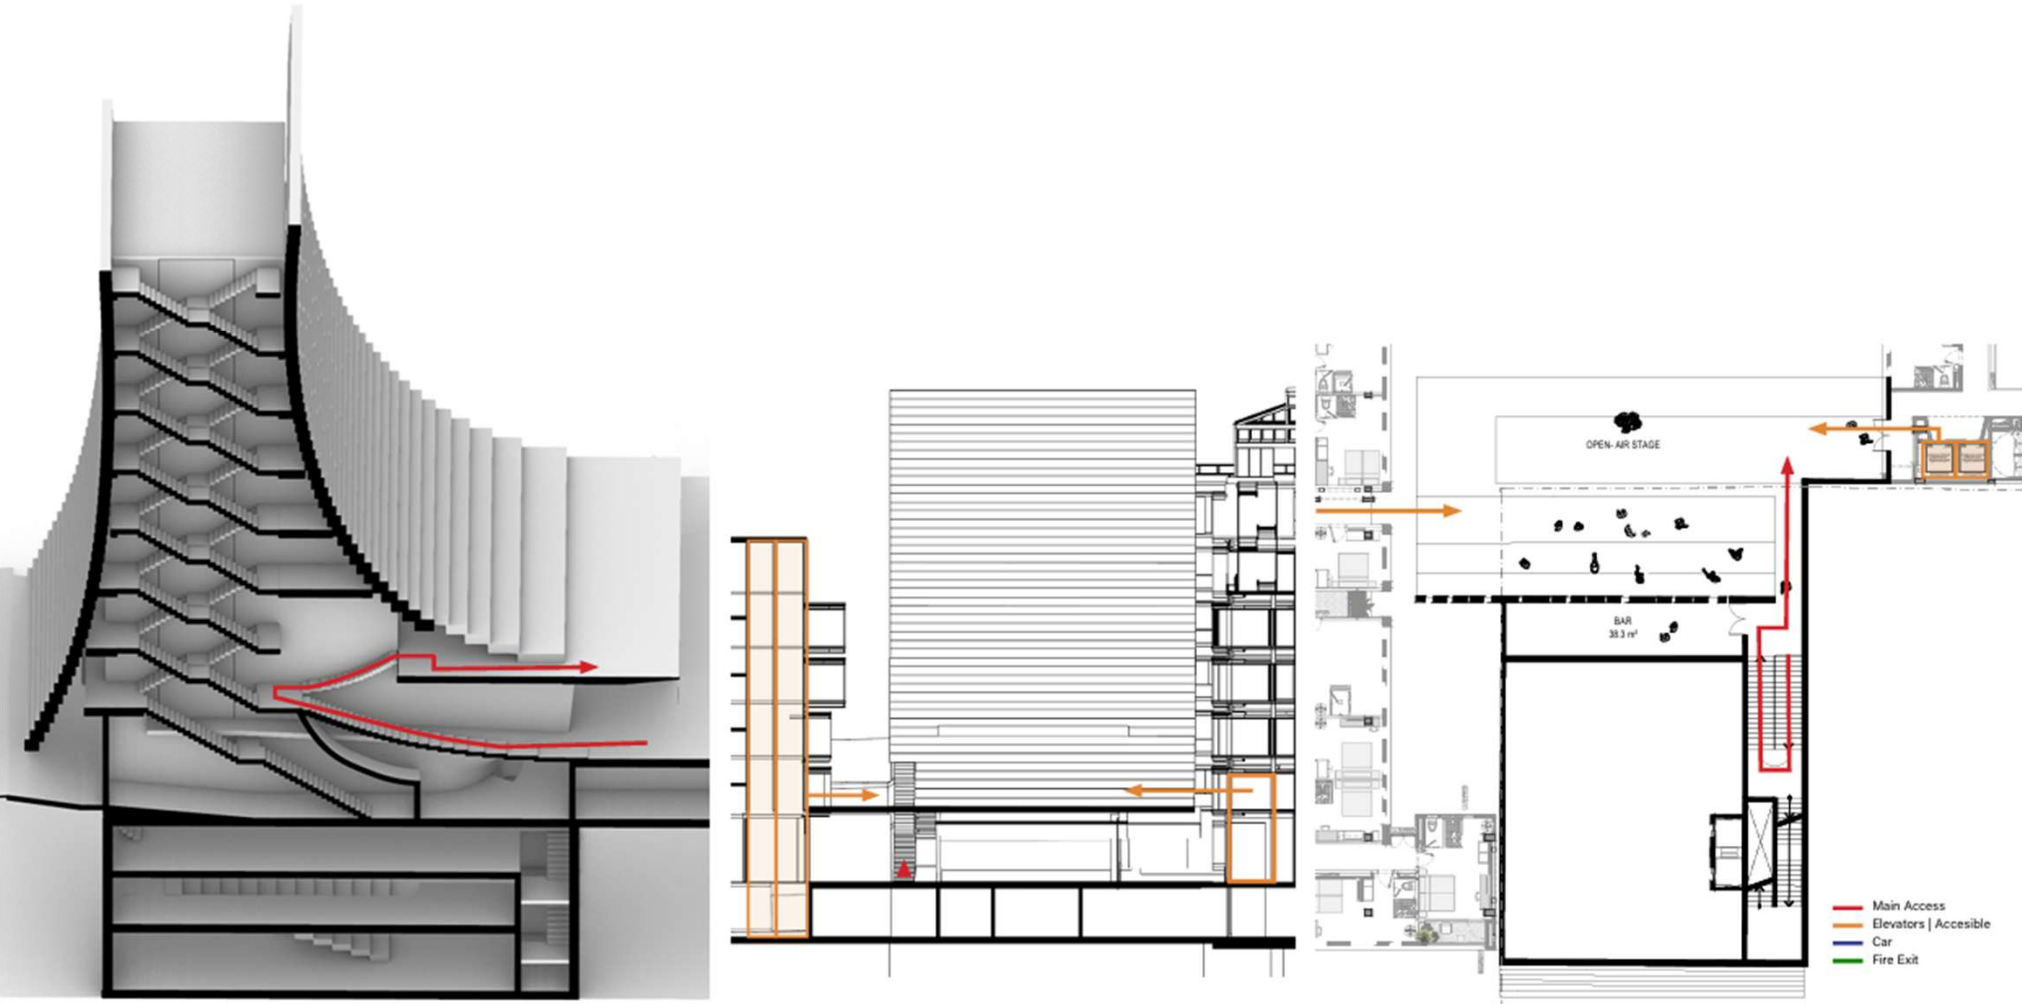


ESQUEMA ACCESO SÓTANO 1 + 2

[Venue Building] Click Clack by Kengo Kuma

Enero '26

confidencial

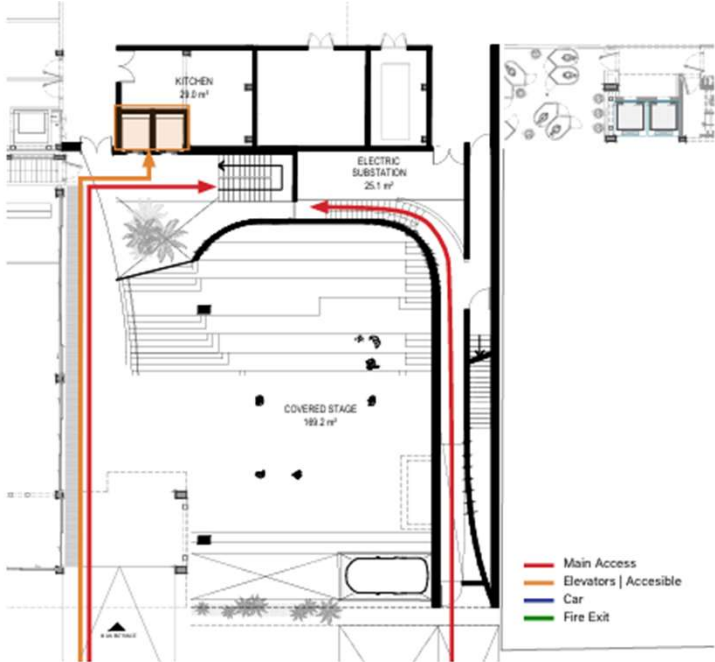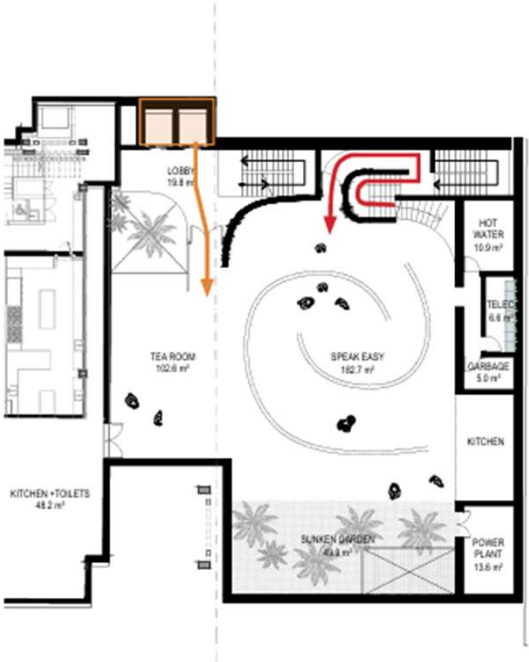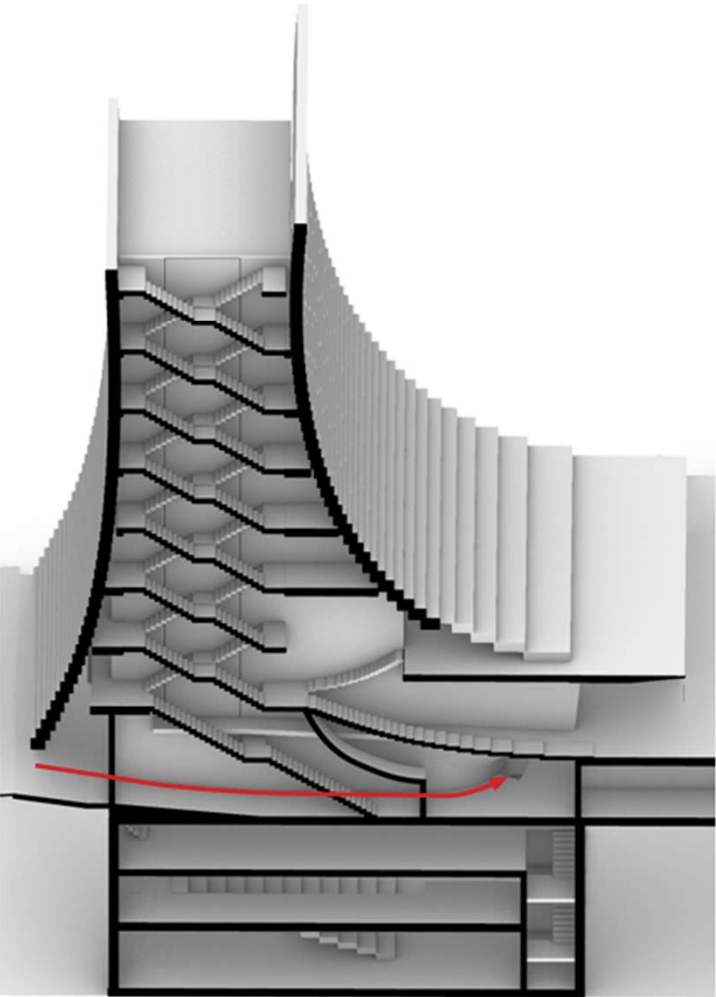

[Venue Building] Click Clack by Kengo Kuma

::


Enero
'26

!

confidencial

LA ENVOLVENTE COMO PAISAJE

PISOS TÉRMICOS

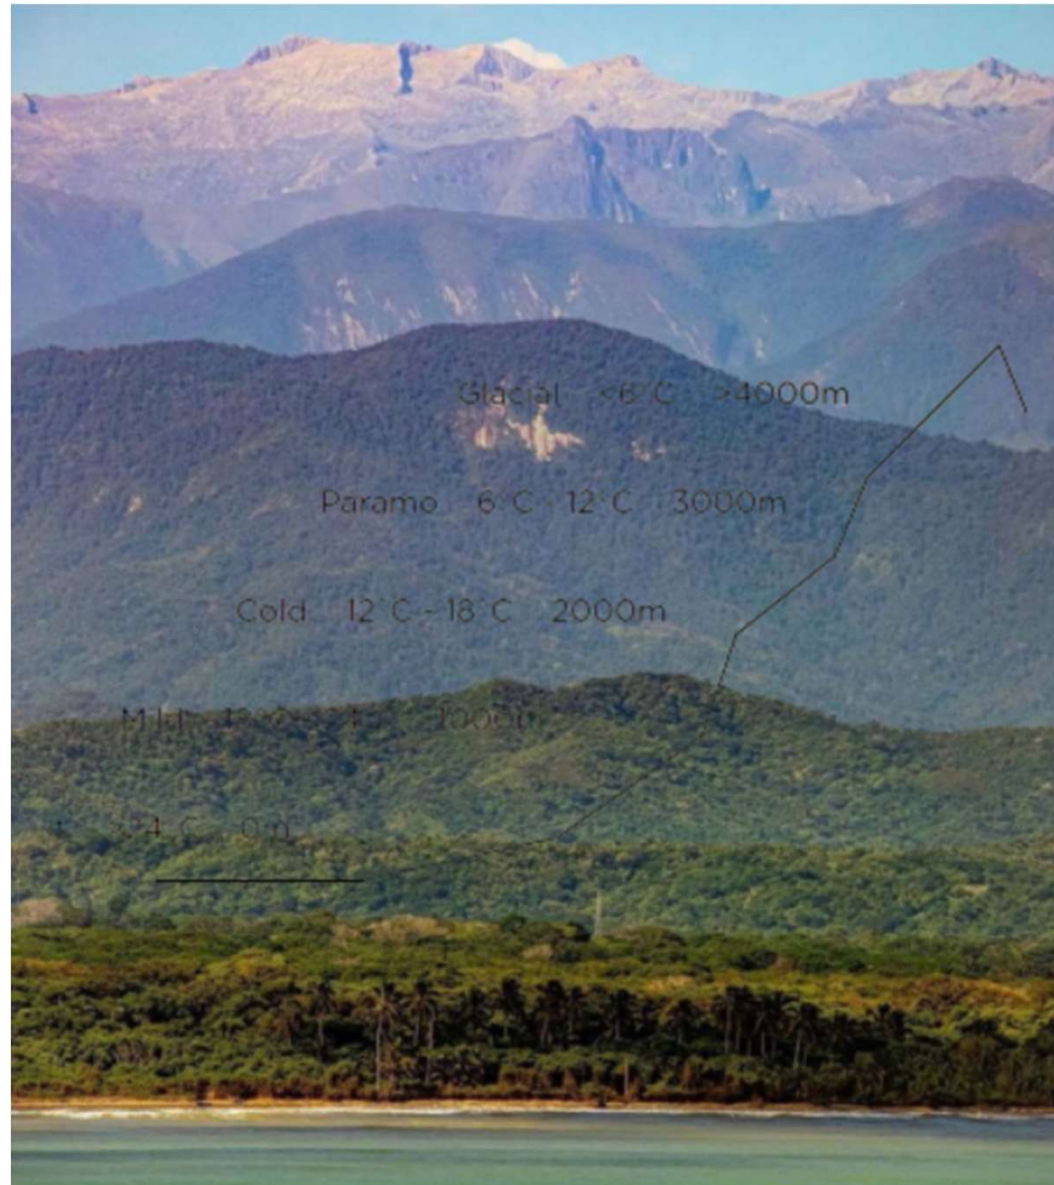

LA ENVOLVENTE COMO PAISAJE

[Venue Building] Click Clack by Kengo Kuma

14


::

Enero
'26

!

confidencial



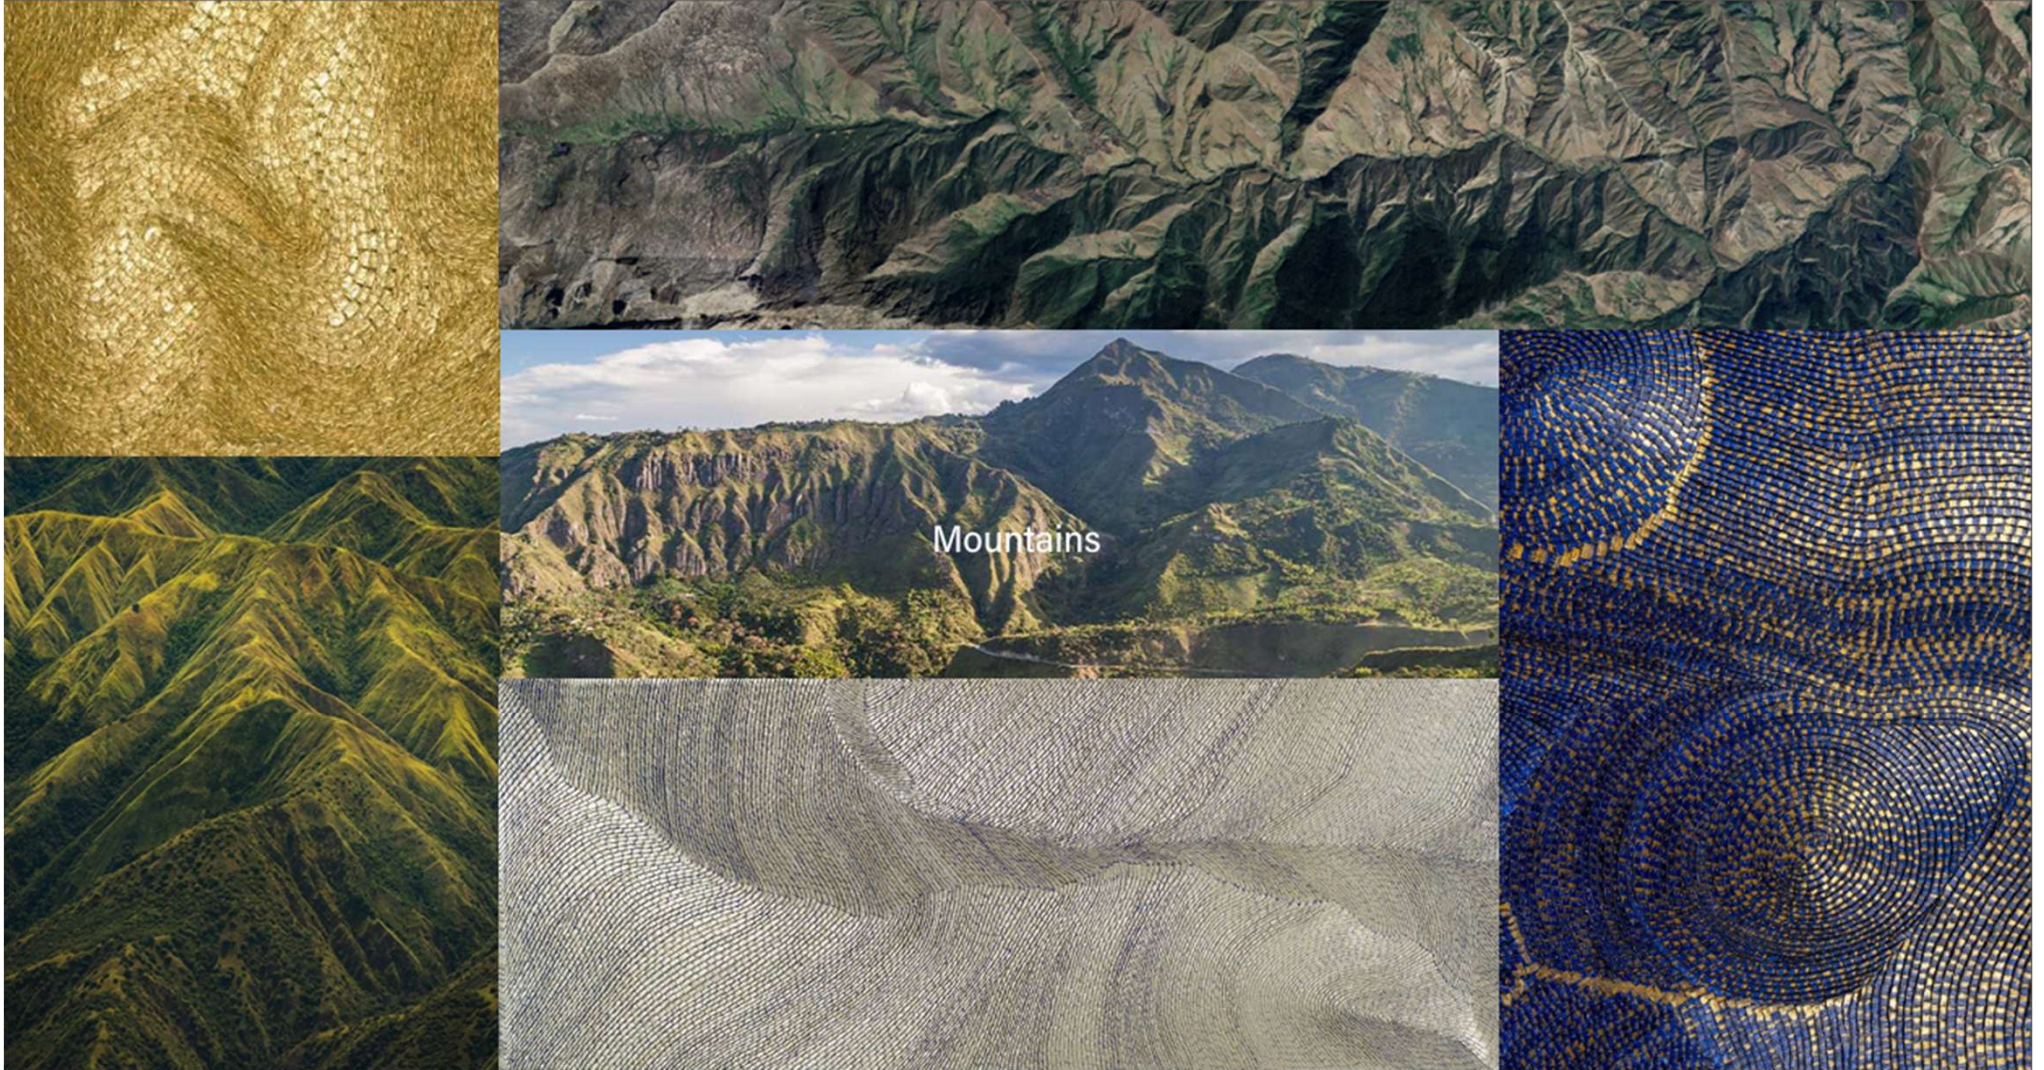


[Venue Building] Click Clack by Kengo Kuma

::

Enero
'26


1

confidencial

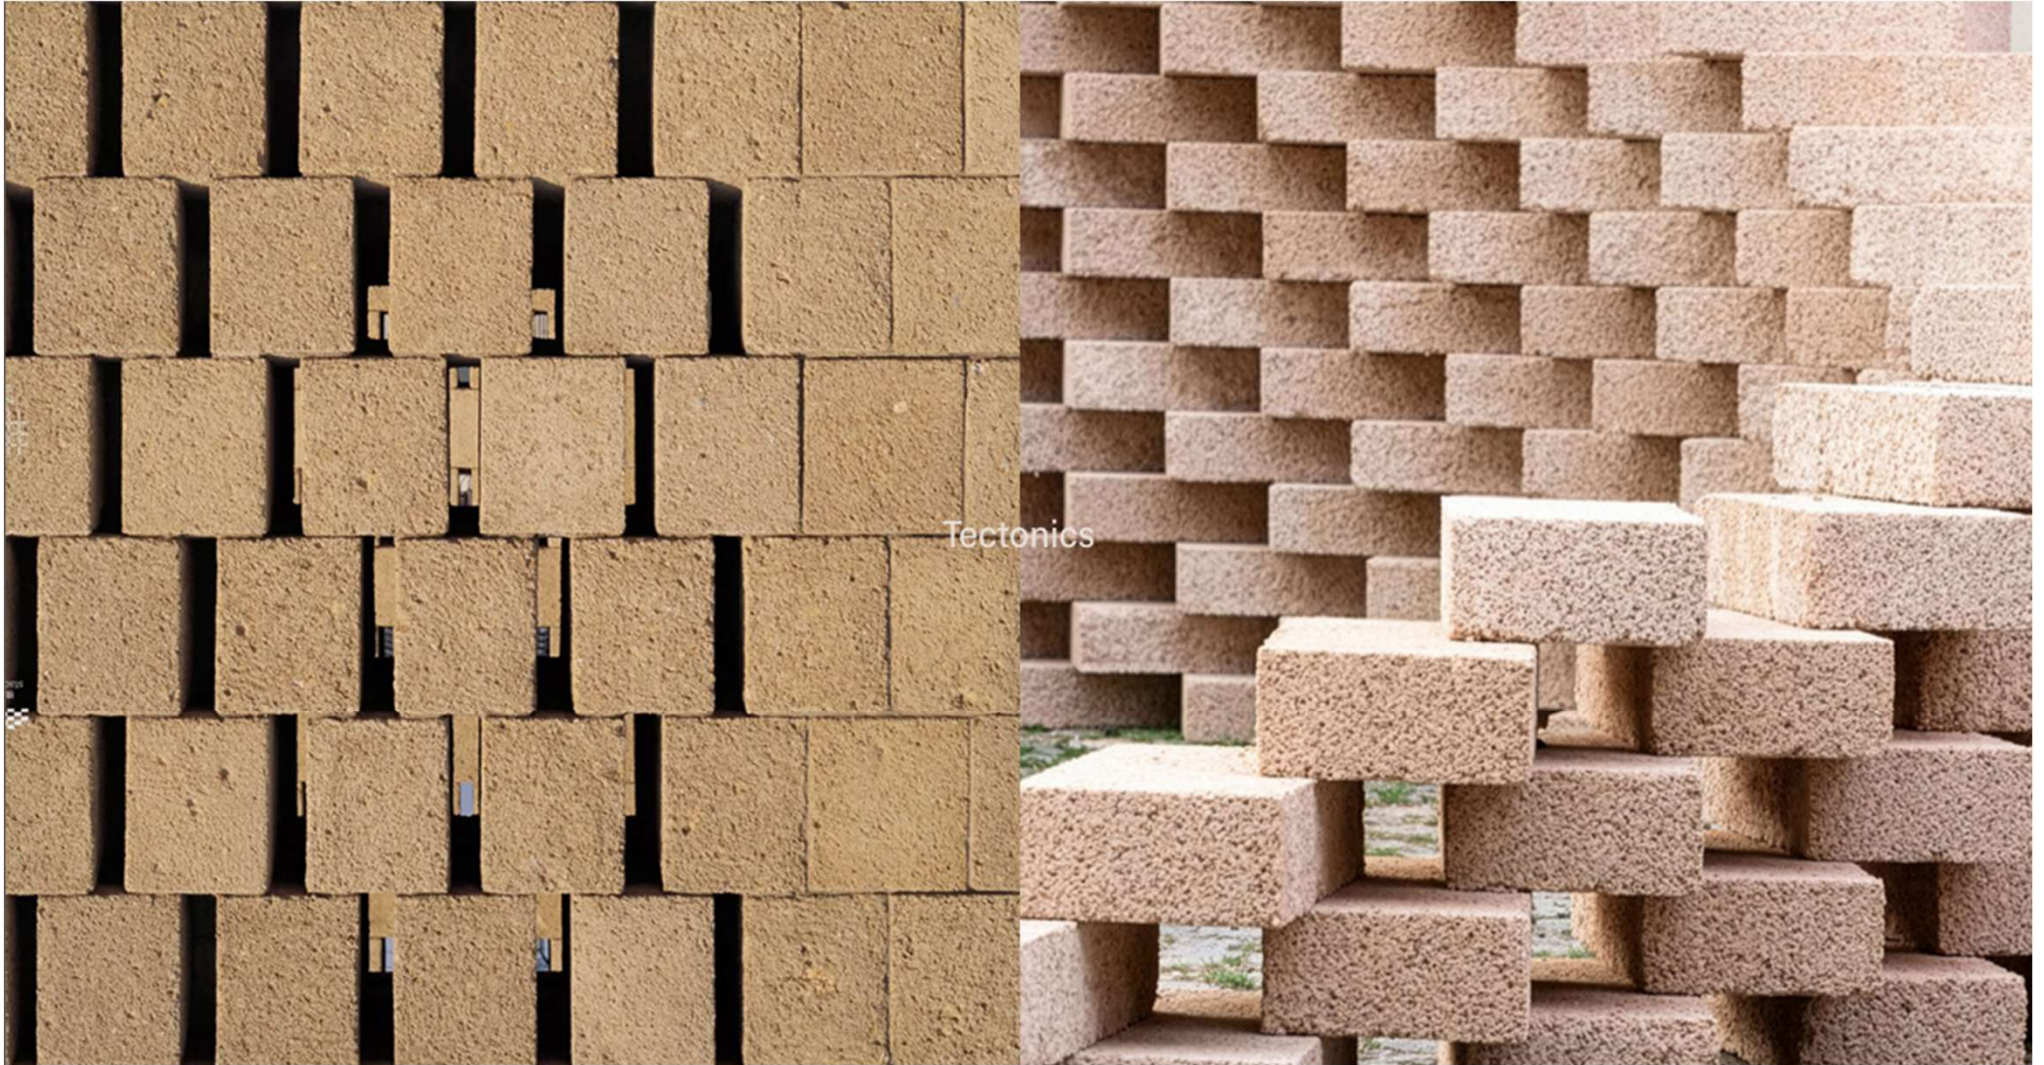






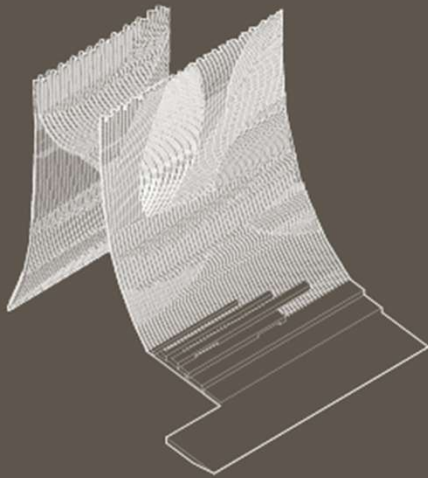


Earth Fabric

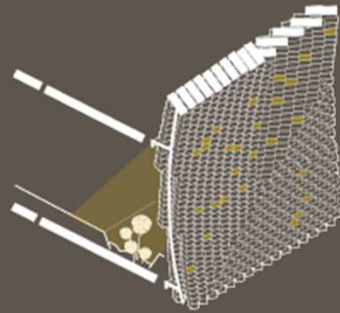

Weaving



Structural Threads

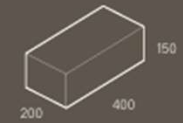

Earth Block

Weaving Earth

MAQUETA

20

[Venue Building] Click Clack by Kengo Kuma

::

Enero
'26

!

confidencial



[Venue Building] Click Clack by Kengo Kuma

::

Enero
'26

!

confidencial




[Venue Building] Click Clack by Kengo Kuma

::

Enero
'26

!

confidencial

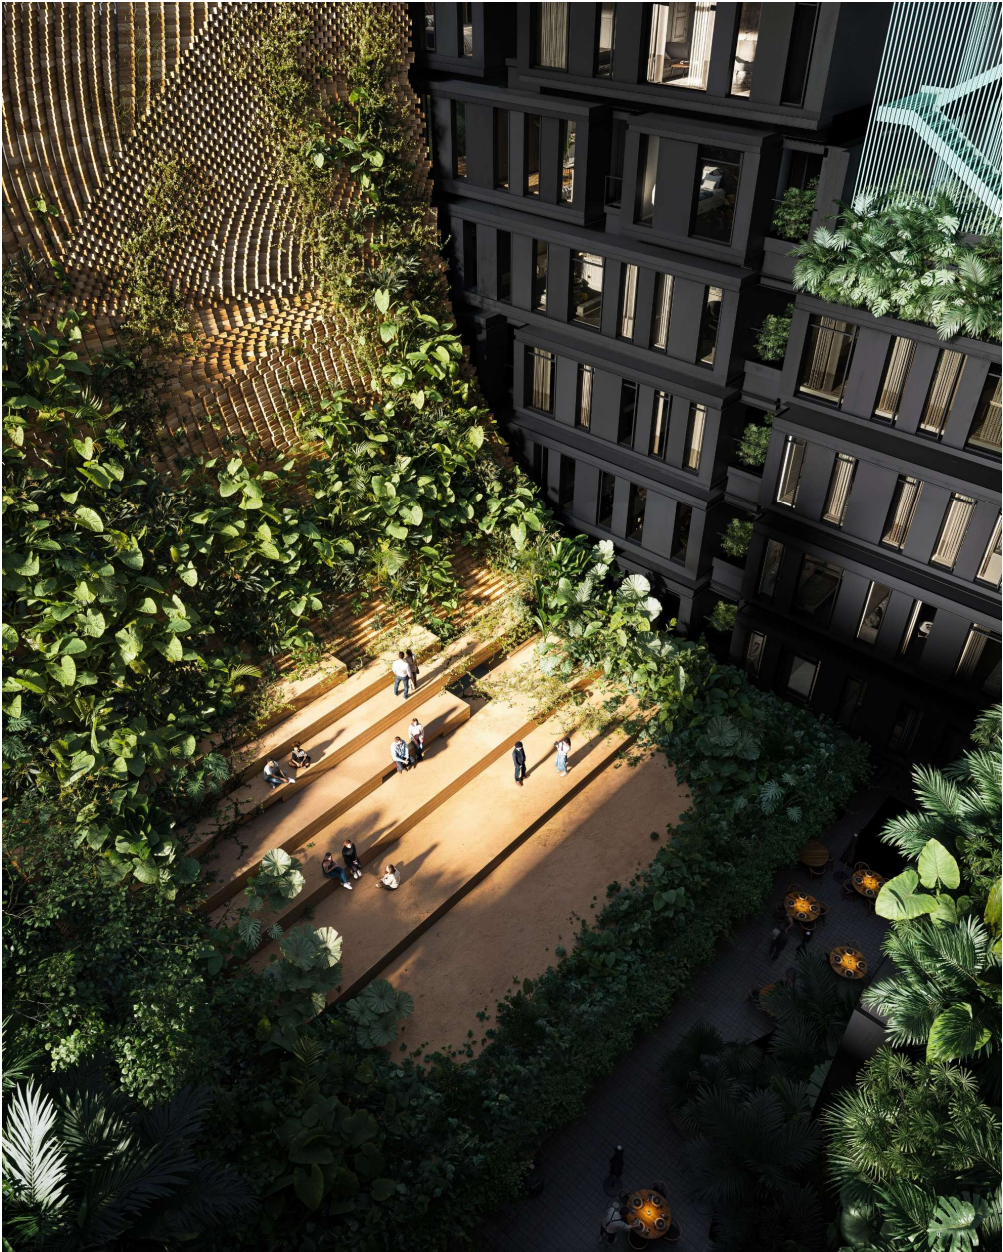

ÁREAS

AREA NORMA + RESUMEN

[Venue Building] Click Clack by Kengo Kuma

24

::

Enero
'26

1

confidencial

AGORA de Click Clack por Kengo Kuma		
CI 10A #37-28	REGULATION	PROJECT
ÁREA BRUTA LOTE	502,74	502,74
FRENTE LOTE	16,84	16,84
FONDO LOTE	30,00	30,00
ALTURA	8 PISOS	8 PISOS
ÁREA ÍNDICE OCUPACIÓN 1 PISO	402,19	431,60
ÍNDICE DE OCUPACIÓN PLATAFORMA	80%	86%
ÁREA ÍNDICE OCUPACIÓN TORRE (4 PISO)	301,64	221,64
ÍNDICE DE OCUPACIÓN TORRE (4 PISO)	60%	56,90%
ÁREA TOTAL CONSTRUIDA		3.348,9
ÁREA QUE CUENTA PARA ÍNDICE DE CONSTRUCCIÓN		
NÚMERO HABITACIONES		17
CELDAS DE CARGUE Y DESCARGUE	1	0
CAR LOBBY	1	0

AREAS OVERVIEW				
FLOOR	SPACE	COVERED GROSS AREA REMUNERATED AREAS		TOTAL
PROGRAMME WITH REVENUE		Within Plot	Extensions	
BASEMENT 3	Black box theatre	541 m²	194 m²	735 m²
BASEMENT 1	Speak Easy / Tea room + Restaurant	288 m²	63 m²	352 m²
FLOOR 1	Covered stage	300 m²		300 m²
MEZZANINE	Open-air stage	144 m²	102 m²	246 m²
FLOOR 2 TO 8	Accommodation 17 rooms aprox 60m2	967 m²		967 m²
FLOOR 9	Rooftop	118 m²		118 m²
TOTAL REVENUE		2.359 m²	359 m²	2.718 m²
ALL FLOORS	Circulations	869 m²	74 m²	943 m²
ALL FLOORS	Technical areas	219 m²		219 m²
TOTAL BUILT		3.447 m²	433 m²	3.880 m²
TOTAL Commercial m2		1.392 m²	6 commercial units	
TOTAL Accommodation m2		967 m²	17 bedrooms	

hm

AREA POR PISO

[Venue Building] Click Clack by Kengo Kuma

::

Enero
'26


confidencial

PROGRAM	ROOM	WITHIN NEW PLOT		EXTENSION EXISTING PLOT		EXTENSION EXISTING PLOT		TOTAL NEW AND REFURBISHED COVERED AREA Gross
		BUILT Gross	UNCOVERED Gross	NEW BUILD Gross	NEW UNCOVERED Gross	INTERIOR REFURBISHMENT Gross	EXTENSIONS UNCOVERED REFURBISHMENT Gross	
BASEMENT 4								
Technical floor	Fire Protection Water tank	46 m²						46 m²
Technical floor	Water Supply Water tank	49 m²						49 m²
Technical floor	Lift Pit	20 m²						20 m²
		116 m²	0 m²	0 m²	0 m²	0 m²	0 m²	116 m²
BASEMENT 3								
Black box theatre	Lobby			38 m²				38 m²
Black box theatre	Bar	10 m²		44 m²				55 m²
Black box theatre	Stage + Seating	212 m²						212 m²
Black box theatre	Backstage	76 m²						76 m²
Black box theatre	Restrooms W/M	45 m²		24 m²				69 m²
Black box theatre	Green Room	13 m²						13 m²
Black box theatre	Vertical circulation (service lift)	29 m²						29 m²
Black box theatre	Vertical circulation 2	24 m²						24 m²
Black box theatre	Vertical circulation 3	18 m²						18 m²
Black box theatre	Vertical circulation 4			17 m²				17 m²
		426 m²	0 m²	124 m²	0 m²	0 m²	0 m²	550 m²
BASEMENT 2								
Black box theatre	Lobby	3 m²		19 m²				23 m²
Black box theatre	VIP	48 m²		68 m²				115 m²
Black box theatre	Restrooms W/M	42 m²						42 m²
Black box theatre	Storage	79 m²						79 m²
Black box theatre	Technical for show	13 m²						13 m²
Black box theatre	Vertical circulation (service lift)	16 m²						16 m²
Black box theatre	Vertical circulation 2	33 m²						33 m²
Black box theatre	Vertical circulation 3	18 m²						18 m²
Black box theatre	Vertical circulation 4			8 m²				8 m²
		251 m²	0 m²	94 m²	0 m²	0 m²	0 m²	345 m²
BASEMENT 1								
Speak Easy / Tea room	Lobby commercial area	3 m²		18 m²				21 m²
Speak Easy / Tea room	Tea room	20 m²		63 m²				83 m²
Speak Easy / Tea room	Speak Easy	215 m²		1 m²				216 m²
Speak Easy / Tea room	Shadow Garden	54 m²						54 m²
Speak Easy / Tea room	Restrooms W/M					57 m²		57 m²
Technical area	Power plant	21 m²						21 m²
Technical area	Technical circulation	6 m²						6 m²
Technical area	Garbage room	7 m²						7 m²
Technical area	Telecommunications	10 m²						10 m²
Technical area	Hot water	11 m²						11 m²
Speak Easy / Tea room	Vertical circulation (service lift)	5 m²						5 m²
Speak Easy / Tea room	Vertical circulation 2	39 m²						39 m²
Speak Easy / Tea room	Vertical circulation 3	18 m²						18 m²
Speak Easy / Tea room	Vertical circulation 4			6 m²				6 m²
		408 m²	0 m²	87 m²	0 m²	57 m²	0 m²	551 m²
FLOOR 1								
Covered stage	Covered stage	151 m²						151 m²
Covered stage	Bleachers	150 m²			49 m²			150 m²
Covered stage	Kitchen		152 m²		74 m²	33 m²	145 m²	0 m²
Covered stage	Outdoor passage (urbanism)							0 m²
Covered stage	Electric Substation	27 m²				20 m²		47 m²
Covered stage	Vertical circulation (service lift)	3 m²						3 m²
Covered stage	Vertical circulation 2	90 m²						90 m²
Covered stage	Vertical circulation 3	22 m²						22 m²
Covered stage	Vertical circulation 4			13 m²		9 m²		0 m²
Covered stage	Vertical circulation 5	20 m²						20 m²
Covered stage	Vertical circulation 6	16 m²						16 m²
Covered stage	Vertical circulation 7	43 m²						43 m²
		521 m²	152 m²	13 m²	123 m²	62 m²	145 m²	393 m²
FLOOR 2								
Accommodation	Room 1		36 m²					36 m²
Accommodation	Room 2		36 m²					36 m²
Accommodation	Room 3		57 m²					57 m²
Accommodation	Room 4		47 m²					47 m²
Open air stage	open air stage		46 m²					46 m²
Accommodation	Storage		9 m²					9 m²
Accommodation	Vertical circulation		64 m²					64 m²
Accommodation	Circulation		30 m²					30 m²
		325 m²	98 m²	102 m²	0 m²	4 m²	77 m²	432 m²
FLOOR 3								
Accommodation	Room 5		32 m²					32 m²
Accommodation	Room 6		77 m²					77 m²
Accommodation	Room 7		87 m²					87 m²
Accommodation	Storage		11 m²					11 m²
Accommodation	Vertical circulation		28 m²					28 m²
Accommodation	Circulation		35 m²					35 m²
		271 m²	0 m²	0 m²	0 m²	0 m²	0 m²	271 m²
FLOOR 4								
Accommodation	Room 8		98 m²					98 m²
Accommodation	Room 9		67 m²					67 m²
Accommodation	Storage		7 m²					7 m²
Accommodation	Vertical circulation		29 m²					29 m²
Accommodation	Circulation		21 m²					21 m²
		222 m²	0 m²	0 m²	0 m²	0 m²	0 m²	222 m²
FLOOR 5								
Accommodation	Room 10		56 m²					56 m²
Accommodation	Room 11		59 m²					59 m²
Accommodation	Vertical circulation		35 m²					35 m²
Accommodation	Circulation		23 m²					23 m²
		173 m²	0 m²	0 m²	0 m²	0 m²	0 m²	173 m²
FLOOR 6								
Accommodation	Room 12		52 m²					52 m²
Accommodation	Room 13		61 m²					61 m²
Accommodation	Vertical circulation		35 m²					35 m²
Accommodation	Circulation		25 m²					25 m²
		172 m²	0 m²	0 m²	0 m²	0 m²	0 m²	147 m²
FLOOR 7								
Accommodation	Room 14		44 m²					44 m²
Accommodation	Room 15		57 m²					57 m²
Accommodation	Connection		0 m²					0 m²
Accommodation	Vertical circulation		32 m²					32 m²
Accommodation	Circulation		25 m²					25 m²
		158 m²	0 m²	13 m²	0 m²	0 m²	0 m²	146 m²
FLOOR 8								
Accommodation	Room 16		44 m²					44 m²
Accommodation	Room 17		57 m²					57 m²
Accommodation	Vertical circulation		32 m²					32 m²
Accommodation	Circulation		25 m²					25 m²
		158 m²	0 m²	0 m²	0 m²	0 m²	0 m²	158 m²
ROOFTOP								
ROOFTOP	Roof top		118 m²					118 m²
ROOFTOP	Vertical circulation		30 m²					30 m²
		148 m²	0 m²	0 m²	16 m²	0 m²	0 m²	148 m²
TOTAL		3,349 m²	250 m²	433 m²	138 m²	123 m²	222 m²	3,652 m²
TOTAL		3,599 m²		571 m²		345 m²		
TOTAL ÁREA INTERVENIDA		Incluye área construida, área descubierta, zonas comunes, Antejardín, intervención hotel existente y cubierta 4.516 m²						

PROGRAM	ROOM	WITHIN NEW PLOT		EXTENSION EXISTING PLOT		EXTENSION EXISTING PLOT		TOTAL NEW AND REFURBISHED COVERED AREA Gross
		BUILT Gross	UNCOVERED Gross	NEW BUILD Gross	NEW UNCOVERED Gross	INTERIOR REFURBISHMENT Gross	EXTENSIONS UNCOVERED REFURBISHMENT Gross	
TOTAL		3.349 m²	250 m²	433 m²	138 m²	123 m²	222 m²	3.652 m²
TOTAL		3.599 m²		571 m²		345 m²		
TOTAL ÁREA INTERVENIDA	Incluye área construida, área descubierta, zonas comunes, Antejardín, intervención hotel existente y cubierta	4.516 m²						


INICIO FASE 2
ANTEPROYECTO

REFERENTES INTERIOR

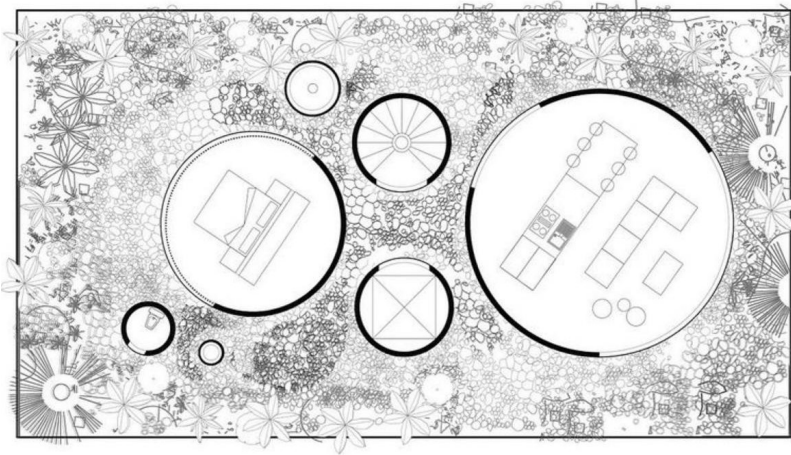

CRONOGRAMA

CRONOGRAMA TRABAJO

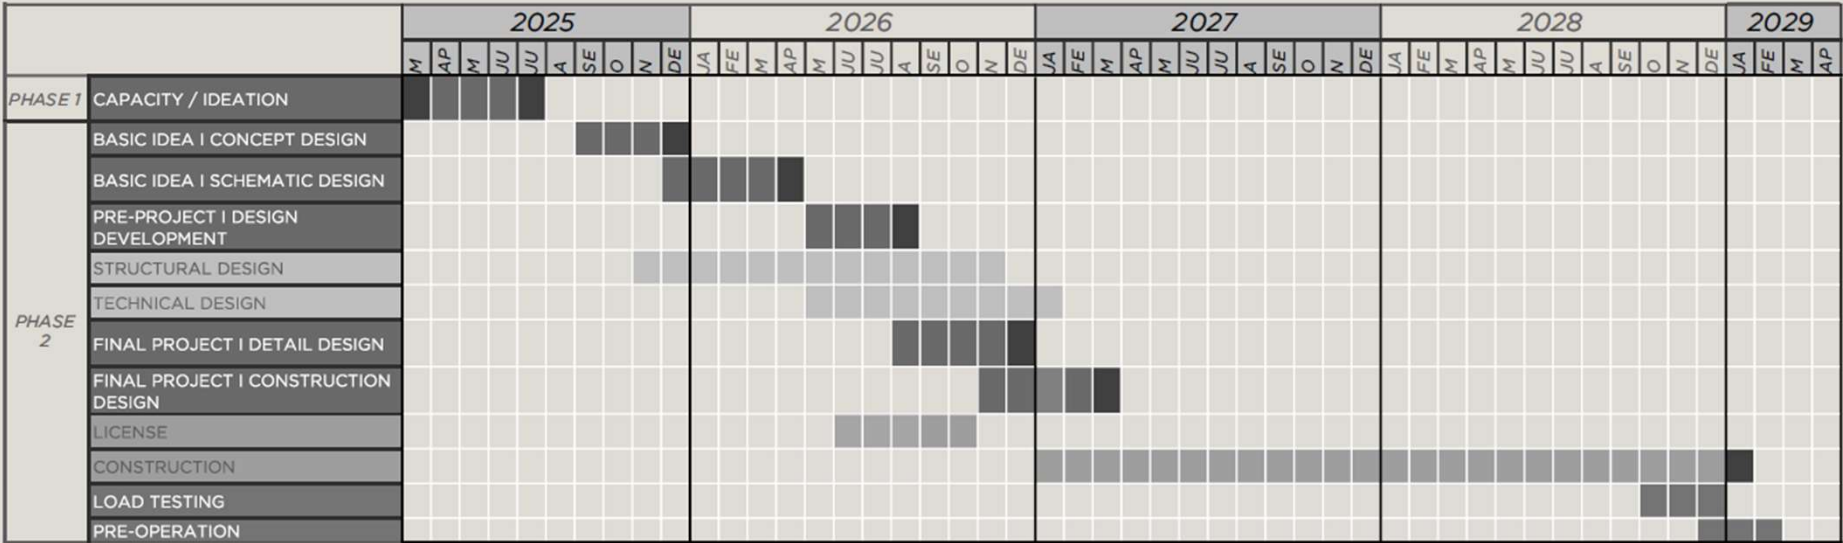

C L I C K · K O A L O